

Разрешение		Обозначение	ПС-70/2-10-С2.9.3.2-АР1		
439-25		Наименование объекта строительства	Таманский терминал навалочных грузов. Этап 1. Конвейерная галерея минеральных удобрений ГК-15 (тит. С2.9.3.2)		
Изм.	Лист	Содержание изменения		Код	Примечание
Изменение 2 внесено на основании ЗВИ-С2.9.3.2-АР1-ИС-000482. По договору ПС-251/2-25					
2	1	В ведомости рабочих чертежей основного комплекта внесены отметки об изменениях.		1.1	Зам.
2	2	В общие указания внесены отметки об изменениях.		1.1	Зам.
2	3	На плане замаркирован узел 12 между складом минеральных удобрений и ГК-15		1.1	Зам.
2	5	На разрезе 1-1 замаркирован узел 11 между складом минеральных удобрений и ГК-15		1.1	Зам.
2	18	Добавлены узлы 11, 12		1.1	Зам.
2	21	В спецификации изделий и материалов добавлены фасонные элементы ФЭ-9, ФЭ-11, ФЭ-12, ФЭ-13.		1.1	Зам.

Требуется корректировка сметной документации.

Согласовано:					Парфенов				25.25				
Н.Н. контроль													
Изм. внес					Недев				12.25				
Составил					Недев				12.25				
ГИП					Пряников				12.25				
Утв.					Агакишиев				12.25				
ООО "ЮТП"										Лист		Листов	
												1	

Согласовано	Курицын	Прокотчук	Чернов	12.20	12.20	12.20
	Гл. конструктор	Рук.подразд.	Нач.отдела	12.20	12.20	12.20
	Кириллов	Старкина	Федоров	12.20	12.20	12.20
	Рук.подразд.	Нач.сектора	Нач.отдела	12.20	12.20	12.20
	Взам. инв. N	Подпись и дата	Инв. N подл.			
		11.25	72831220327			

Ведомость рабочих чертежей основного комплекта

Лист	Наименование	Примечание
1	Общие данные	Изм.1,2(Зам.)
2	Общие данные	Изм.1,2(Зам.)
3	План конвейерной галереи	Изм.1,2(Зам.)
4	План кровли	Изм.1(Зам.)
5	Разрез 1-1	Изм.1,2(Зам.)
6	Разрез 2-2	Изм.1(Зам.)
7	Фрагмент 1 разреза	Изм.1(Зам.)
8	Фасад 1-2/А	Изм.1(Зам.)
9	Фасад 2-1/Б	Изм.1(Зам.)
10	Фасад 1-2/В	Изм.1(Зам.)
11	Фасад 2-1/Г	Изм.1(Зам.)
12	Цветовое решение фасадов	Изм.1(Зам.)
13	Схемы раскладки стеновых ограждающих конструкций в осях 1-2/А; 1-2/В; А-Г/1	Изм.1(Зам.)
14	Схемы раскладки стеновых ограждающих конструкций в осях 2-1/Б; 2-1/Г	Изм.1(Зам.)
15	Схема раскладки кровельных ограждающих конструкций	Изм.1(Зам.)
16	Узлы 1-2, 10	Изм.1(Зам.)
17	Узлы 3-5	Изм.1(Зам.)
18	Узлы 6-9, 11, 12	Изм.1,2(Зам.)
19	План площадок обслуживания на отм. 78,090	Изм.1(Зам.)
20	План площадок обслуживания на отм. 82,270	Изм.1(Зам.)
21	Спецификация изделий и материалов	Изм.1,2(Зам.)

Ведомость спецификаций

Лист	Наименование	Примечание
3	Спецификация элементов заполнения проемов дверей	
11	Спецификация элементов ограждающих конструкций	
14	Спецификация к схемам раскладки стеновых ограждающих конструкций	
15	Спецификация к схемам раскладки кровельных ограждающих конструкций	
21	Спецификация изделий и материалов	

Ведомость ссылочных и прилагаемых документов

Обозначение	Наименование	Примечание
	Ссылочные документы	
ГОСТ 24045-2016	Профили стальные листовые гнутые с трапециевидными гофрами для строительства. Технические условия	


Условные обозначения:

- д.ш.
- деформационный шов
-
- профилированный лист
-
- светопрозрачное заполнение проемов (профилированный поликарбонат)
-
- направление движения, ось конвейера
-
- ходовые трапы (настил с поперечинами)
- 1
- ось другого объекта

Ведомость основных комплектов рабочих чертежей марки АР

Обозначение	Наименование	Примечание
ПС-70/2-10-С2.9.3.2-АР	Конвейерная галерея перегрузочного комплекса минеральных удобрений ГК-15 (тит. С2.9.3.2)	аннулирован
ПС-70/2-10-С2.9.3.2-АР1	Конвейерная галерея минеральных удобрений ГК-15 (тит. С2.9.3.2)	

Ситуационный план

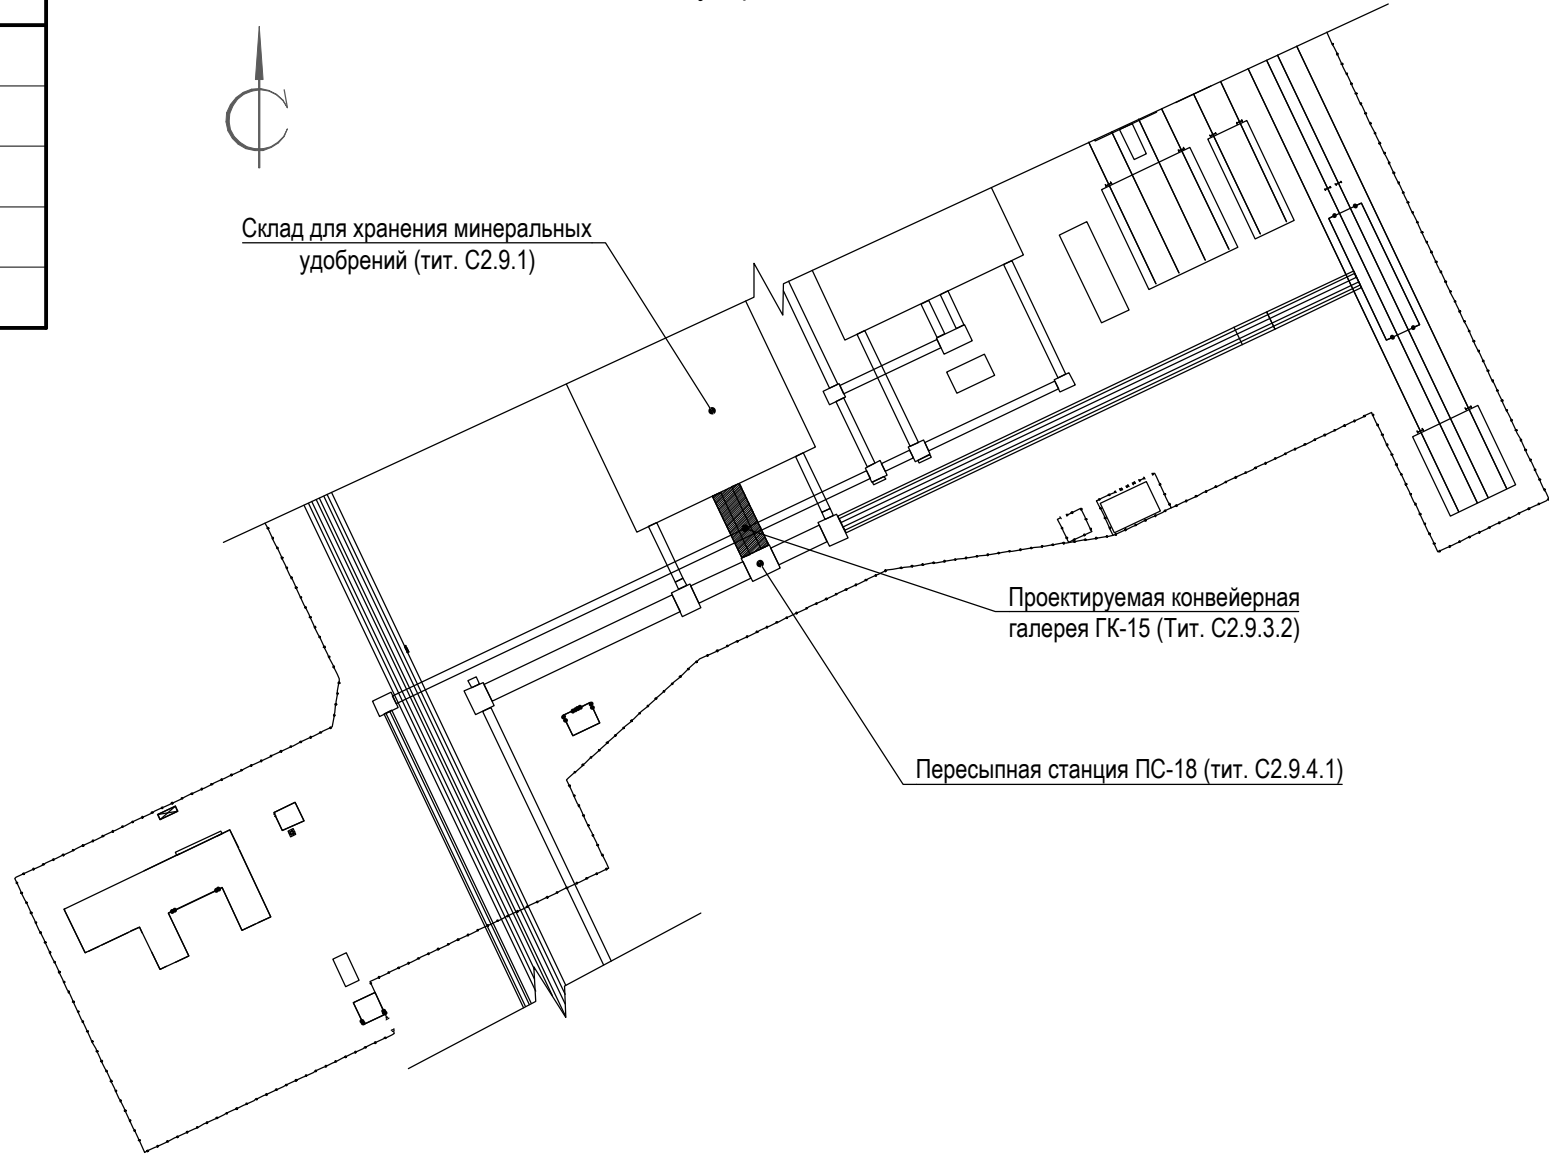

						ПС-70/2-10-С2.9.3.2-АР1			
2	-	Зам.	439-25	12.25		Таманский терминал навалочных грузов. Этап 1			
1	-	Зам.	1617-20	12.20					
Изм.	Колуч	Лист	Недок	Подпись	Дата				
Разработал	Недев			12.25		Конвейерная галерея минеральных удобрений ГК-15 (тит. С2.9.3.2)	Стадия	Лист	Листов
Проверил	Зырянов			12.25			Р	1	21
Нач. отдела	Зеленева			12.25					
Н. контроль	Парфёнов			12.25		Общие данные		ООО "Югтерминалпроект"	
ГИП	Пряников			12.25					

Инов. N подл.	Подпись и дата	Взам. инв. N

Общие указания

- 1
- Рабочие чертежи данного комплекта разработаны на основании задания технологического сектора ООО "ЮТП".
- 2
- Настоящая рабочая документация разработана в соответствии с действующими техническими регламентами, нормами, правилами и стандартами Российской Федерации, в том числе предусматривающими мероприятия, обеспечивающие взрывопожарную и пожарную безопасность при эксплуатации объектов и сооружений.
- 3
- Перечень национальных стандартов, технические регламентов и нормативных документов:

Технический регламент о требованиях пожарной безопасности;
Технический регламент о безопасности зданий и сооружений;
Специальные технические условия на проектирование и строительство, в части обеспечения пожарной безопасности объекта: «Таманский терминал навалочных грузов», расположенного по адресу: Краснодарский край, Темрюкский район, морской порт "Тамань".
СП 1.13130.2020 «Эвакуационные пути и выходы»;
СП 2.13130.2020 «Обеспечение огнестойкости объектов защиты»;
СП 4.13130.2013 «Ограничение распространения пожара на объектах защиты»;
СП 56.13330.2011 «Производственные здания»;
СП 43.13330.2012 «Сооружения промышленных предприятий»;
СП 37.13330.2012 «Промышленный транспорт»;
СП 28.13330.2017 «Защита строительных конструкций от коррозии»;
СП 14.13330.2018 «Строительство в сейсмических районах»
СП 17.13330.2017 «Кровли»;
СП 52.13330.2016 «Естественное и искусственное освещение»;
СП 29.13330.2011 «Полы»;
СП 51.13330.2011 «Защита от шума»;
СП 50.13330.2012 «Тепловая защита зданий»;
СП 23-101-2004 «Проектирование тепловой защиты зданий»;
СП 131.13330.2018 «Строительная климатология»;
СНKK 23-302-2000 (ТСН 23-319-2000 Краснодарского края) «Энергетическая эффективность жилых и общественных зданий. Нормативы по теплозащите зданий»;
СанПиН 2.2.4.548-96 «Гигиенические требования к микроклимату производственных помещений»;
СП 71.13330.2017 «Изоляционные и отделочные покрытия»;
ГОСТ 21.501-2018 «Правила выполнения рабочей документации архитектурных и конструктивных решений».
- 4
- Все высотные отметки в проекте приняты абсолютными в Балтийской системе высот. Координатные привязки и расположение сооружения на площадке строительства смотреть раздел ГП.
- 5
- В рабочих чертежах использованы известные конструкции и решения, не требующие проверки на патентную чистоту.
- 6
- Примененные в проекте конструкции имеют предел огнестойкости, класс пожарной опасности, требуемые по № 123-ФЗ для зданий IV степени огнестойкости, класса конструктивной пожарной опасности С0 в соответствии с № 123-ФЗ, табл. 21, 22.

Уровень ответственности здания - нормальный в соответствии с № 384-ФЗ, Ст. 4, п. 7.

Класс функциональной пожарной опасности здания - Ф 5.1 в соответствии с № 123-ФЗ, Ст. 32.

Категория здания по взрывопожарной и пожарной опасности - В в соответствии с СП 12.13130.2009, п. 6.

Класс пожарной опасности строительных конструкций - К0 в соответствии с № 123-ФЗ, табл. 22.

Этажность здания - 1 этаж, в соответствии с СП 56.13330.2011. п. 4.11.
- 7
- Степень агрессивного воздействия внутренней среды - сильноагрессивная (в соответствии с технологическим заданием).

Климатический район - IIIБ (в соответствии с СП 131.13330.2012, Приложение А).

- 8
- Характеристика стеновых и кровельных материалов.

Кровлю выполнить совмещенной односкатной (max i=25%), с наружным организованным водостоком, неутепленной, из профилированного листа Н-75-750-0,8 ПВДФ ГОСТ 24045-2016 (или аналог). Предусмотреть ограждение Roof Systems PRESTIGE Н-600 ТУ 5262-001-84344822-2019 (или аналог) и страховочные крюки в соответствии с ПС-70/2-10-С2.9.3.2-КМ4.

Наружные ограждающие стены выполнить из профилированного листа НС-44-1000-0,8 ПВДФ ГОСТ 24045-2016 (или аналог).

Светопрозрачные вставки в наружных ограждающих стенах выполнить из профилированных листов монолитного поликарбоната марки "BORREX" ПЛМПКГ ТУ 2291-002-73658121-2009 (или аналог).

Стальные профилированные листы крепить к конструкциям самосверлящими шурупами **HE5-R-Z19 5.5x38** (или аналог) в каждую волну, а между собой самосверлящими шурупами **HE4-R-Z16 5.5x25** (или аналог) с шагом 300 мм. Листы профилированного поликарбоната крепить по аналогии со стальными профлистами через волну.

Возможна замена S-MD55GZ 5,5Х40 на шурупы, приведенные в таблице:

	Шурупы S-MD 55 GZ (горяч.цинк)	Шурупы S-MD 55S (нержавейка) А4
Тех. решение. Расчеты	+	+
Коррозийная стойкость	3 года	50 лет
Скорость монтажа	Х	Х
Стоимость	Х	5Х
Демонтаж	Да	ДА
Срок поставки	5-7 дней	5 недель
Документы на сейсмику	нет данных	нет данных

Толщина, материал покрытия и другие характеристики профилированных листов должны быть подтверждены производителем исходя из климатических условий и степени агрессивного воздействия внутренней среды сооружения.
- 9
- Перечень видов работ, которые оказывают влияние на безопасность здания и для которых необходимо составлять акты на скрытые работы:

- установка дверных блоков (крепление коробок, их гидроизоляция, защитная обработка);

- устройство кровельного покрытия профилированными листами;

- устройство водосточного желоба.
- 10
- Безопасность пребывания людей в здании обеспечивается санитарно-эпидемиологическими и микроклиматическими условиями: отсутствием вредных веществ в воздухе помещений выше предельно допустимых концентраций, отсутствием выше допустимых значений шума, вибрации, статического электричества и излучений в соответствии с требованиями СанПиН 2.2.4.548, СП 2.2.2.1327 и действующих гигиенических нормативов.
- 11
- В процессе строительства и эксплуатации здания должны быть выполнены водозащитные мероприятия, обеспечивающие надежный водоотвод от здания:

- планировка территории должна обеспечивать надежный сток атмосферных вод в ливнесточную канализацию;

- отвод воды с кровли здания выполнить организованным.
- 12
- При производстве работ необходимо соблюдать правила техники безопасности согласно требованиям СНиП 12-03-2001 ч. 1 и СНиП 12-04-2002 ч. 2 "Техника безопасности в строительстве".
- 13
- Цветовое решение фасадов приведено на листе 12.

- 14
- Места прохода металлических конструкций сквозь стеновой и кровельный профилированный лист заделать гидроизоляционной самоклеящейся битумно-полимерной лентой NICOBAND шириной 150-200 мм, цвет защитной пленки - серебристый, СТО 72746455-3.1.6-2014 (или аналог). Работы по подготовке поверхности и монтажу производить в соответствии с рекомендациями и инструкциями компании-изготовителя.
- 15
- Состав полов см. в комплекте ПС-70/2-10-С2.9.3.2-КМ4.
- 16
- Проход инженерных коммуникаций диаметром до 150 мм через ограждающие конструкции выполняется по месту.
- 17
- Перед заказом у производителя дверных блоков необходимо выполнить замеры проемов. Установку блоков необходимо делать по монтажной схеме производителя.

Размеры в чертежах марки АР ставятся по проему.
- 18
- В случае обнаружения на объекте строительства несоответствий проектным решениям необходимо обратиться к ген. проектировщику за решением. Заказ материала выполнить после решения данного несоответствия.
- 19
- С выпуском данного комплекта ранее выданный комплект чертежей ПС-70/2-10-С2.9.3.2-АР (разработанный ООО "МСТ") аннулируется.
- 20
- Изменение 1 внесено в связи с выпуском измененных конструкций фахверка в комплекте ПС-70/2-10-С2.9.3.2-КМ4 Изм.1, выпуском стальных труб водостока в комплекте ПС-70/2-10-С2.9.3.2-КМ3 Изм.1, по заданию отдела ПБ №10250 от 19.11.2020 на размещение шкафов пожарного инвентаря и заданию отдела ЭТО №9268 от 16.11.2020 на расположение кабельных конструкций, а также в связи с корректировкой наименования объекта строительства в штампе
- 21
- Изменение 2 внесено на основании ЗВИ-С2.9.3.2-АР1-ИС-000482. По договору ПС-251/2-25


2.1

						ПС-70/2-10-С2.9.3.2-АР1			
2	1	Изм.	439-25		12.25	Таманский терминал навалочных грузов. Этап 1			
1	-	Зам.	1617-20		12.20				
Изм.	Копуч	Лист	Недок	Подпись	Дата				
Разработал	Тимофеенко				05.26	Конвейерная галерея минеральных удобрений ГК-15 (тит. С2.9.3.2)	Стадия	Лист	Листов
Проверил							Р	2	
Нач. отдела									
						Общие данные	ООО "Гранд Вэй"		
Н. контроль									
ГИП									

Инд. N подл.	783/20327
Подпись и дата	11/25
Взам. инв. N	

Склад минеральных удобрений
см. ПС-70/2-10-С2.9.1-АР

План конвейерной галереи

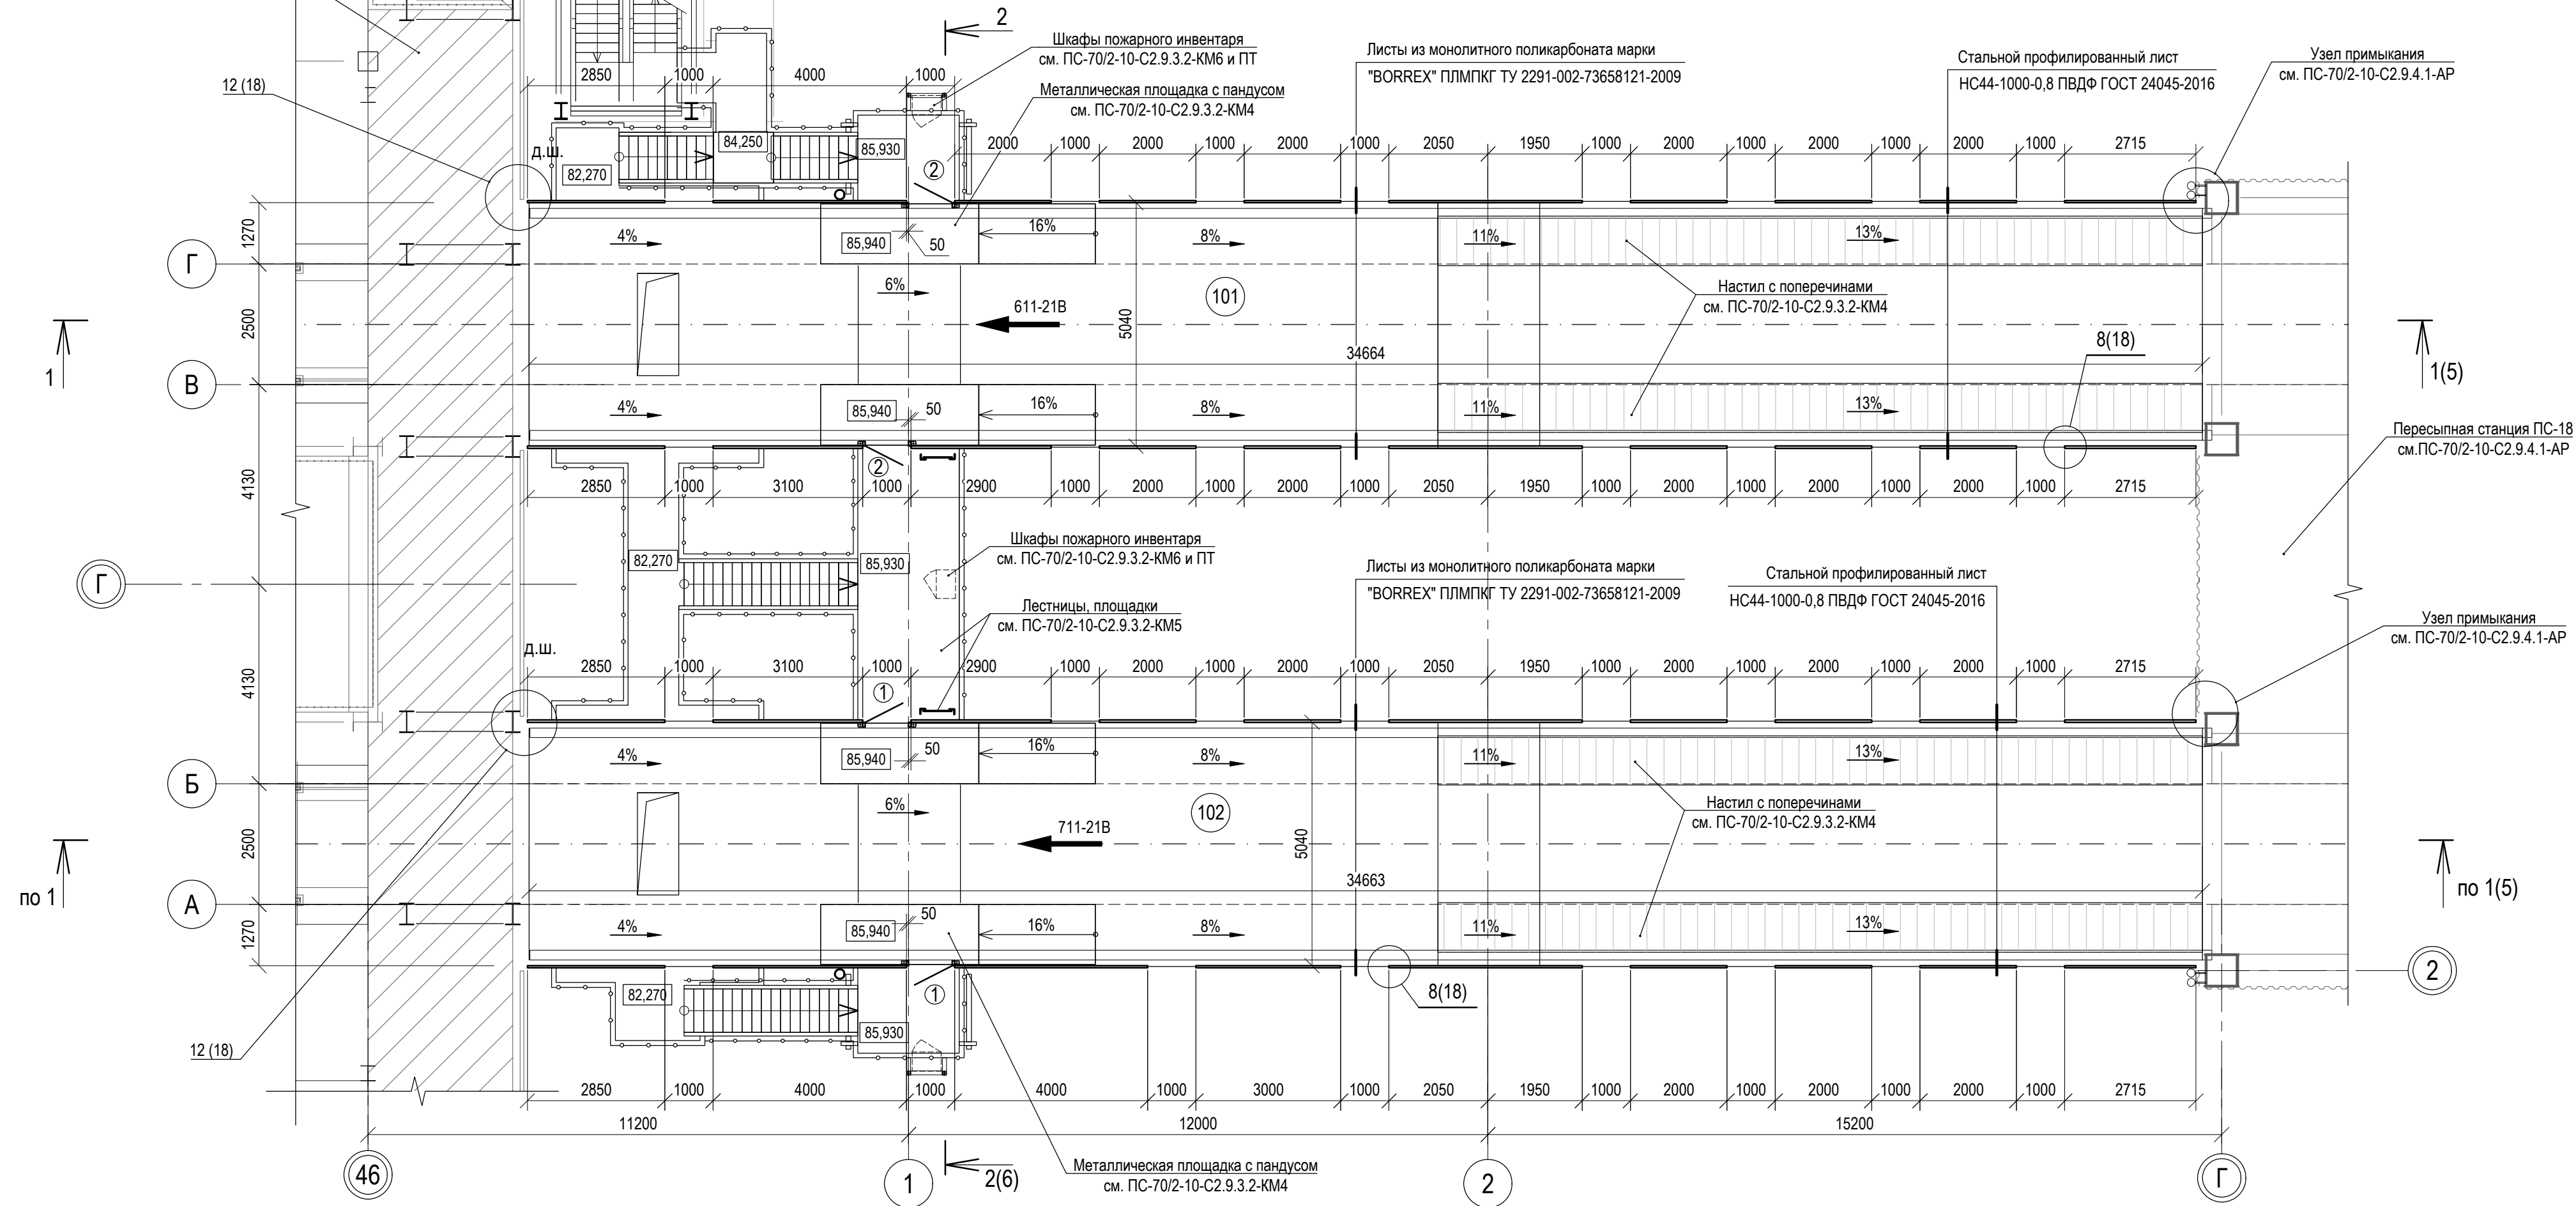

Спецификация элементов заполнения проемов дверей

Поз.	Обозначение	Наименование	Кол. по фасадам					Масса, ед., кг	Примечание
			1-2/А	2-1/Б	1-2/В	2-1/Г	Всего		
1	ГОСТ 31173-2016	ДСН, А, Оп, Пр, Прг, Н, П2лс, М3, О 2100-1000*	1	1	-	-	2		RAL9006, с доводчиком (см. примечание п.2)
2	ГОСТ 31173-2016	ДСН, А, Оп, Л, Прг, Н, П2лс, М3, О 2100-1000*	-	-	1	1	2		RAL9006, с доводчиком (см. примечание п.2)


* - размеры проемов под дверные блоки, ширина монтажного зазора уточняется у производителя. Двери должны открываться наружу и снабжаться samozapirayushimsya замком, открываемым без ключа изнутри пересыпной станции. Минимальная ширина выхода в свету не менее 800 мм, минимальная высота не менее 1900 мм.

Экспликация помещений

Номер помеще-ния	Наименование	Площадь, м²	Кат. помеще-ния
101	Конвейерная галерея	175,6	В1
102	Конвейерная галерея	175,6	В1

- Общие указания см. лист 2.
- Двери должны быть выполнены в антикоррозионном исполнении согласно п.7 Общих указаний.

						ПС-70/2-10-С2.9.3.2-АР1			
2	-	Зам.	439-25	12	25	Таманский терминал навалочных грузов. Этап 1			
1	-	Зам.	1617-20	12	20				
Изм.	Копуч	Лист	№ док	Подпись	Дата	Конвейерная галерея минеральных удобрений ГК-15 (тит. С2.9.3.2)	Стадия	Лист	Листов
Разработал	Недев				12.25		Р	3	
Проверил	Зырянов				12.25				
Нач. отдела	Зеленева				12.25				
Н. контроль	Парфёнов				12.25	План конвейерной галереи	ООО "Югтерминалпроект"		
ГИП	Пряников				12.25				

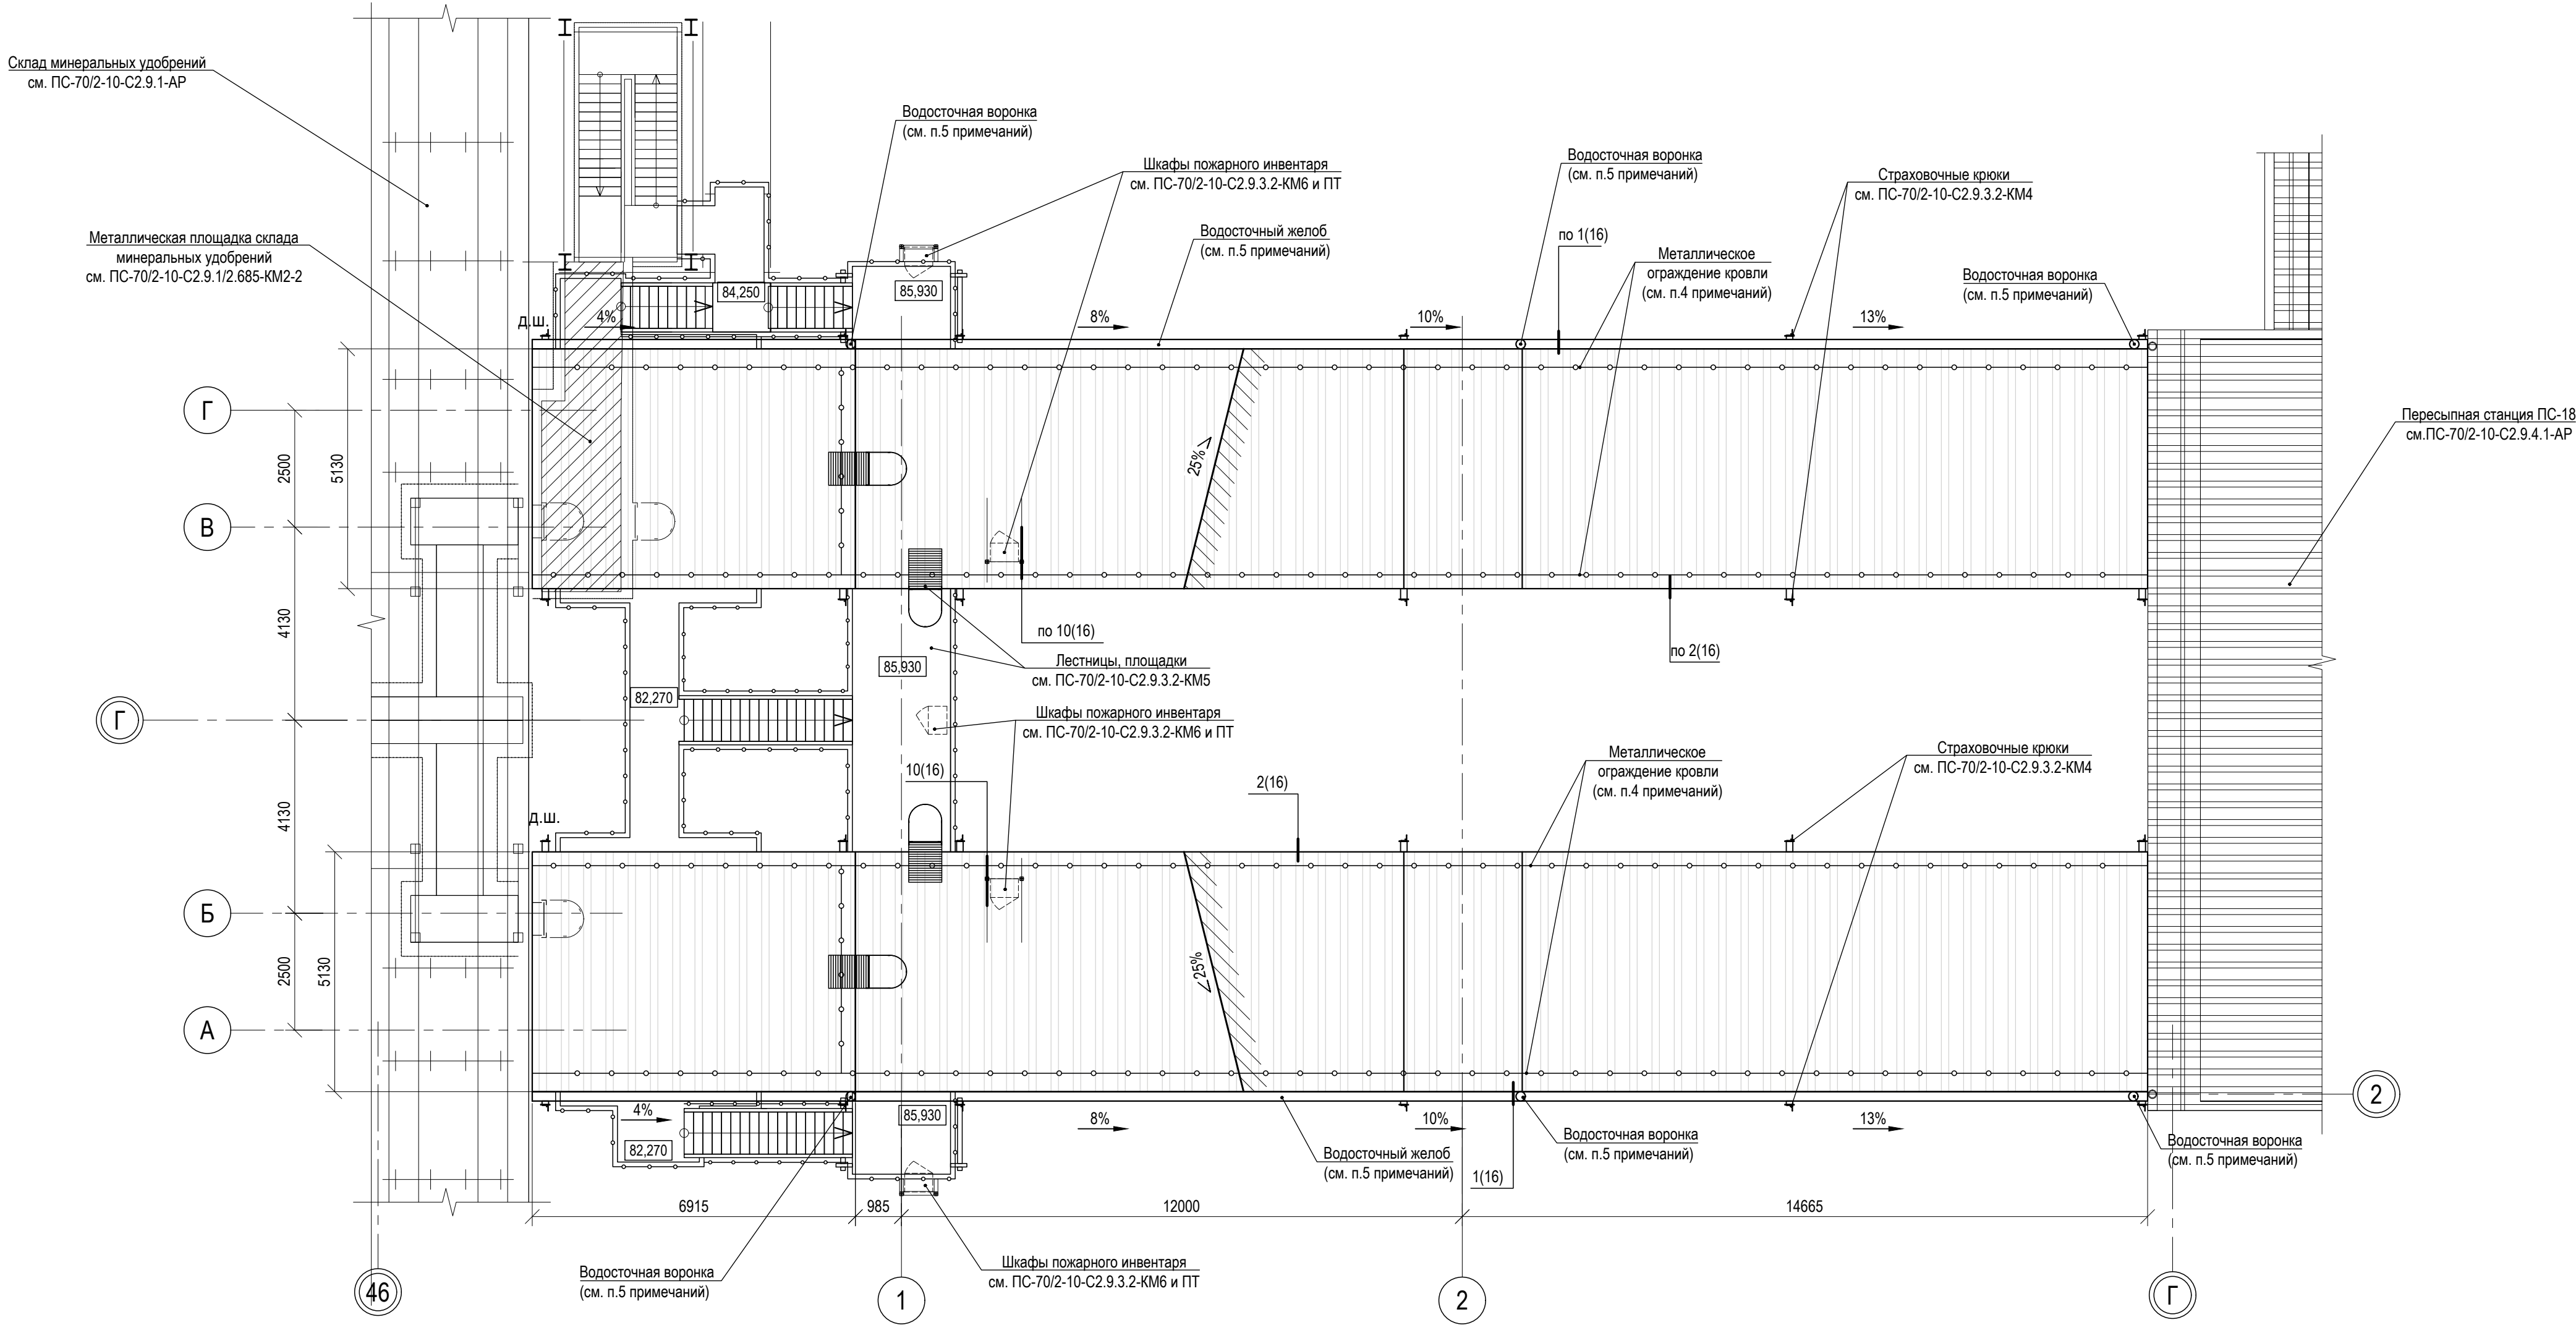

1. Общие указания см. лист 2.
2. Все узкие места, зазоры заполнить герметиком Сазиласт 13, ТУ 2513-118-32478306-2011.
3. Спецификацию элементов ограждающих конструкций см. на листе 11.
4. Ограждение кровельное Roof Systems PRESTIGE H-600 45x25 (овал) 2 трубы EURO L=3м ТУ 5262-001-84344822-2016 (или аналог), RAL 9006. Крепление ограждения выполнять в верхнюю волну через планку-переходник для профнастила Н75 к прогонам в соответствии с инструкцией по монтажу и др. техническими документами производителя.
5. Водосточная система "МП Проект" ТУ 5285-002-37144780-2012, производитель - ООО "Компания Металл Профиль" (или аналог):
 - желоб водосточный D185x3000 (RAL 7047);
 - воронка выпускная D185/150 (RAL 7047);
 - труба водосточная D150 (RAL 7047).
6. Схему раскладки кровельных ограждающих конструкций см. на листе 15.

						ПС-70/2-10-С2.9.3.2-АР1			
						Таманский терминал навалочных грузов. Этап 1			
1	-	Зам.	1617-20		12.20	Конвейерная галерея минеральных удобрений ГК-15 (тит. С2.9.3.2)	Стадия	Лист	Листов
Изм.	Копуч	Лист	Недок	Подпись	Дата		Р	4	
Разработал	Божкова				12.20				
Проверил	Силина				12.20				
Нач. отдела	Зеленеева				12.20	План кровли	ООО "Югтерминалпроект"		
Н. контроль	Фоменкова				12.20				
ГИП	Пряников				12.20				

Разрез 1-1 (3-4)

11 (18)

д.ш.

3(17)

4%

4(17)

8%

10%

13%

16%

86,300

86,200

88,040

85,940

84,915

84,680

82,270

78,090

47,950

47,950

11200

12000

15200

Металлическая лестница
см. ПС-70/2-10-С2.9.3.2-КМ5

Металлическое ограждение кровли
(см. п.4 примечаний на листе 4)

Стальной профилированный лист
Н75-750-0,8 ПВДФ ГОСТ 24045-2016
по металлическим прогонам

Металлические площадки
см. ПС-70/2-10-С2.9.3.2-КМ5

46

1

2

Г


Узел примыкания
см. ПС-70/2-10-С2.9.4.1-АР

Склад минеральных удобрений
см. ПС-70/2-10-С2.9.1-АР

					ПС-70/2-10-С2.9.3.2-AP1				
2	-	Зам.	439-25	<i>И</i>	12.25	Таманский терминал навалочных грузов. Этап 1			
1	-	Зам.	1617-20	<i>И</i>	12.20				
Изм.	Колуч	Лист	Назад	Подпись	Дата				
Разработал	Недев			<i>И</i>	12.25	Конвейерная галерея минеральных удобрений ГК-15 (тип. С2.9.3.2)	Стация	Лист	Листов
Проверил	Зырянов			<i>И</i>	12.25		Р	5	
Нач. отдела	Зеленева			<i>И</i>	12.25				
Н. контроль	Парфёнов			<i>И</i>	12.25	Разрез 1-1	ООО "Югтерминалпроект"		
Г.П.	Пряников			<i>И</i>	12.25				

Разрез 2-2 (3-4)


Склад минеральных удобрений
см. ПС-70/2-10-С2.9.1-АР

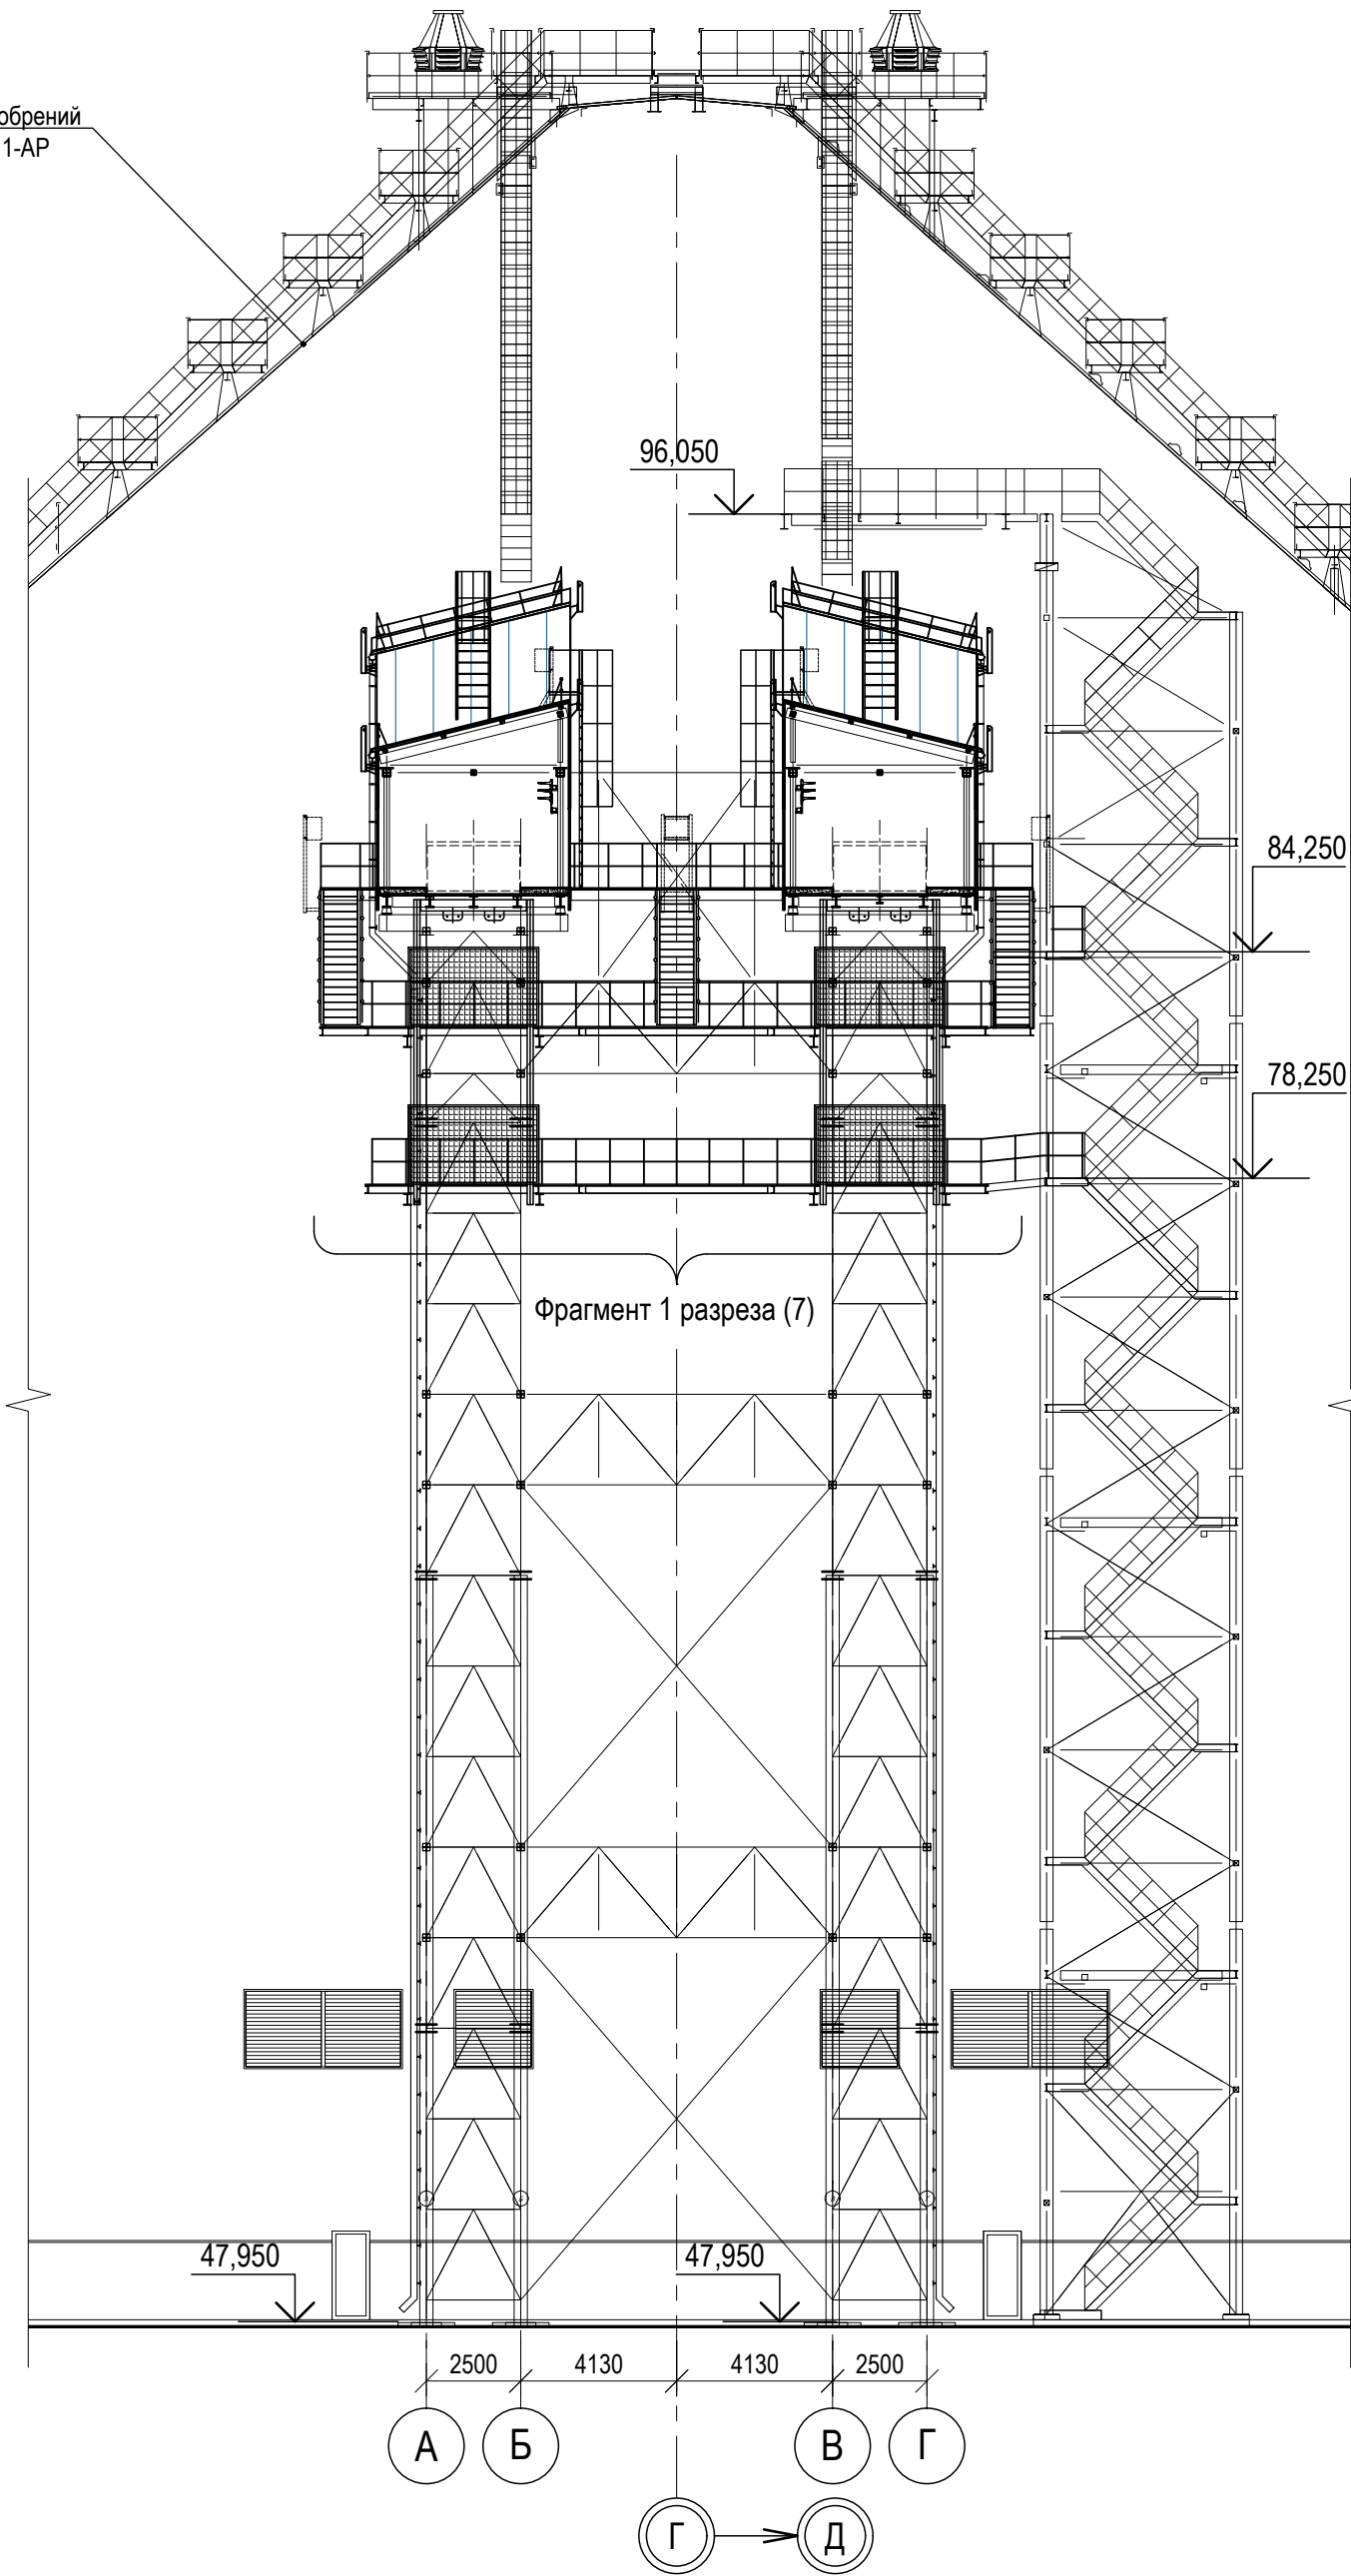

Общие указания см. лист 2.

						ПС-70/2-10-С2.9.3.2-АР1			
						Таманский терминал навалочных грузов. Этап 1			
1	-	Зам.	1617-20		12.20				
Изм.	Колуч	Лист	Недок	Подпись	Дата				
Разработал	Божкова				12.20	Конвейерная галерея минеральных удобрений ГК-15 (тит. С2.9.3.2)	Стадия	Лист	Листов
Проверил	Силина				12.20		Р	6	
Нач. отдела	Зеленева				12.20				
Н. контроль	Фоменкова				12.20	Разрез 2-2	ООО "Югтерминалпроект"		
ГИП	Пряников				12.20				

Фрагмент 1 разреза (6)

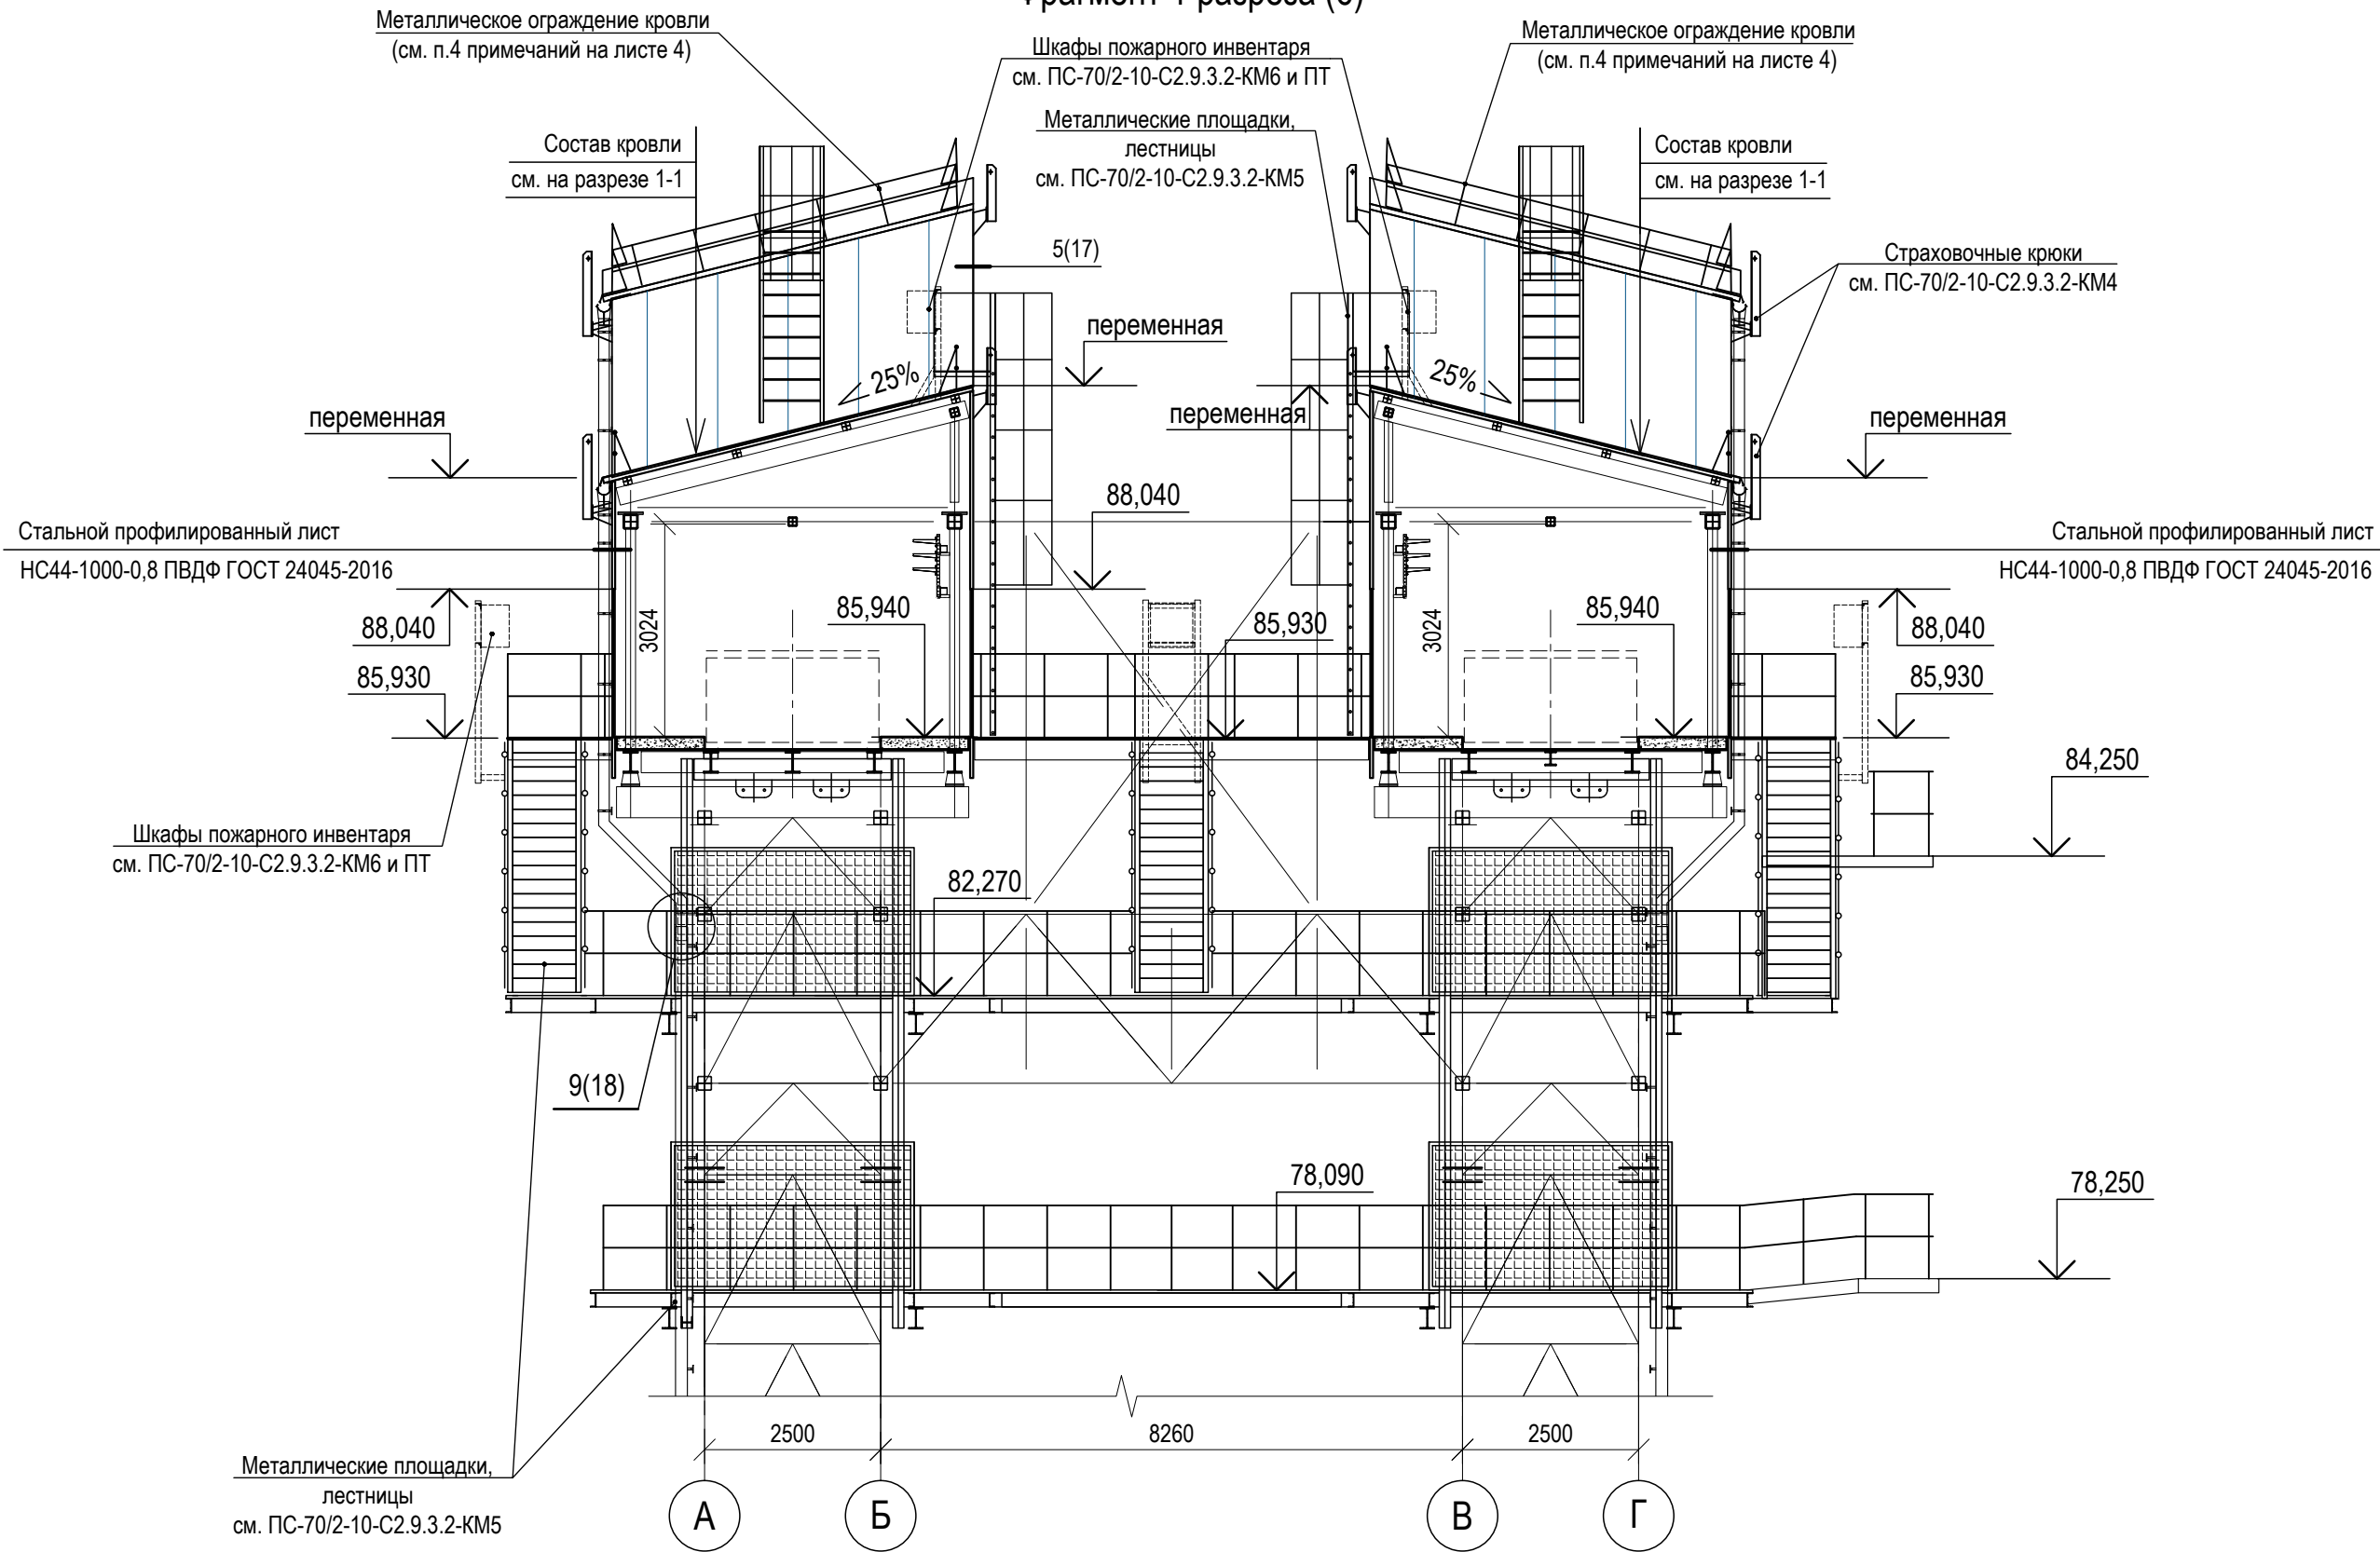

Общие указания см. лист 2.


						ПС-70/2-10-С2.9.3.2-АР1			
1	-	Зам.	1617-20		12.20	Таманский терминал навалочных грузов. Этап 1			
Изм.	Колуч	Лист	Подок	Подпись	Дата				
Разработал	Божкова			12.20	Конвейерная галерея минеральных удобрений ГК-15 (тит. С2.9.3.2)		Стадия	Лист	Листов
Проверил	Силина			12.20			Р	7	
Нач. отдела	Зеленева			12.20					
					Фрагмент 1 разреза		ООО "Югтерминалпроект"		
Н. контроль	Фоменкова			12.20					
ГИП	Пряников			12.20					

Инв. N подл.	Подпись и дата	Взам. инв. N
72931220327		

Склад минеральных удобрений
см. ПС-70/2-10-С2.9.1-АР


Фасад 1-2/А

Пересыпная станция ПС-18
см. ПС-70/2-10-С2.9.4.1-АР

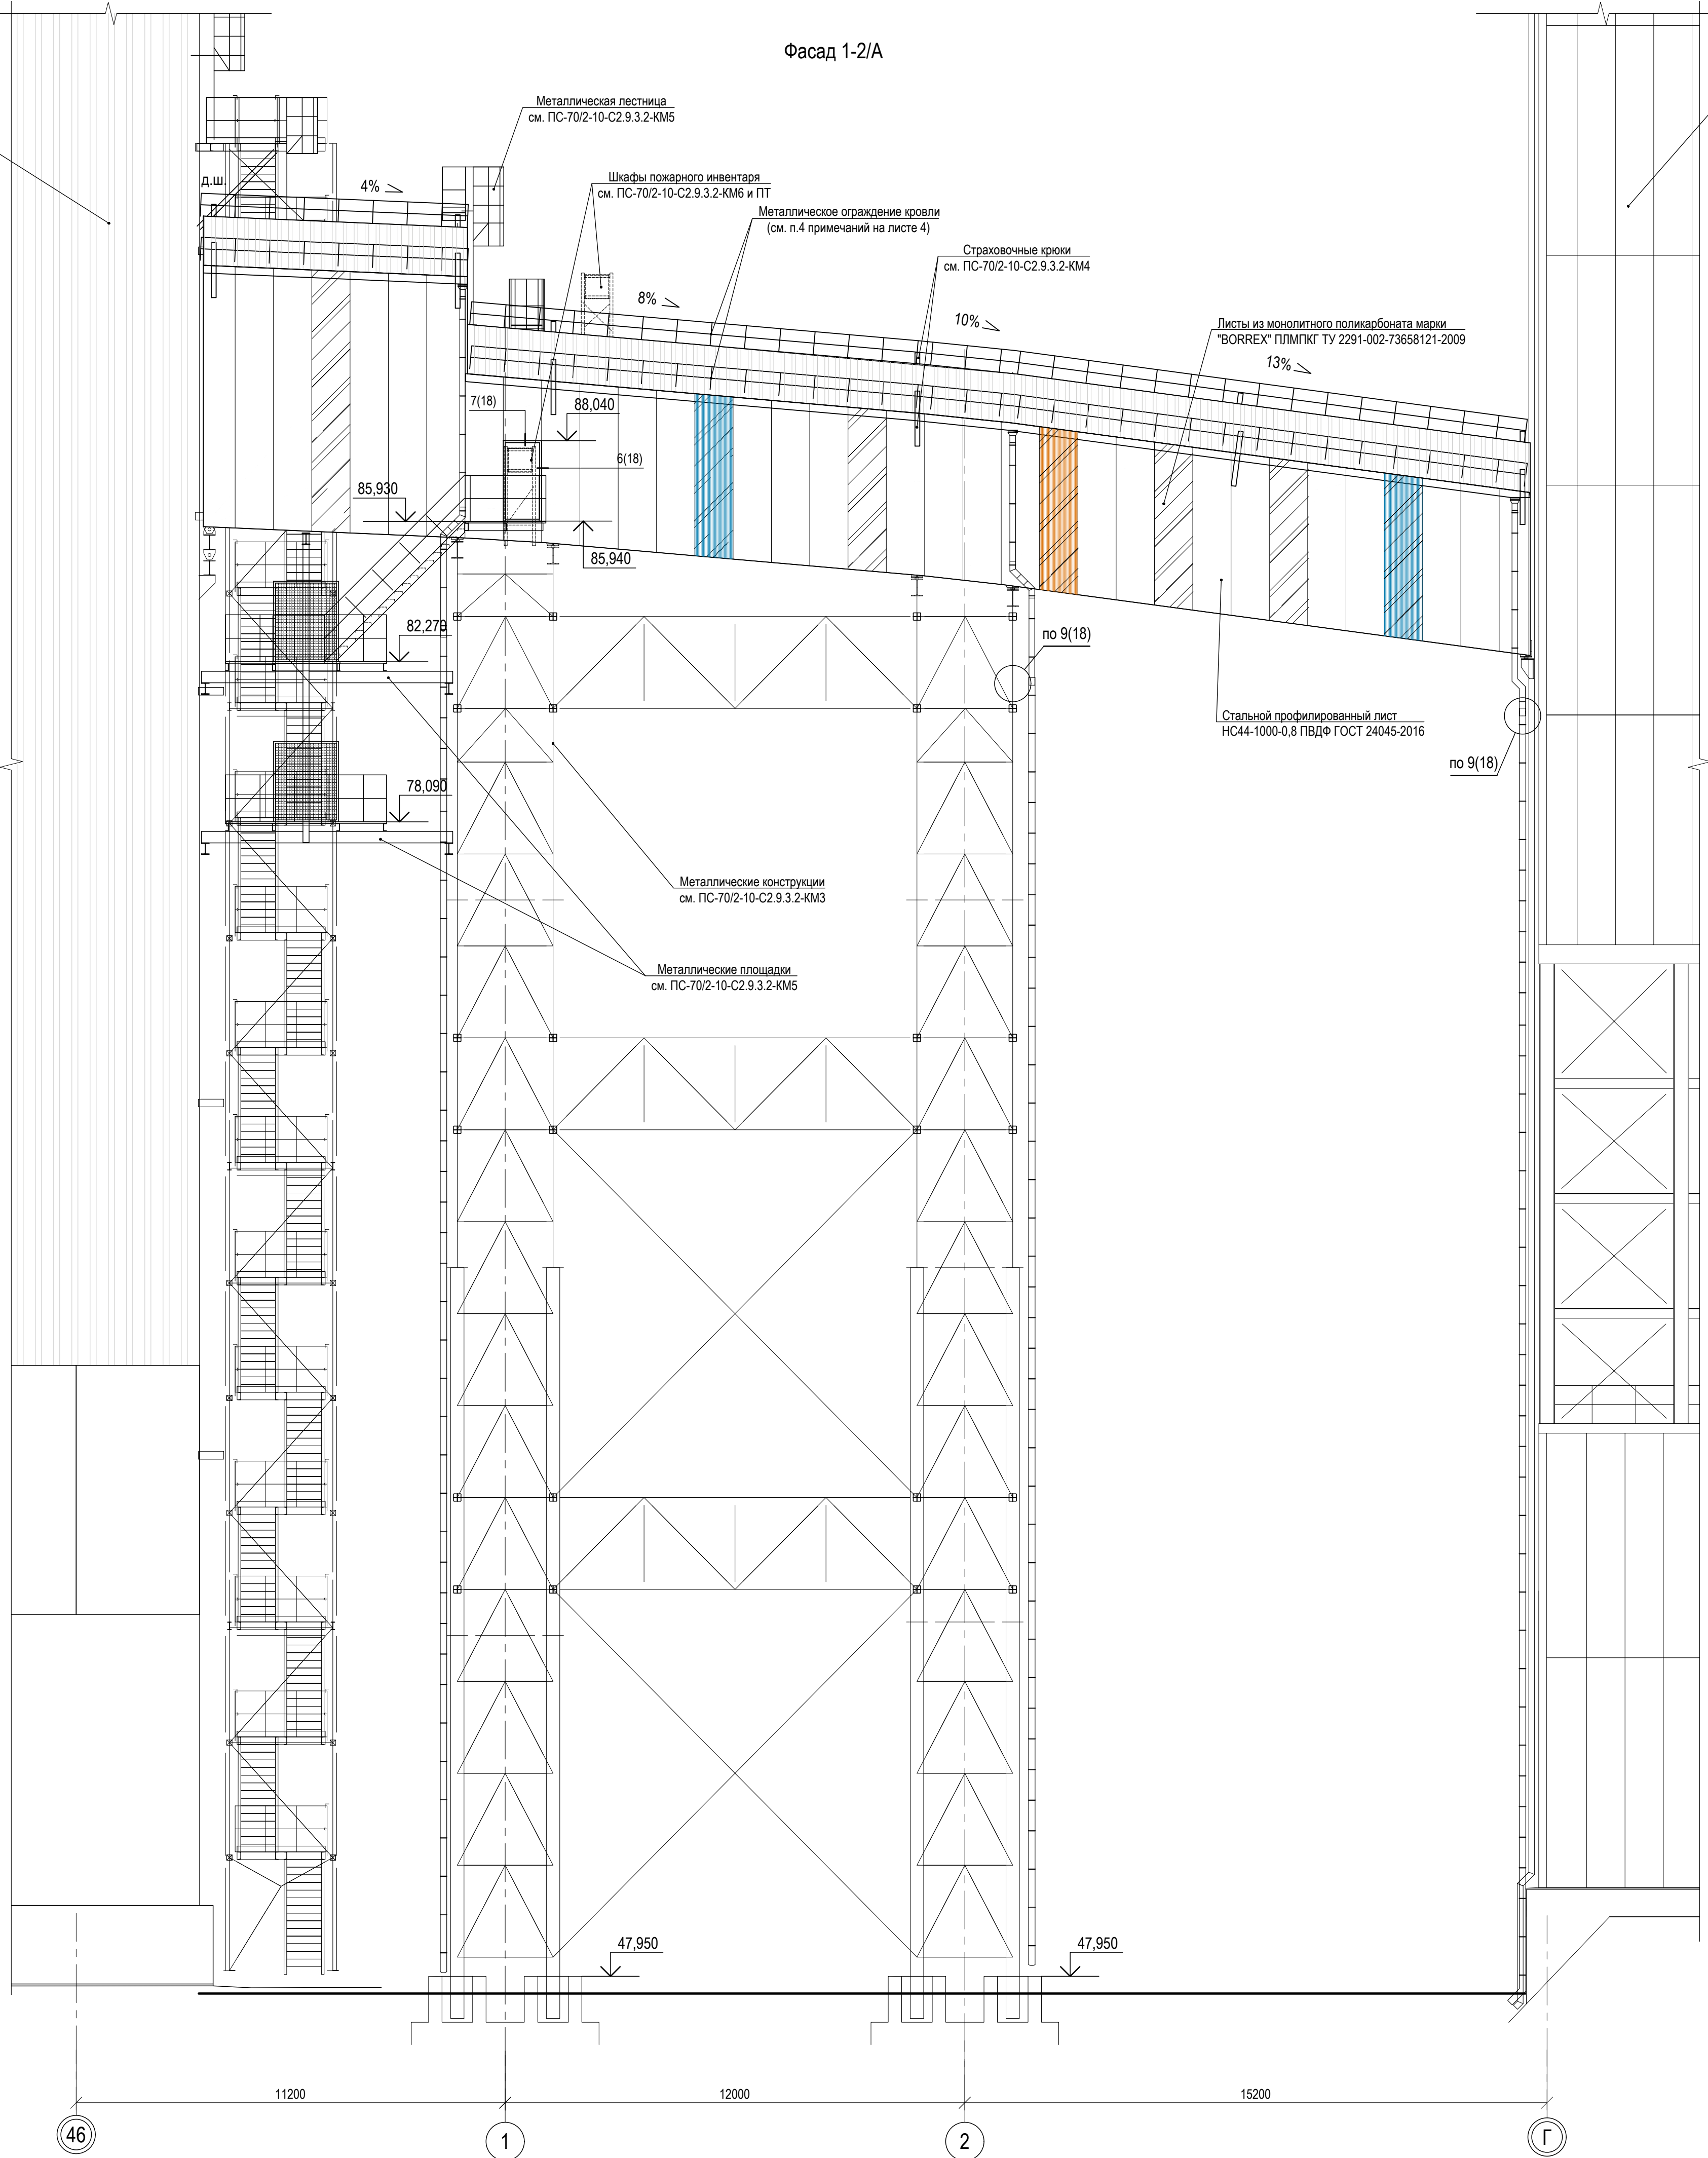

- Общие указания см. лист 2.
- Схемы раскладки стеновых ограждающих конструкций см. на листах 13-14.
- Спецификацию элементов ограждающих конструкций см. на листе 11.

						ПС-70/2-10-С2.9.3.2-АР1			
1	-	Зам.	1617-20	<i>В.П.</i>	12.20	Таманский терминал навалочных грузов.			
		Лист	Недрж	Подпись	Дата	Этап 1			
Изм.	Колуч					Конвейерная галерея минеральных удобрений ГК-15 (тит. С2.9.3.2)	Стадия	Лист	Листов
Разработал		Божкова		<i>В.П.</i>	12.20		Р	8	
Проверил		Силина		<i>В.П.</i>	12.20				
Нач. отдела		Зеленева		<i>В.П.</i>	12.20				
Н. контроль		Фоменова		<i>В.П.</i>	12.20	Фасад 1-2/А	ООО "Ютерминалпроект"		
ГИП		Пряников		<i>В.П.</i>	12.20				

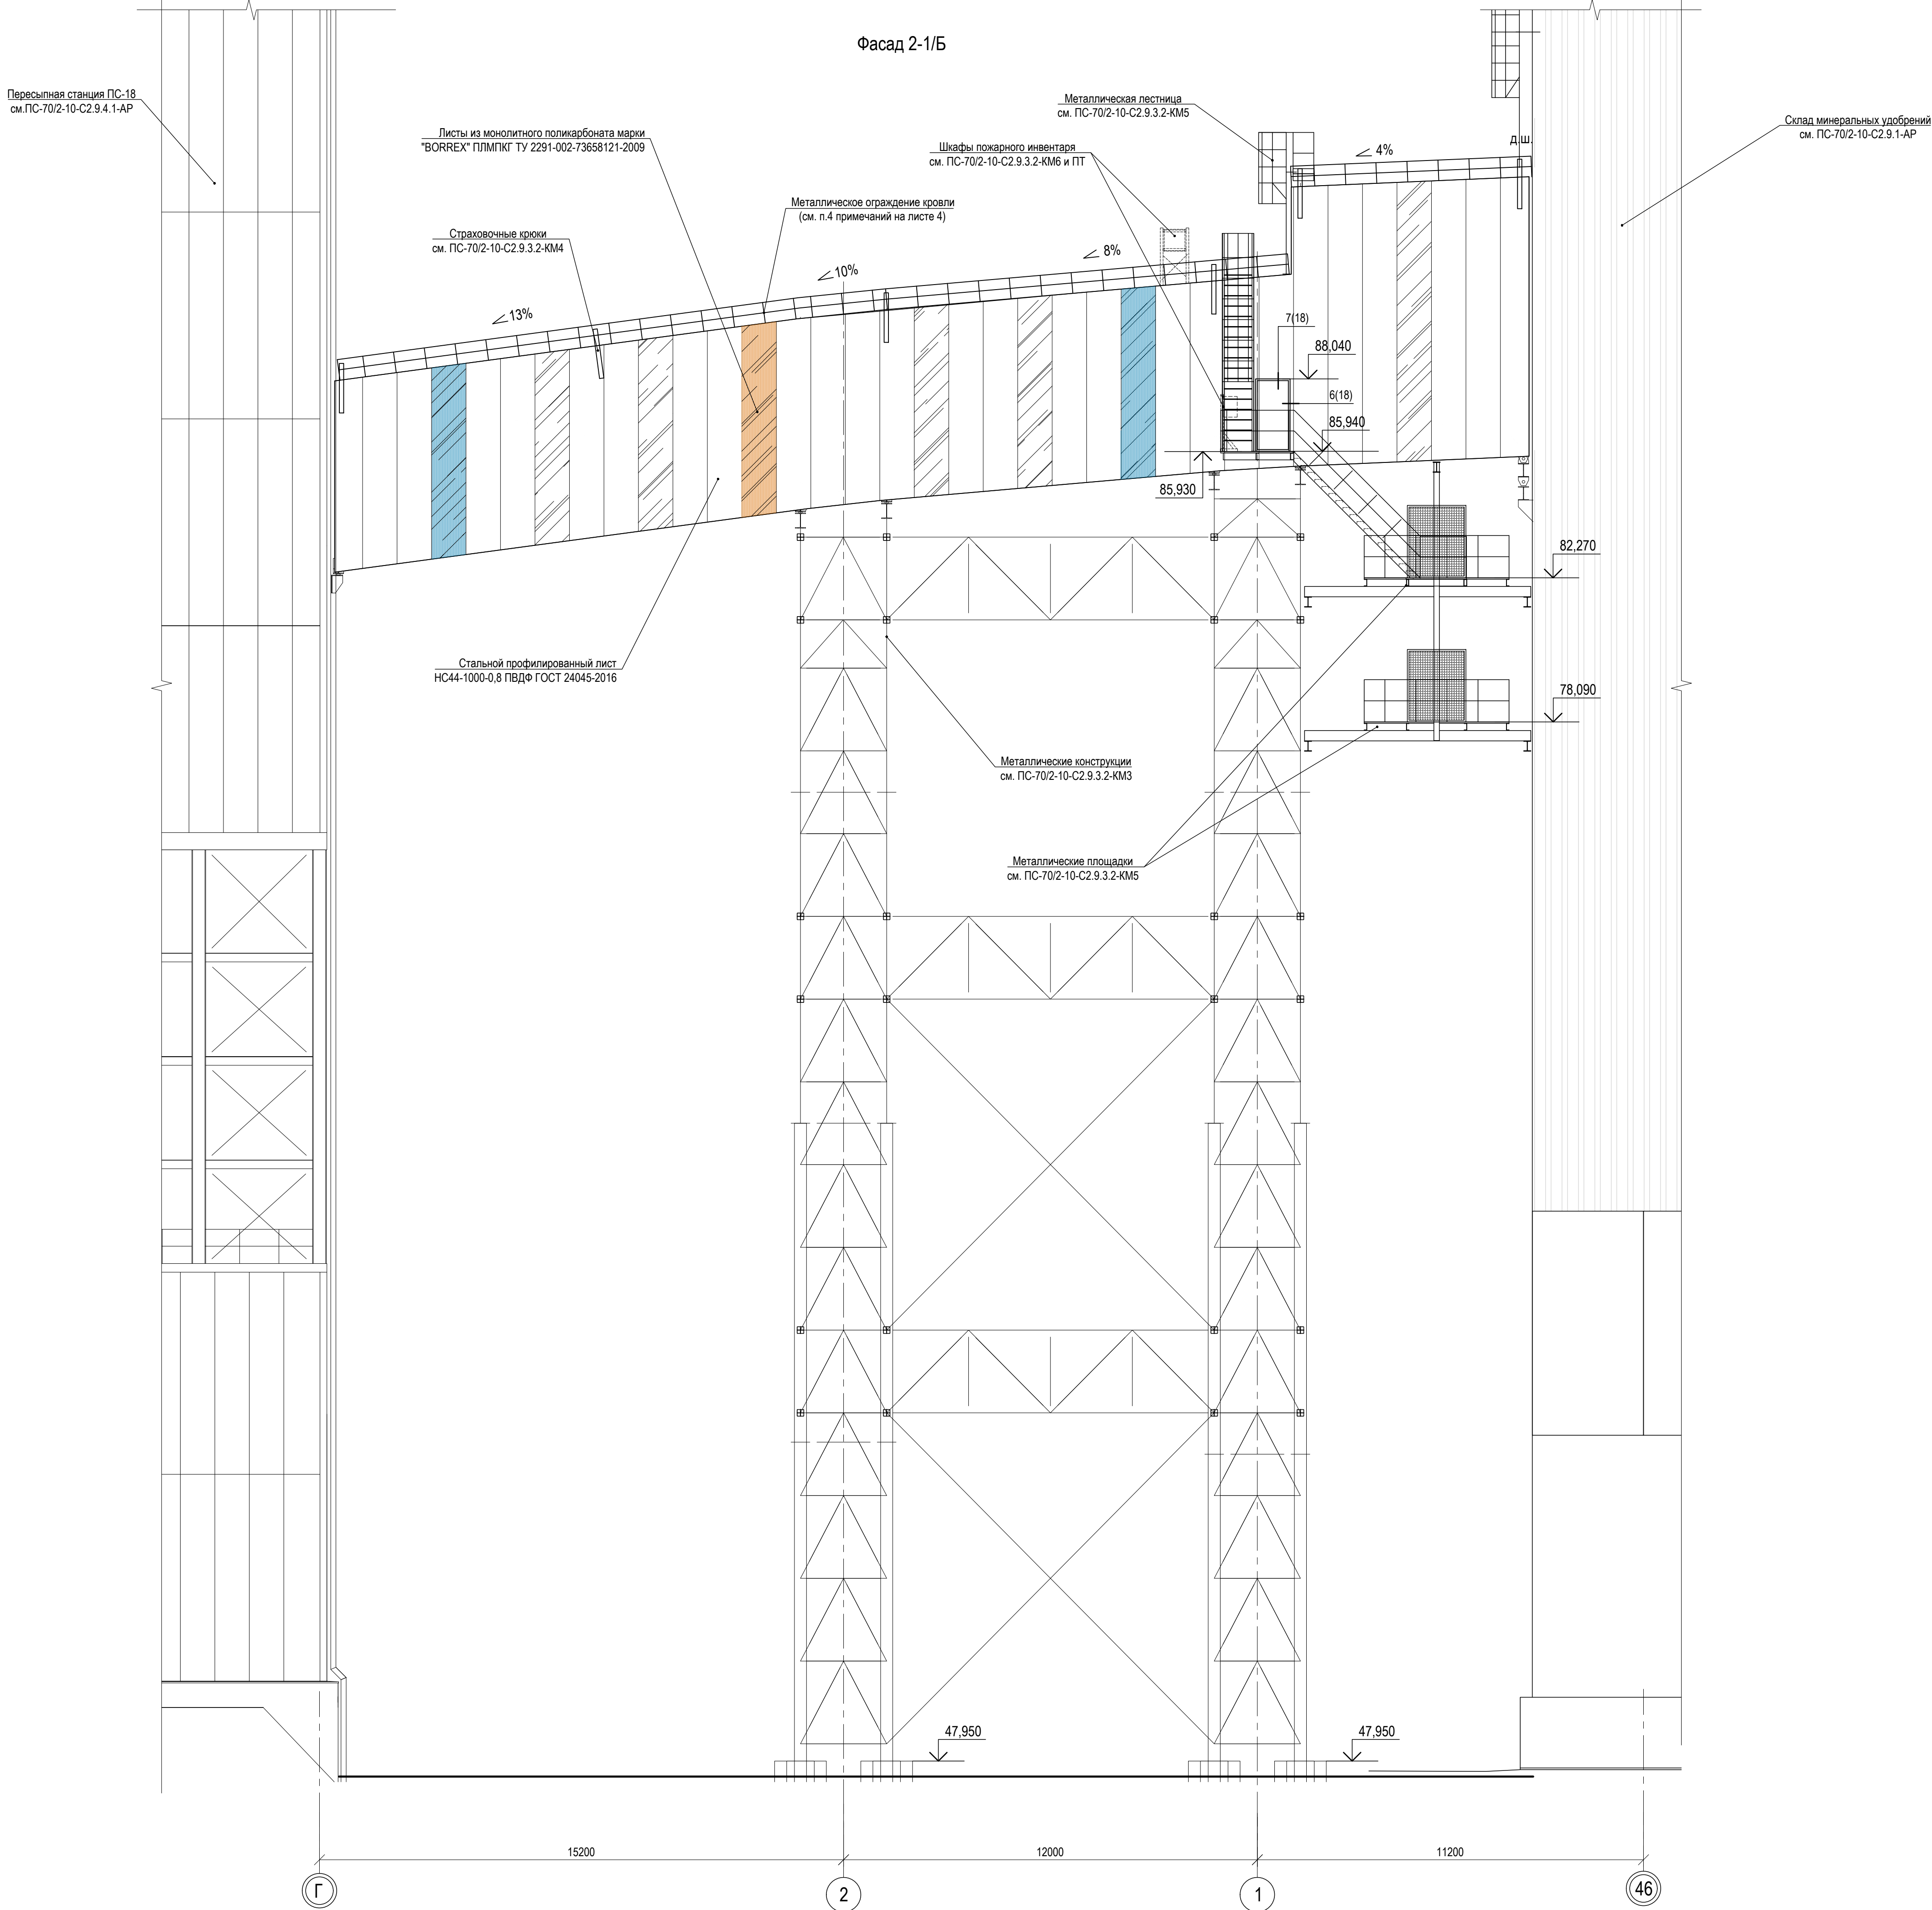


1. Общие указания см. лист 2.
2. Схемы раскладки стеновых ограждающих конструкций см. на листах 13-14.
3. Спецификацию элементов ограждающих конструкций см. на листе 11.

						ПС-70/2-10-С2.9.3.2-AP1				
						Таманский терминал навалочных грузов.				
						Этап 1				
1	-	Зам.	1617.20	<i>Подпись</i>	12.20	Конвейерная галерея минеральных удобрений ГК-15 (тит. С2.9.3.2)	Стадия	Лист	Листов	
Изм.	Копию	Лист	№рек	Подпись	Дата		Р	9		
Разработал		Божкова		<i>Подпись</i>	12.20					
Проверил		Силина		<i>Подпись</i>	12.20					
Нач. отдела		Зеленева		<i>Подпись</i>	12.20					
Н. контроль		Фоменкова		<i>Подпись</i>	12.20	Фасад 2-1/Б	ООО "Югтерминалпроект"			
ГИП		Пряников		<i>Подпись</i>	12.20					

Склад минеральных удобрений
см. ПС-70/2-10-С2.9.1-АР


Фасад 1-2/В

Пересыпная станция ПС-18
см. ПС-70/2-10-С2.9.4.1-АР

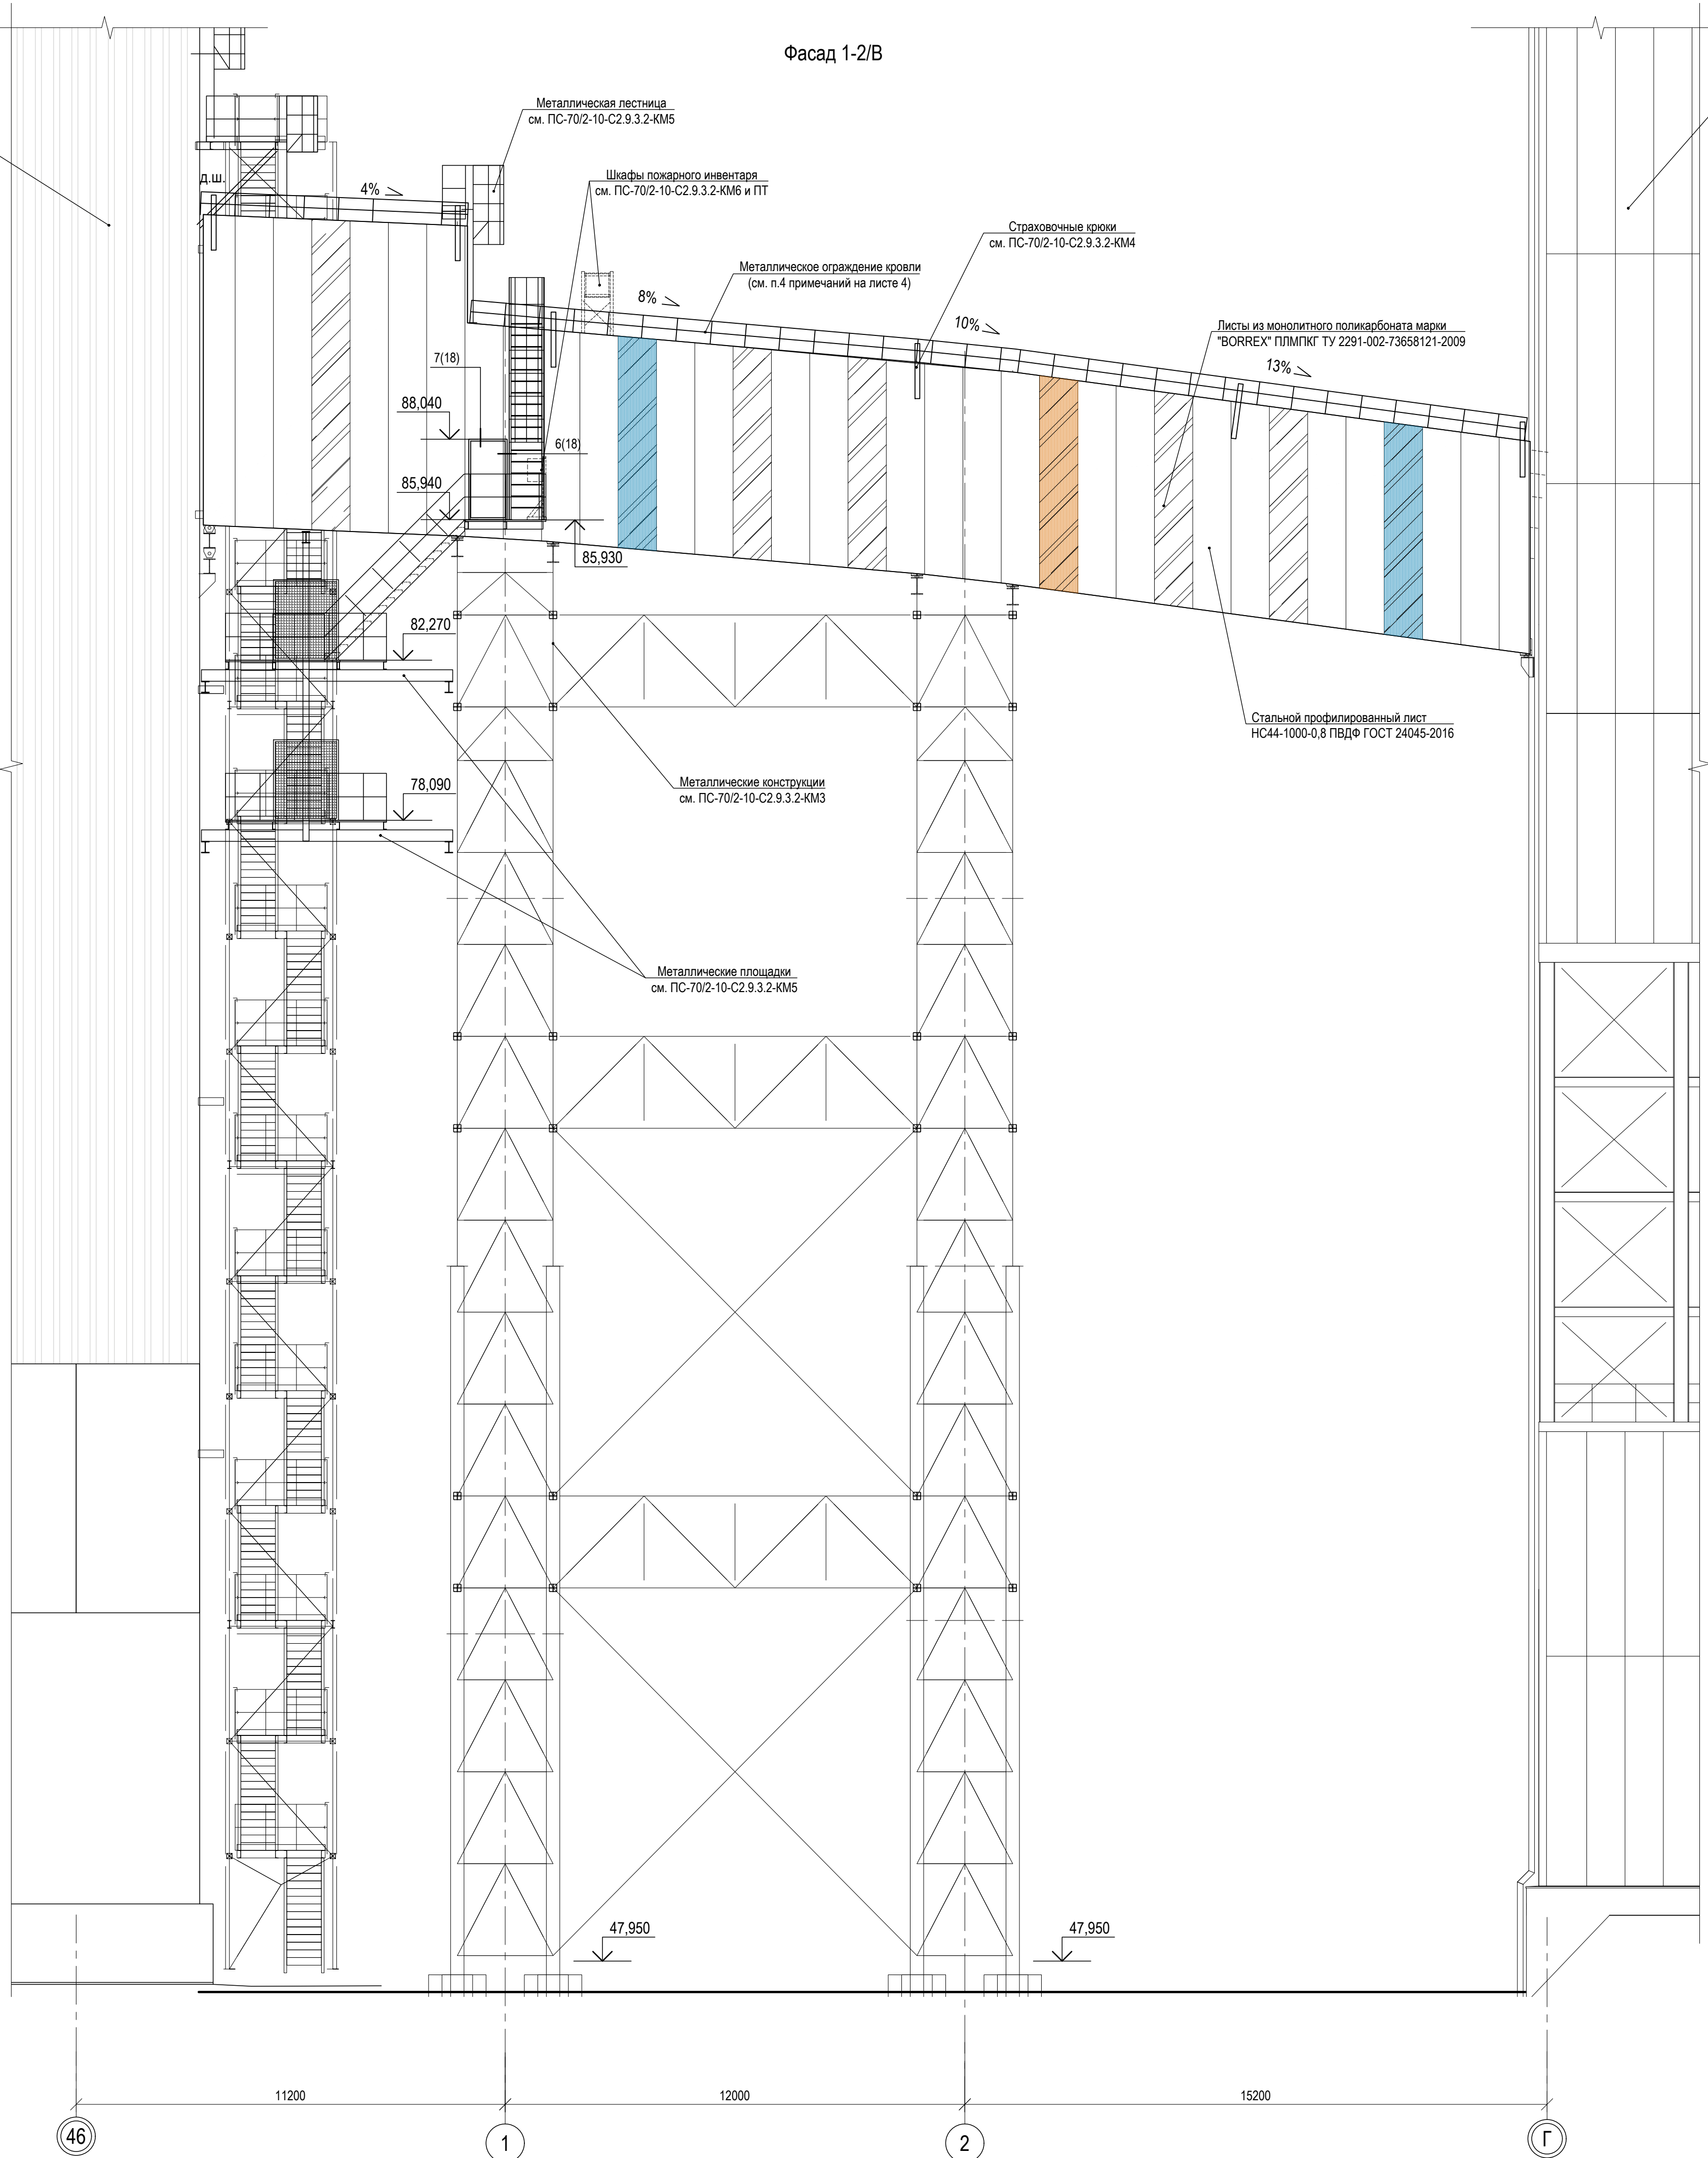

- Общие указания см. лист 2.
- Схемы раскладки стеновых ограждающих конструкций см. на листах 13-14.
- Спецификацию элементов ограждающих конструкций см. на листе 11.

						ПС-70/2-10-С2.9.3.2-АР1			
						Таманский терминал навалочных грузов.			
						Этап 1			
1	-	Зам.	1617.20	Подпись	Дата	Конвейерная галерея минеральных удобрений ГК-15 (тит. С2.9.3.2)			
Изм.	Кол.	Лист	Число	Подпись	Дата				
Разработал	Божкова		12.20		12.20				
Проверил	Силина		12.20		12.20				
Нач. отдела	Зеленева		12.20		12.20	Фасад 1-2/В			
Н. контроль	Фоменкова		12.20		12.20				
ГИП	Пряников		12.20		12.20	ООО "Югтерминалпроект"			

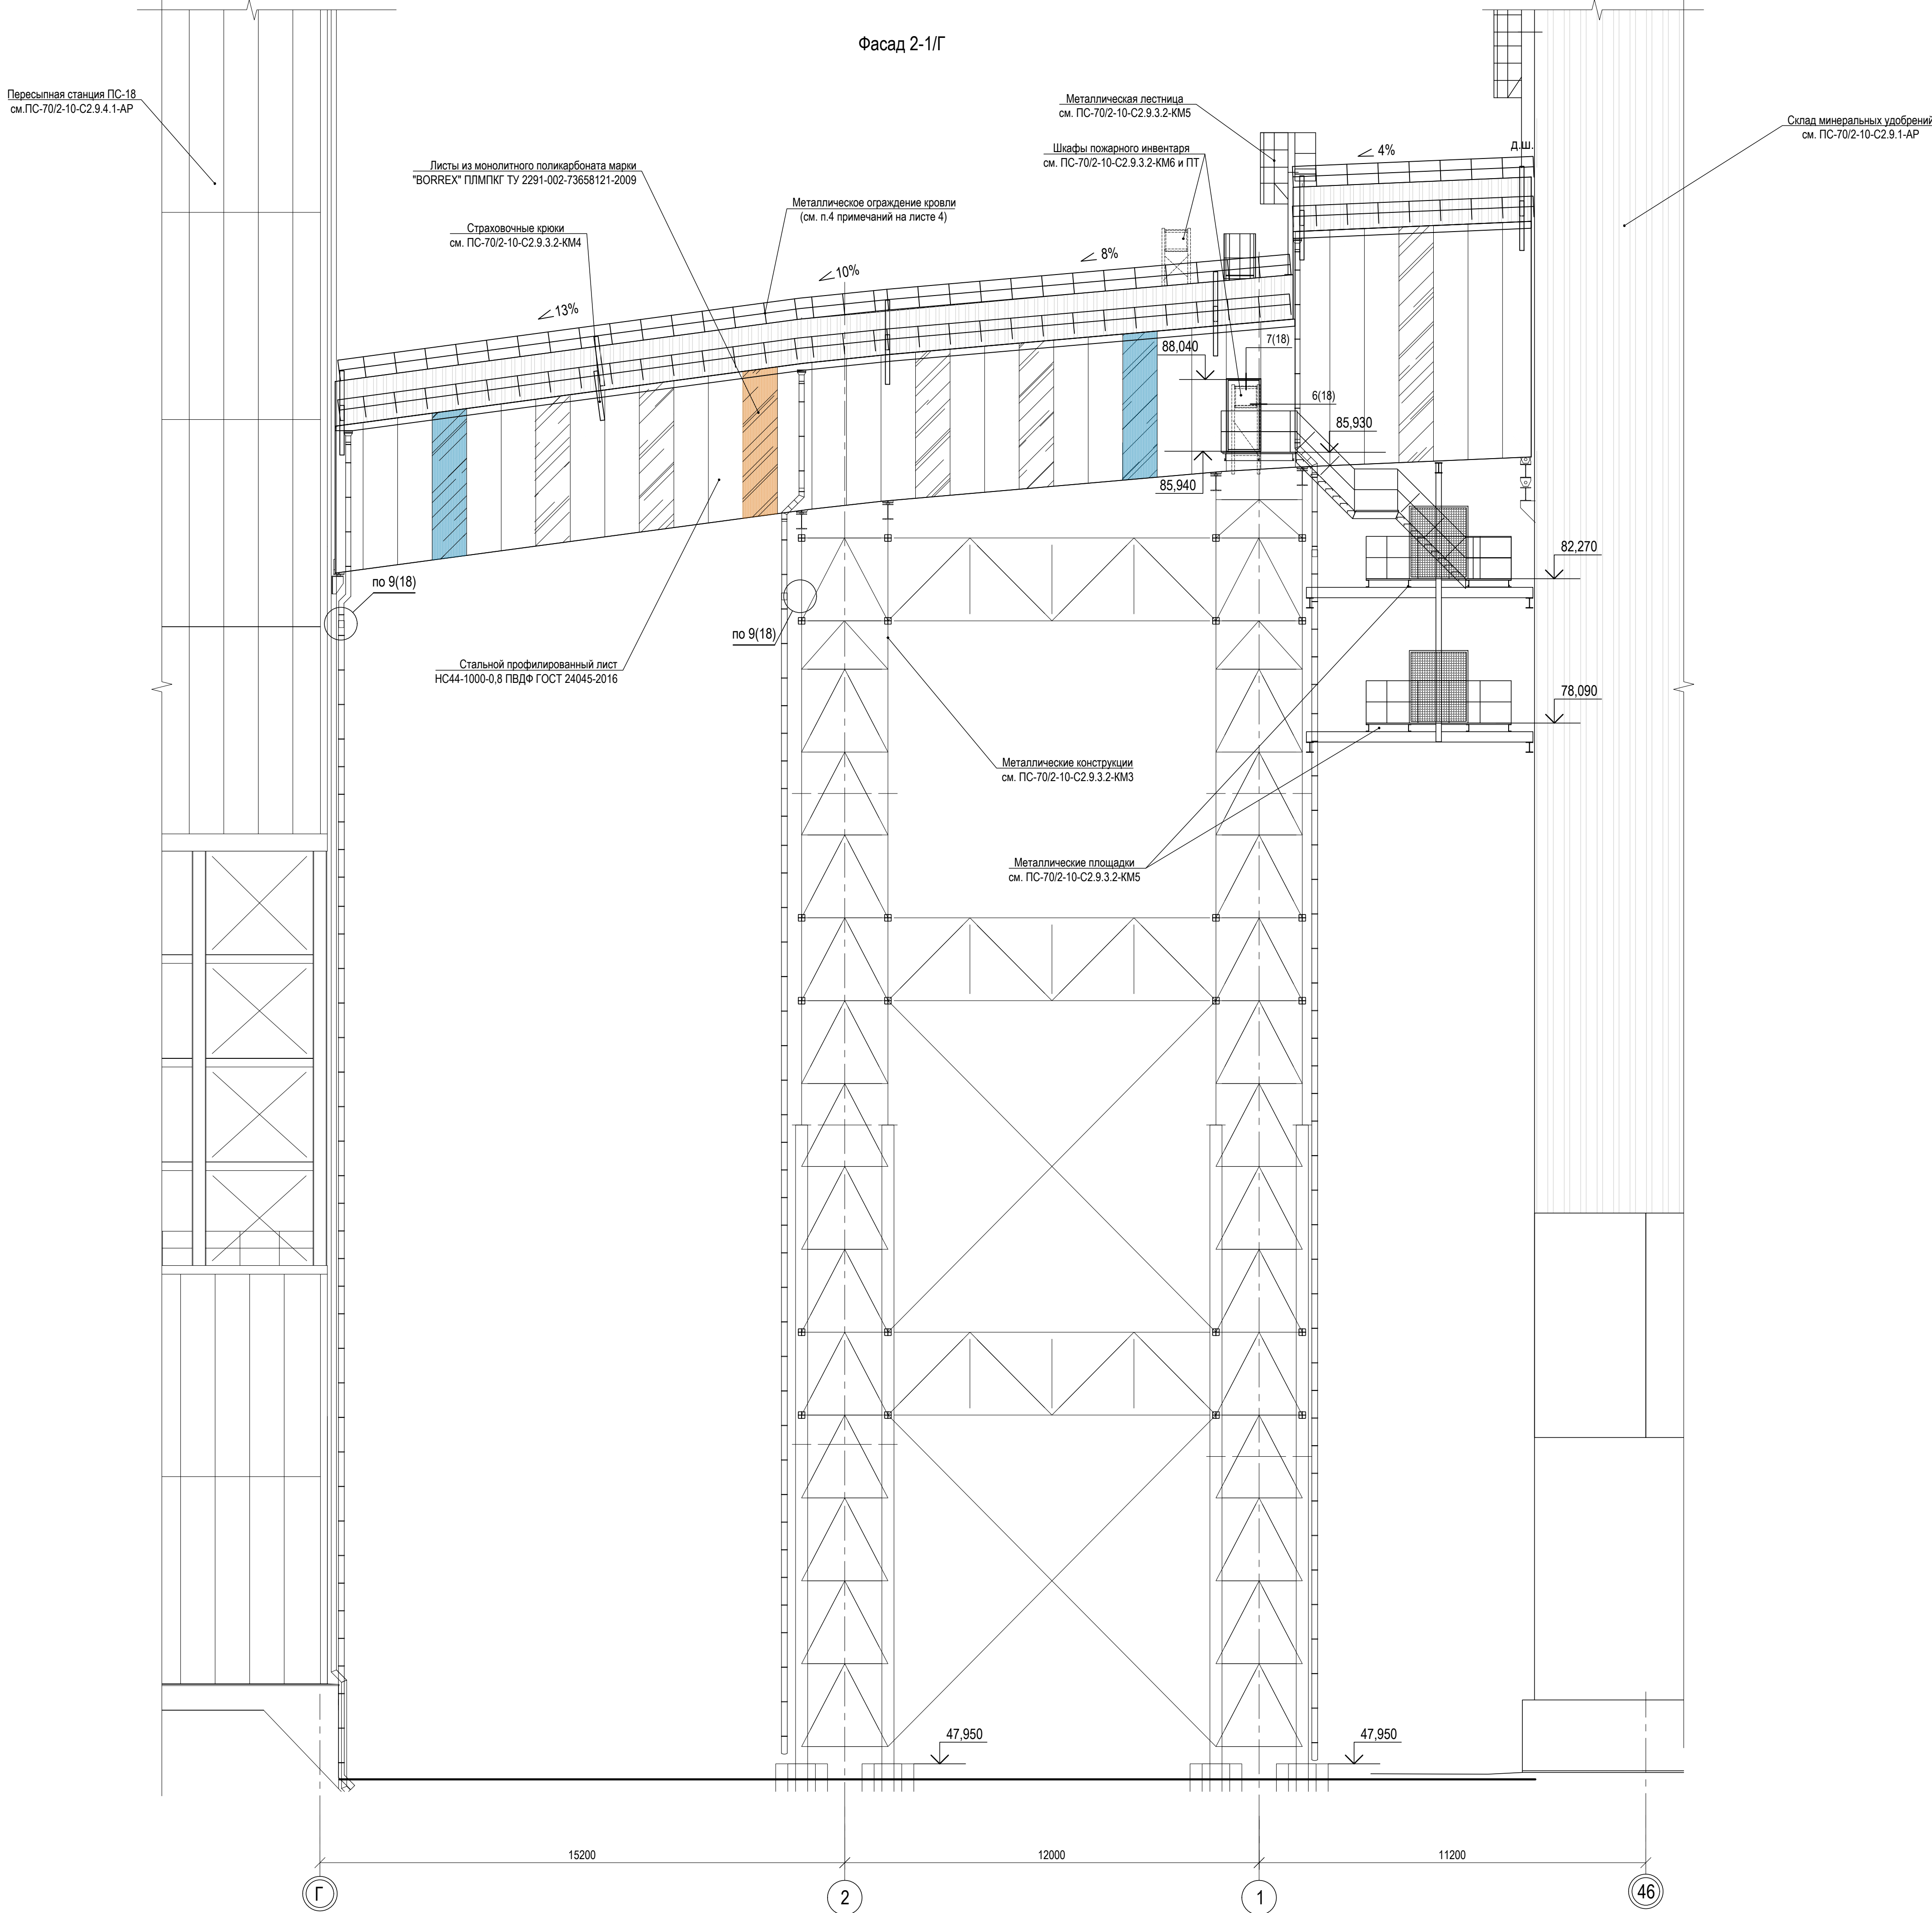

Спецификация элементов ограждающих конструкций*

Поз.	Обозначение	Наименование	Кол.	Масса, ед., кг	Примечание
		Фасады			
	ГОСТ 24045-2016	НС44-1000-0,8 ПВДФ RAL 5005 ПВДФ RAL 9003	586		м2
	ТУ 2291-002-73658121-2009	ПЛМПКГ 1,3-1050-ОРН-Пр-Глн	19.7		м2
	ТУ 2291-002-73658121-2009	ПЛМПКГ 1,3-1050-СИН-Пр-Глн	39.3		м2
	ТУ 2291-002-73658121-2009	ПЛМПКГ 1,3-1050-БЦ-Пр-Глн	104.2		м2
		Кровля			
	ГОСТ 24045-2016	Н75-750-0,8 ПВДФ RAL 7047 ПВДФ RAL 9003	358		м2

* В спецификации указаны площади фасадов и кровли без учета нахлестов профлиста и за вычетом проемов.

1. Общие указания см. лист 2.
2. Схемы раскладки стеновых ограждающих конструкций см. на листах 13-14.

						ПС-70/2-10-С2.9.3.2-AP1				
						Таманский терминал навалочных грузов.				
						Этап 1				
1	-	Зам.	16.17.20		12.20	Конвейерная галерея минеральных удобрений ГК-15 (тит. С2.9.3.2)	Стадия	Лист	Листов	
Изм.	Колуч	Лист	Нижж	Подпись	Дата		Р	11		
Разработал	Божкова				12.20					
Проверил	Силина				12.20					
Нач. отдела	Зеленева				12.20					
Н. контроль	Фоменкова				12.20	Фасад 2-1/Г	ООО "Югтерминалпроект"			
ГИП	Пряников				12.20					

Цветовое решение фасадов

Фасад 1-2/А

Фасад 2-1/Б

Фасад 1-2/В

Фасад 2-1/Г

Цветовое решение фасадов

№ п/п	Наименование и номер эталона цвета или образец колера	Наименование материала или детали отделки	Образец
2	Синий, RAL 5005	Профилированный лист НС44-1000-0,8 ПВДФ ГОСТ 24045-2016	
4	Серебристый, RAL 9006	Металлические двери, наружные лестницы, ограждения, площадки, фасонные элементы	
5	Серый, RAL 7047	Профилированный лист покрытия Н75-750-0,8 ПВДФ ГОСТ 24045-2016, металлические конструкции, водосточные системы	
6	Прозрачный оранжевый	Листы из монолитного поликарбоната марки "BORREX" ПЛМПКГ 1,3-1050-ОРН-Пр-Глн ТУ 2291-002-73658121-2009	
7	Прозрачный синий	Листы из монолитного поликарбоната марки "BORREX" ПЛМПКГ 1,3-1050-СИН-Пр-Глн ТУ 2291-002-73658121-2009	
8	Прозрачный	Листы из монолитного поликарбоната марки "BORREX" ПЛМПКГ 1,3-1050-БЦ-Пр-Глн ТУ 2291-002-73658121-2009	

1. Общие указания см. лист 2.
2. Схемы раскладки стеновых ограждающих конструкций см. на листах 13-14.

						ПС-70/2-10-С2.9.3.2-АР1			
						Таманский терминал навалочных грузов. Этап 1			
1	-	Зам.	1617-20		12.20	Конвейерная галерея минеральных удобрений ГК-15 (тит. С2.9.3.2)	Стадия	Лист	Листов
Изм.	Колуч	Лист	Надок	Подпись	Дата		Р	12	
Разработал	Божкова				12.20				
Проверил	Силина				12.20				
Нач. отдела	Зеленева				12.20	Цветовое решение фасадов	ООО "Югтерминалпроект"		
Н. контроль	Фоменкова				12.20				
ГИП	Пряников				12.20				

Инв. N подл.	Подпись и дата	Взам. инв. N
72931220327		

Схема раскладки стеновых ограждающих конструкций в осях 1-2/А

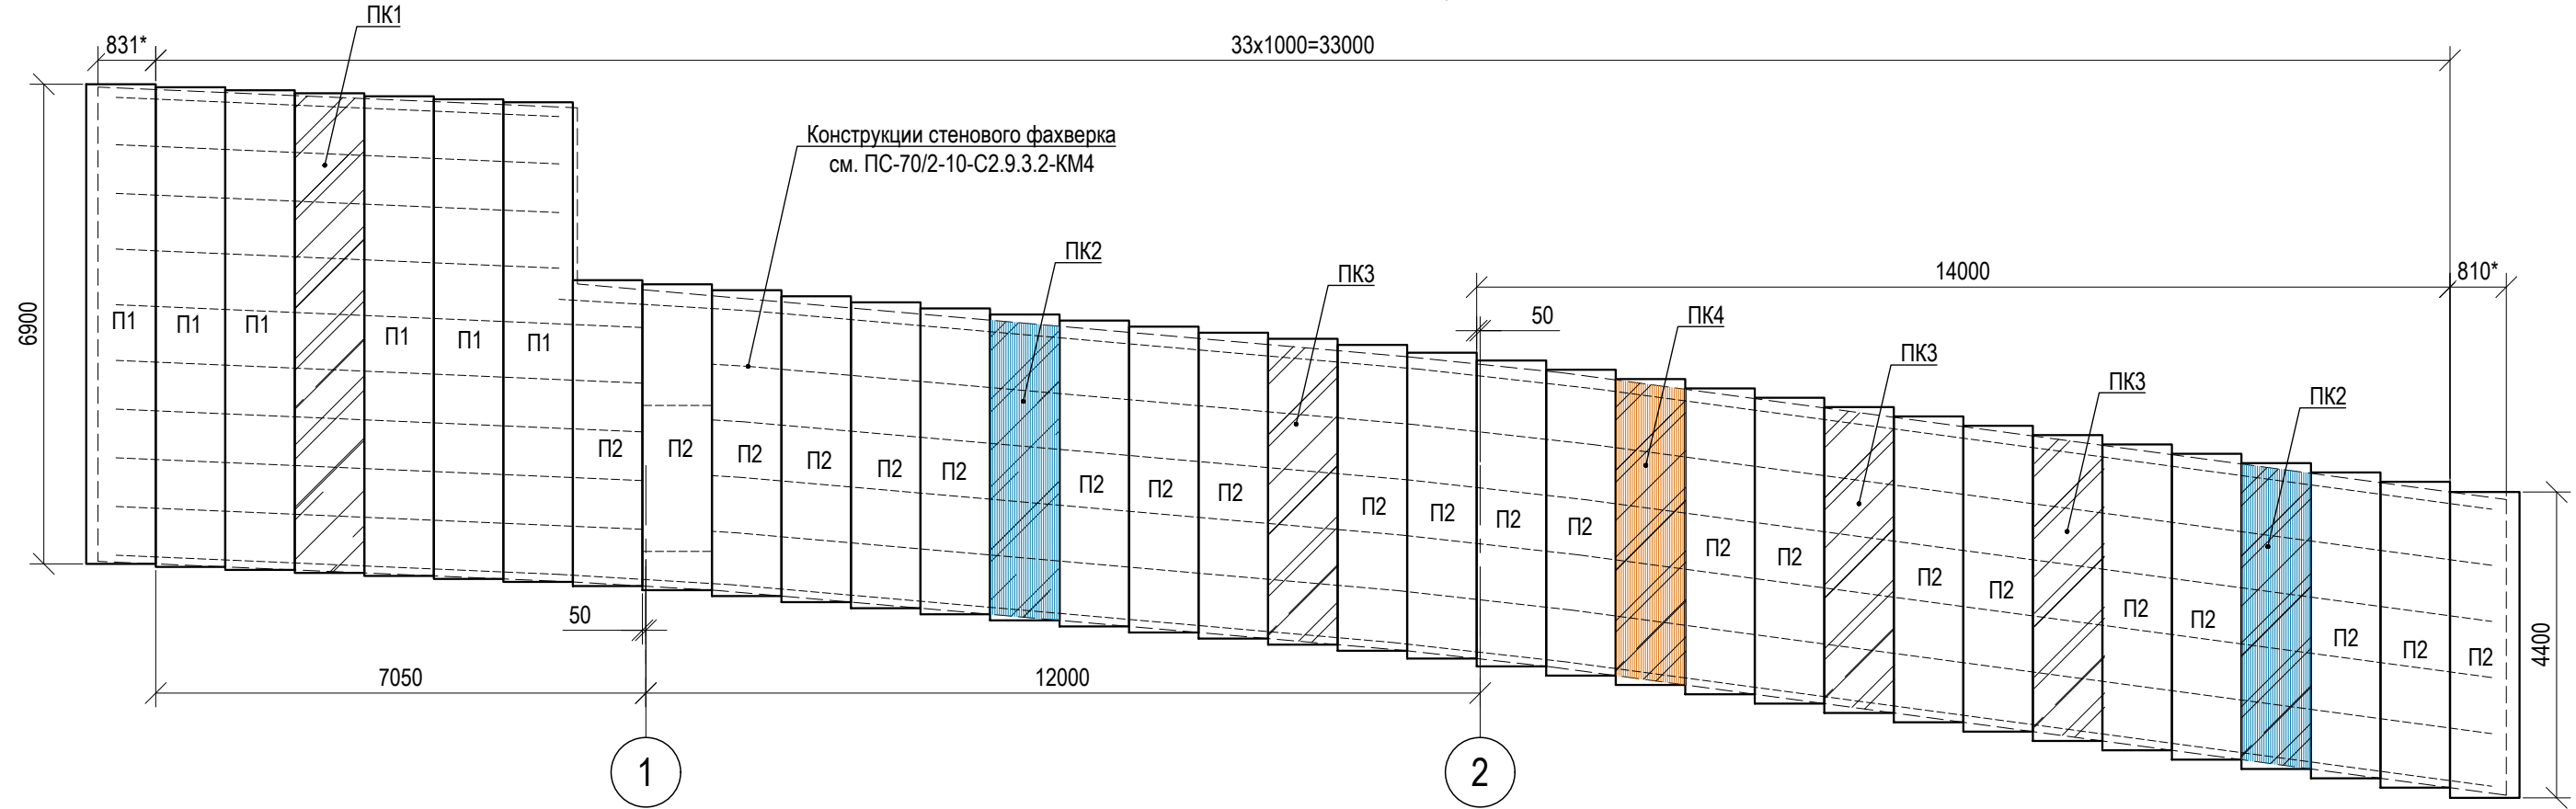


Схема раскладки стеновых ограждающих конструкций в осях 1-2/В


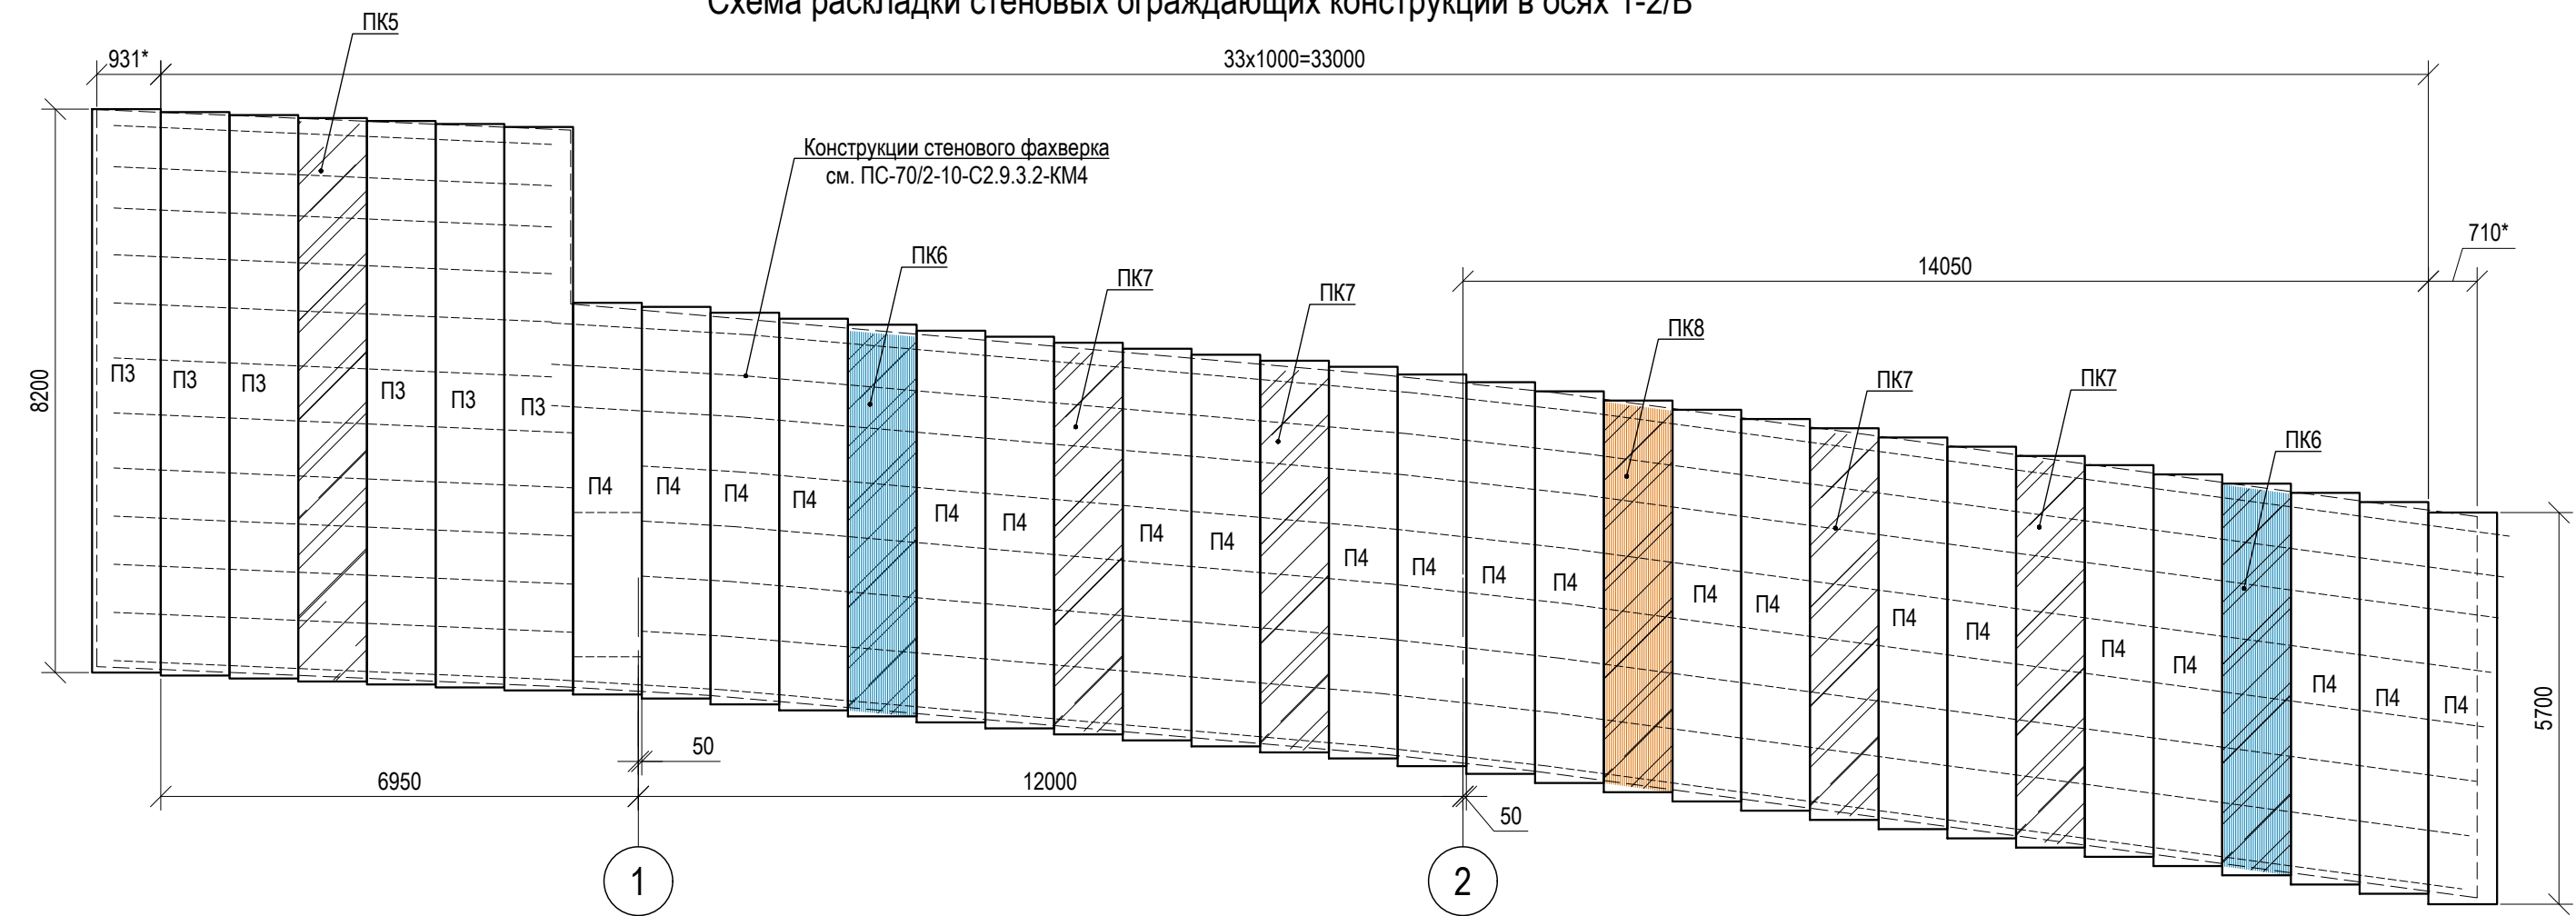


Схема раскладки стеновых ограждающих конструкций в осях А-Г/1

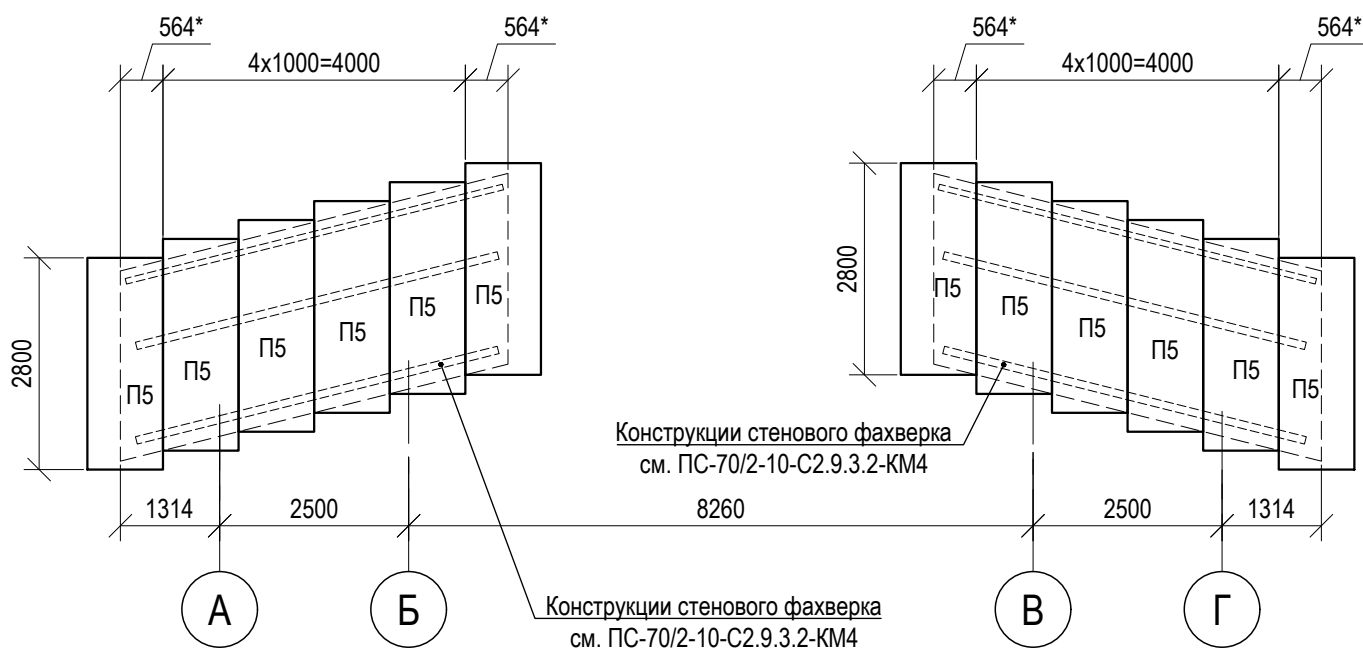

- Общие указания см. лист 2.
- Профлист обрезать по месту в соответствии с углом наклона галереи.
- * Привязки и размеры крайних листов уточнить по месту в соответствии с фактическим расположением фахверка.
- Данный лист см. совместно с листом 14.

						ПС-70/2-10-С2.9.3.2-АР1					
						Таманский терминал навалочных грузов. Этап 1					
1	-	Зам.	1617-20	Подпись	Дата	Конвейерная галерея минеральных удобрений ГК-15 (тит. С2.9.3.2)			Стадия	Лист	Листов
Изм.	Колуч	Лист	Недок	Подпись	Дата				Р	13	
Разработал	Божкова			Подпись	Дата						
Проверил	Силина			Подпись	Дата	Схема раскладки стеновых ограждающих конструкций в осях 1-2/А; 1-2/В; А-Г/1			ООО "Югтерминалпроект"		
Нач. отдела	Зеленева			Подпись	Дата						
Н. контроль	Фоменкова			Подпись	Дата						
ГИП	Пряников			Подпись	Дата						

Схема раскладки стеновых ограждающих конструкций в осях 2-1/Г


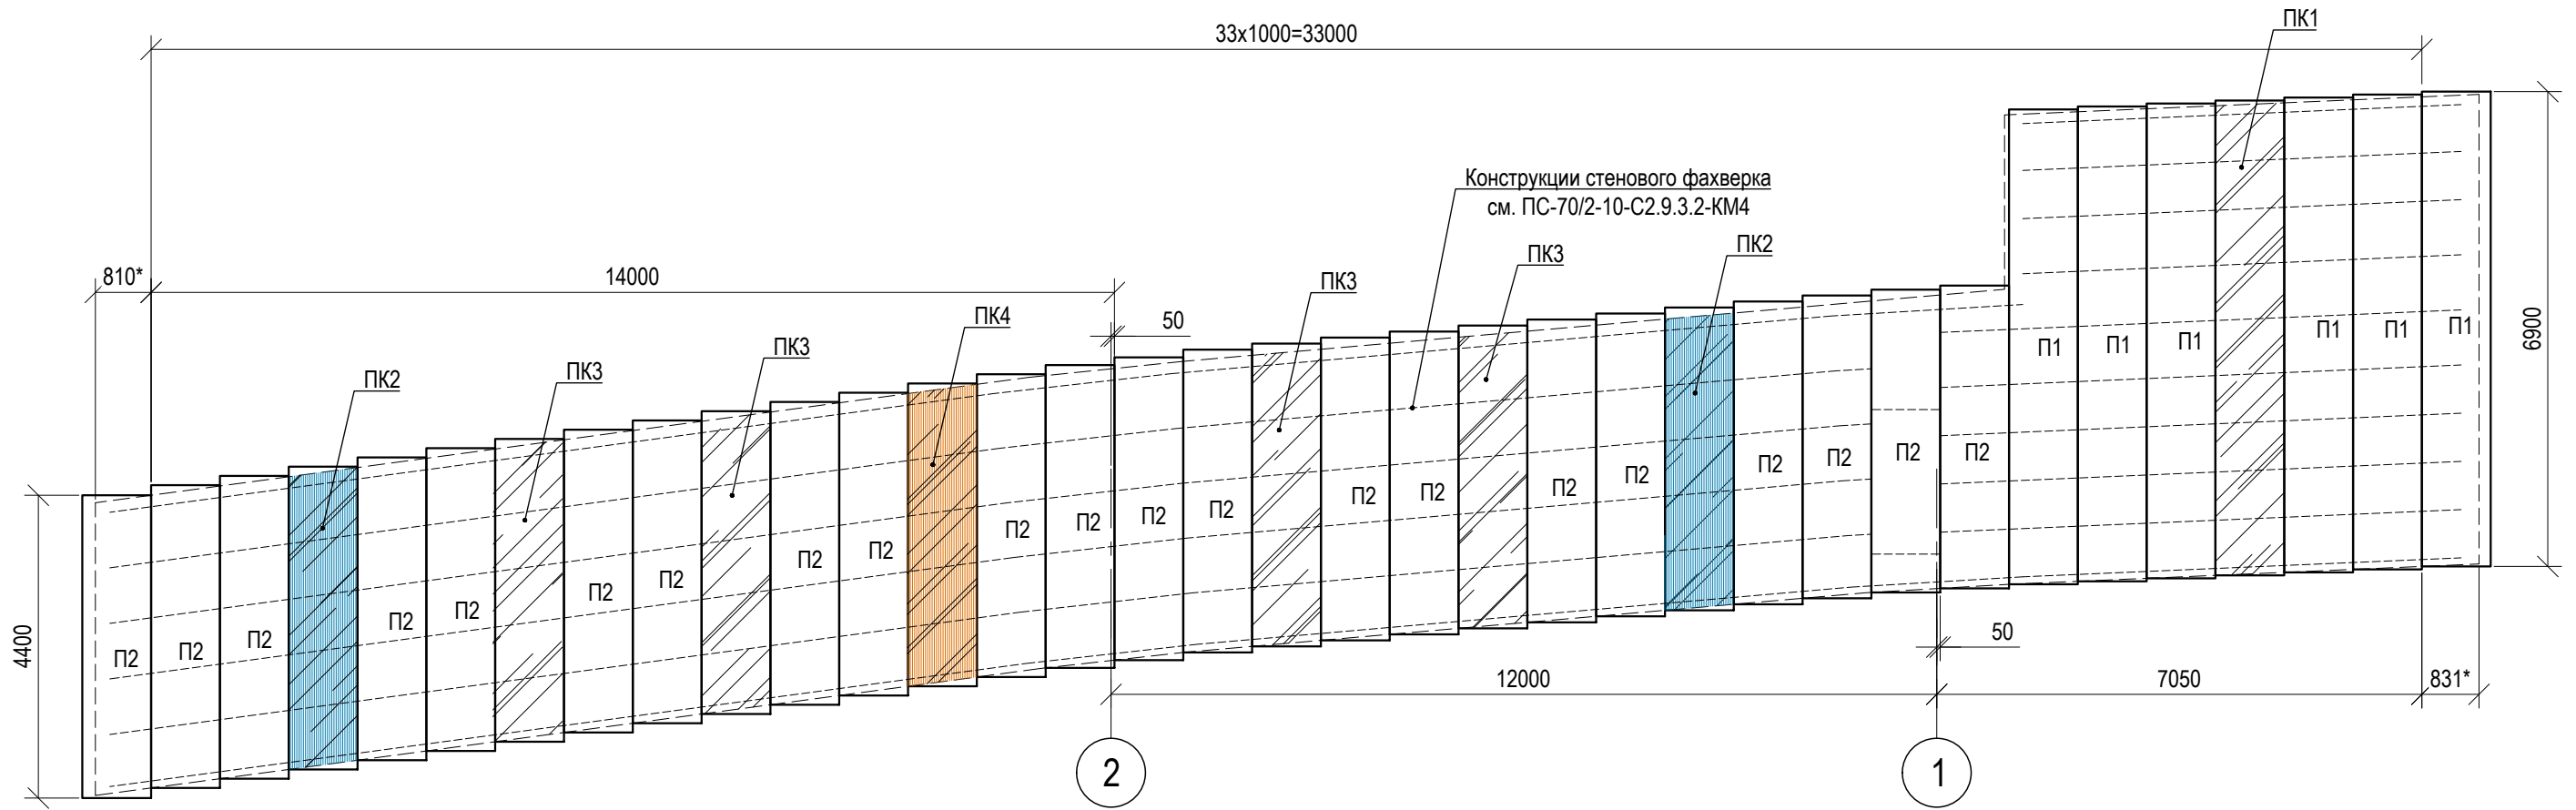


Схема раскладки стеновых ограждающих конструкций в осях 2-1/Б

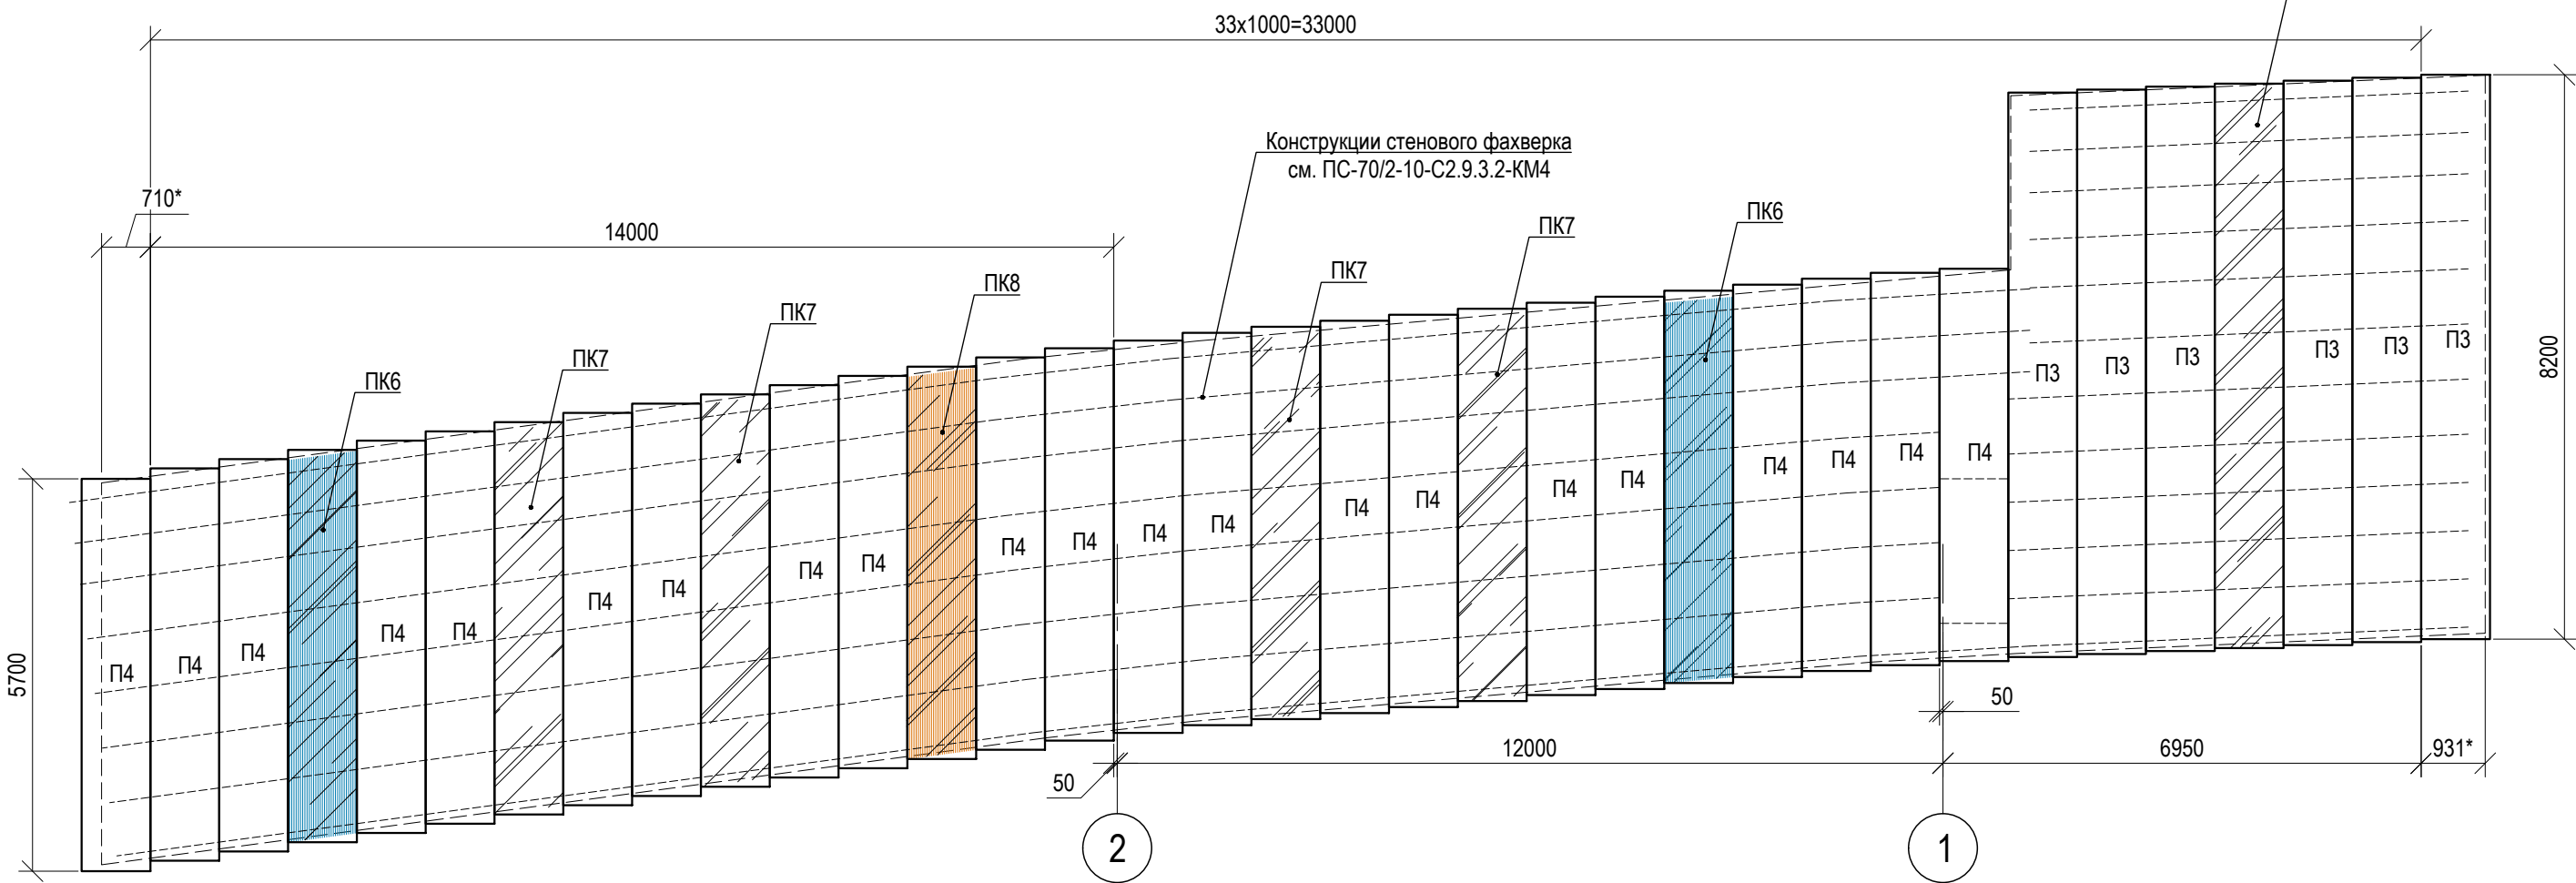

Спецификация к схемам раскладки стеновых ограждающих конструкций

Поз.	Обозначение	Наименование	Кол., шт.	Масса, ед., кг	Примечание
П1	ГОСТ 24045-2016	НС44-1000-0,8 ПВДФ, L=6900, RAL 5005/RAL 9003	12		
П2	ГОСТ 24045-2016	НС44-1000-0,8 ПВДФ, L=4400, RAL 5005/RAL 9003	43		
П3	ГОСТ 24045-2016	НС44-1000-0,8 ПВДФ, L=8200, RAL 5005/RAL 9003	12		
П4	ГОСТ 24045-2016	НС44-1000-0,8 ПВДФ, L=5700, RAL 5005/RAL 9003	42		
П5	ГОСТ 24045-2016	НС44-1000-0,8 ПВДФ, L=2800, RAL 5005/RAL 9003	12		
ПК1	ТУ 2291-002-73658121-2009	ПЛМПКГ 1,3-6900-1050-БЦ-Пр-Глн	2		
ПК2	ТУ 2291-002-73658121-2009	ПЛМПКГ 1,3-4400-1050-СИН-Пр-Глн	4		
ПК3	ТУ 2291-002-73658121-2009	ПЛМПКГ 1,3-4400-1050-БЦ-Пр-Глн	7		
ПК4	ТУ 2291-002-73658121-2009	ПЛМПКГ 1,3-4400-1050-ОРН-Пр-Глн	2		
ПК5	ТУ 2291-002-73658121-2009	ПЛМПКГ 1,3-8200-1050-БЦ-Пр-Глн	2		
ПК6	ТУ 2291-002-73658121-2009	ПЛМПКГ 1,3-5700-1050-СИН-Пр-Глн	4		
ПК7	ТУ 2291-002-73658121-2009	ПЛМПКГ 1,3-5700-1050-БЦ-Пр-Глн	8		
ПК8	ТУ 2291-002-73658121-2009	ПЛМПКГ 1,3-5700-1050-ОРН-Пр-Глн	2		

ИТОГО :


НС44-1000-0,8 ПВДФ RAL 5005/RAL9003 ГОСТ 24045-2016	643.4 м²	
"BORREX"ПЛМПКГ 1,3-1050-ОРН-Пр-Глн ТУ 2291-002-73658121-2009	21.2 м²	
"BORREX"ПЛМПКГ 1,3-1050-СИН-Пр-Глн ТУ 2291-002-73658121-2009	42.5 м²	
"BORREX" ПЛМПКГ 1,3-1050-БЦ-Пр-Глн ТУ 2291-002-73658121-2009	112 м²	

- Поэлементный расчет стеновых ограждающих конструкций дан для информации сметному отделу

1. Общие указания см. лист 2.
2. Профлист обрезать по месту в соответствии с углом наклона галереи.
3. * Привязки и размеры крайних листов уточнить по месту в соответствии с фактическим расположением фахверка.
- 4.. Данный лист см. совместно с листом 13.

						ПС-70/2-10-С2.9.3.2-АР1					
						Таманский терминал навалочных грузов. Этап 1					
1	-	Зам.	1617-20		12.20	Конвейерная галерея минеральных удобрений ГК-15 (тит. С2.9.3.2)			Стадия	Лист	Листов
Изм.	Коплуч	Лист	Недок	Подпись	Дата				Р	14	
Разработал	Божкова				12.20						
Проверил	Силина				12.20						
Нач. отдела	Зеленева				12.20	Схема раскладки стеновых ограждающих конструкций в осях 2-1/Б; 2-1/Г			ООО "Югтерминалпроект"		
Н. контроль	Фоменкова				12.20						
ГИП	Пряников				12.20						

Схема раскладки кровельных ограждающих конструкций

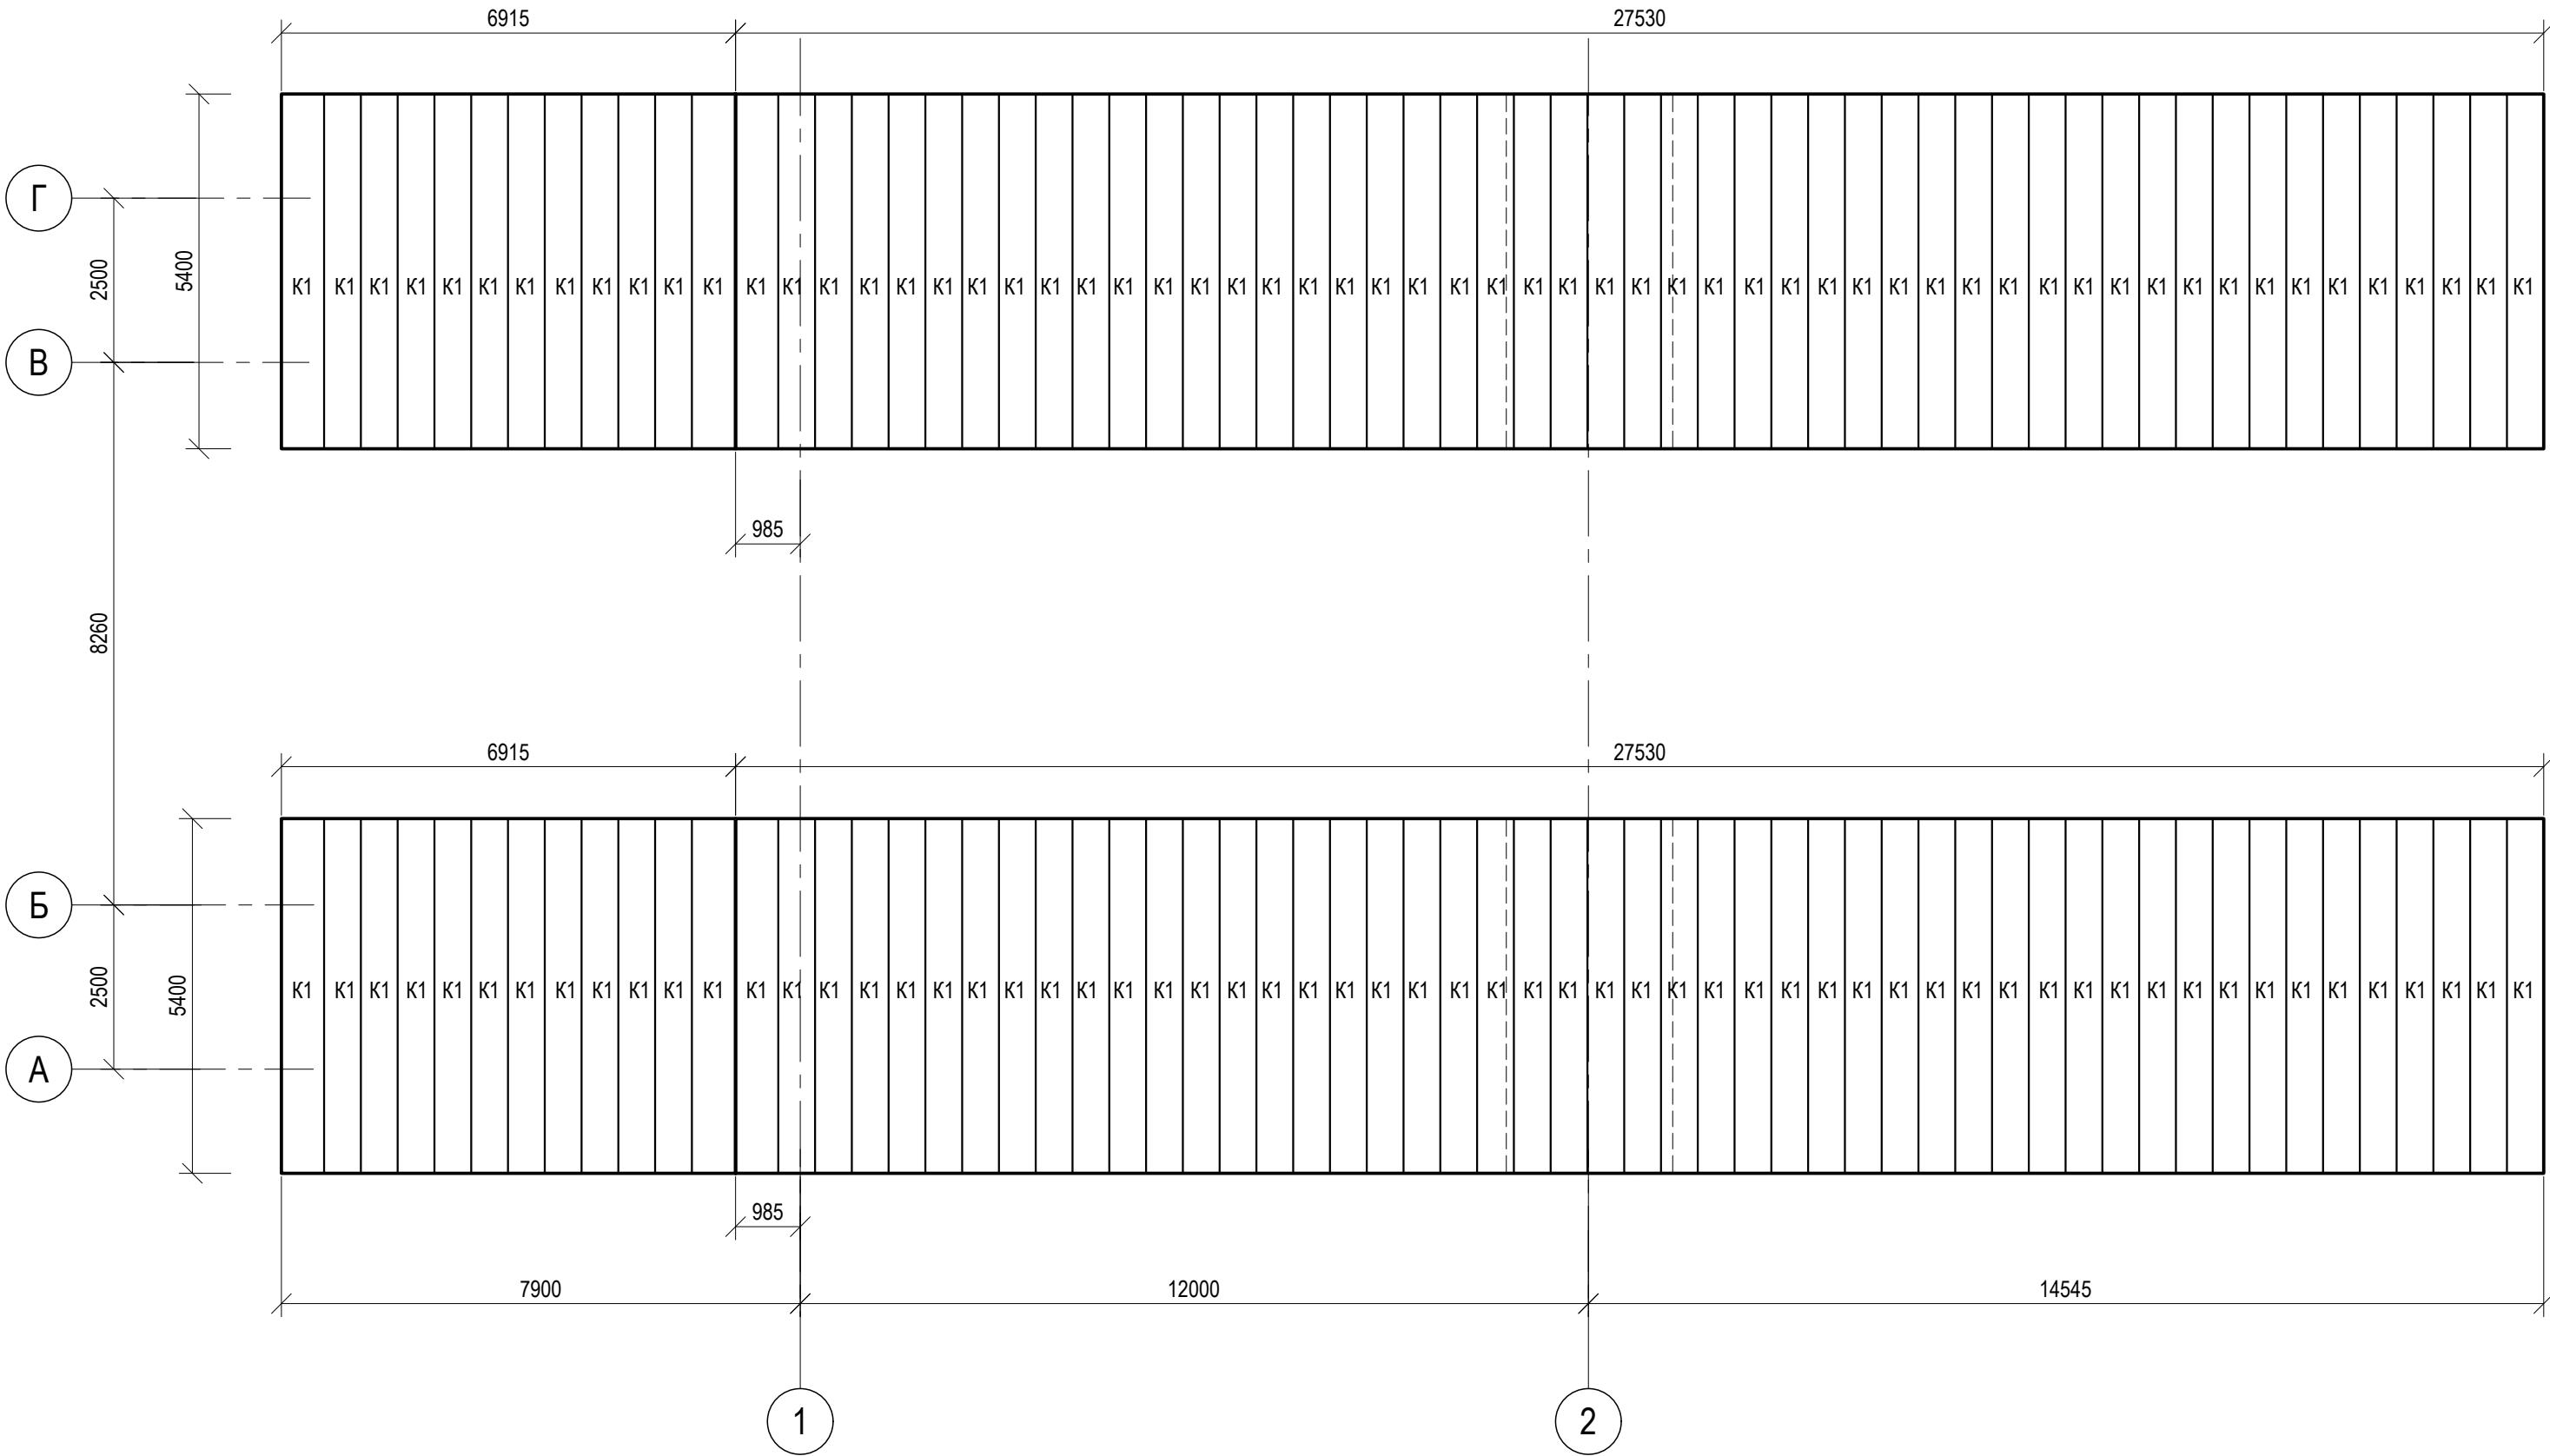


Спецификация к схемам раскладки кровельных ограждающих конструкций

Поз.	Обозначение	Наименование	Кол., шт.	Масса, ед., кг	Примечание
К1	ГОСТ 24045-2016	Н75-750-0,8 ПВДФ, L=5400, RAL7047/RAL9003	122		
ИТОГО :					
Н75-750-0,8 ПВДФ RAL 7047/ RAL 9003 ГОСТ 24045-2016				494.1 м²	





- Поэлементный расчет стеновых ограждающих конструкций дан для информации сметному отделу

Схема стыковки листов кровельного профлиста поперек ската

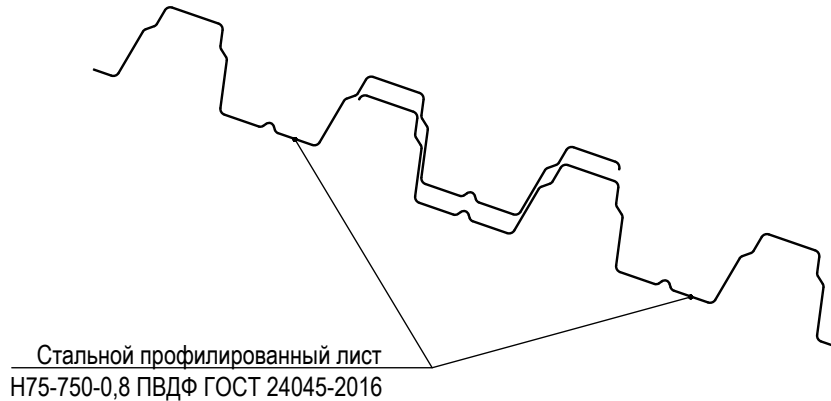







1. Общие указания см. лист 2.
2. Значение нахлеста профиля поперек ската должно быть на один гофр.
3. * Привязки и размеры крайних листов уточнить по месту в соответствии с фактическим расположением фахверка.

						ПС-70/2-10-С2.9.3.2-АР1					
						Таманский терминал навалочных грузов. Этап 1					
1	-	Зам.	1617-20		12.20	Конвейерная галерея минеральных удобрений ГК-15 (тит. С2.9.3.2)			Стадия	Лист	Листов
Изм.	Копуч	Лист	№док	Подпись	Дата				Р	15	
Разработал	Божкова			12.20	Схема раскладки кровельных ограждающих конструкций				ООО "Югтерминалпроект"		
Проверил	Силина			12.20							
Нач. отдела	Зеленеева			12.20							
Н. контроль	Фоменкова			12.20							
ГИП	Пряников			12.20							

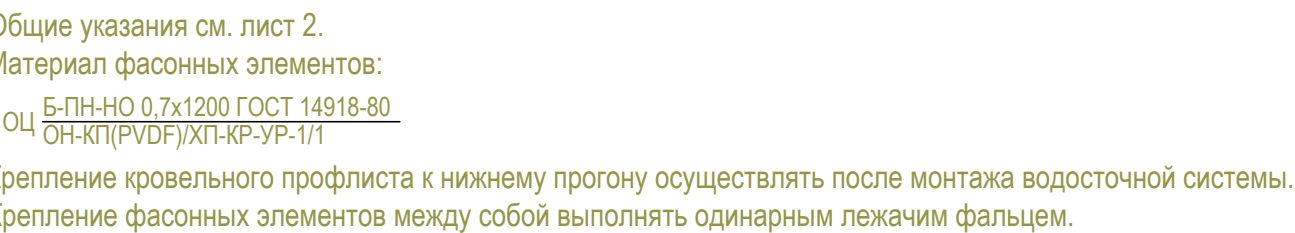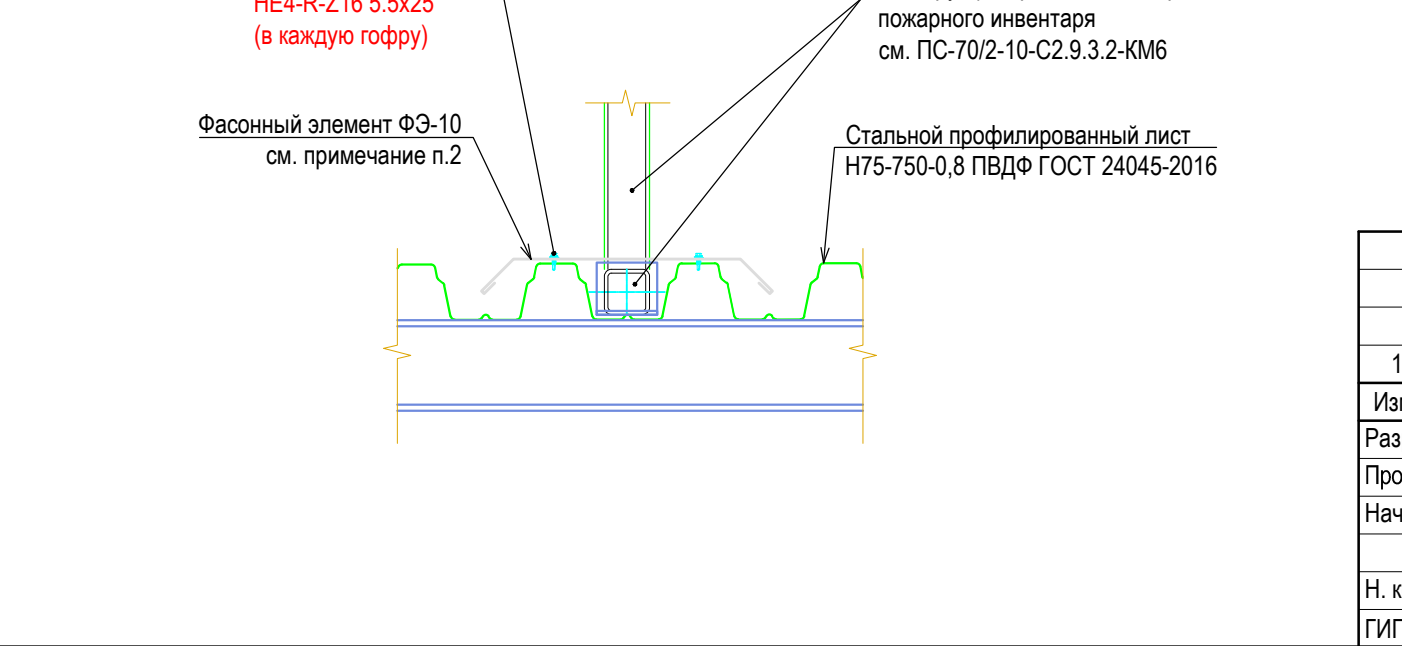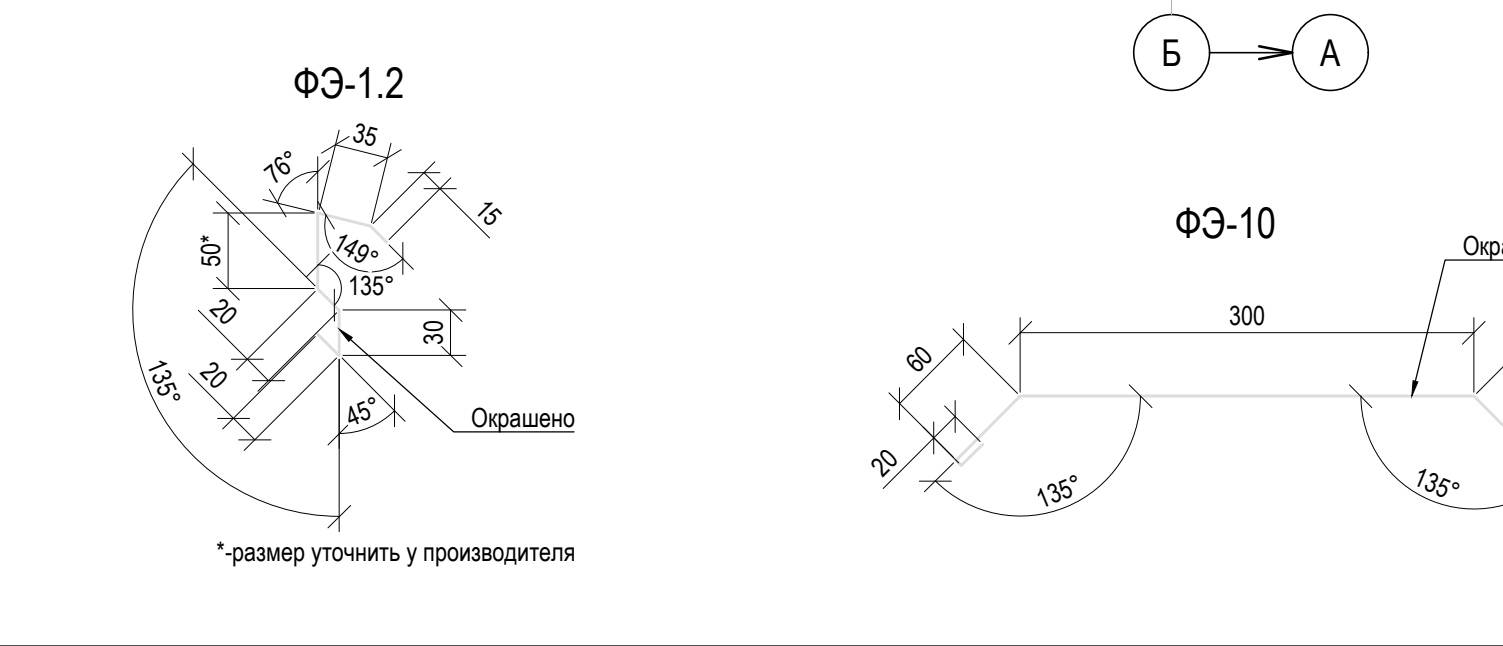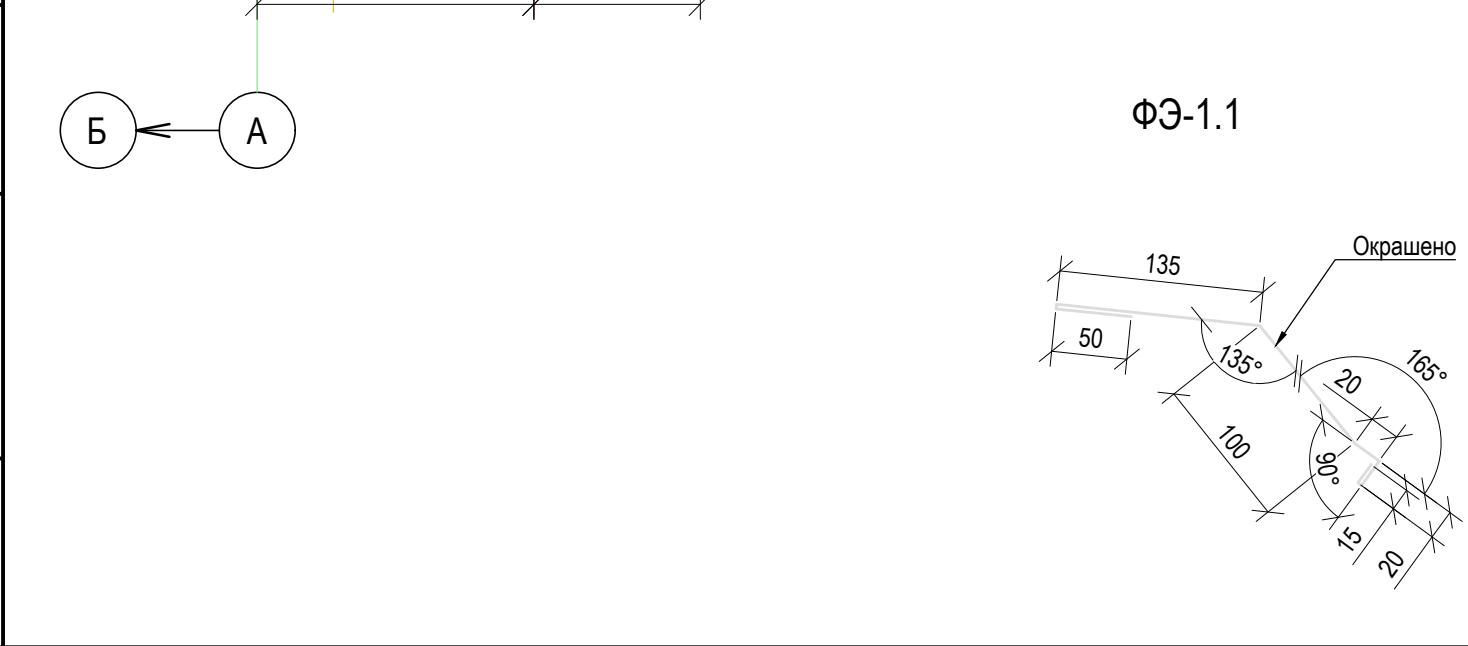

							ПС-70/2-10-С2.9.3.2-АП1			
1	-	Зам.	16/17-20			12.20	Таманский терминал навалочных грузов.			
Изм.	Копия	Лист	Надрж	Подпись		Дата	Этап 1			
Разработан		Тимофеев				05.26	Конвейерная галерея минеральных удобрений ГК-15 (тит. С2.9.3.2)	Стадия	Лист	Листов
Проверил								Р	16	
Нач. отдела										
Н. контроль							Узлы 1-2, 10	ООО "Гранд Вэй"		
ГИП										















Инв. N подл.	
Подпись и дата	
Взам. инв. N	

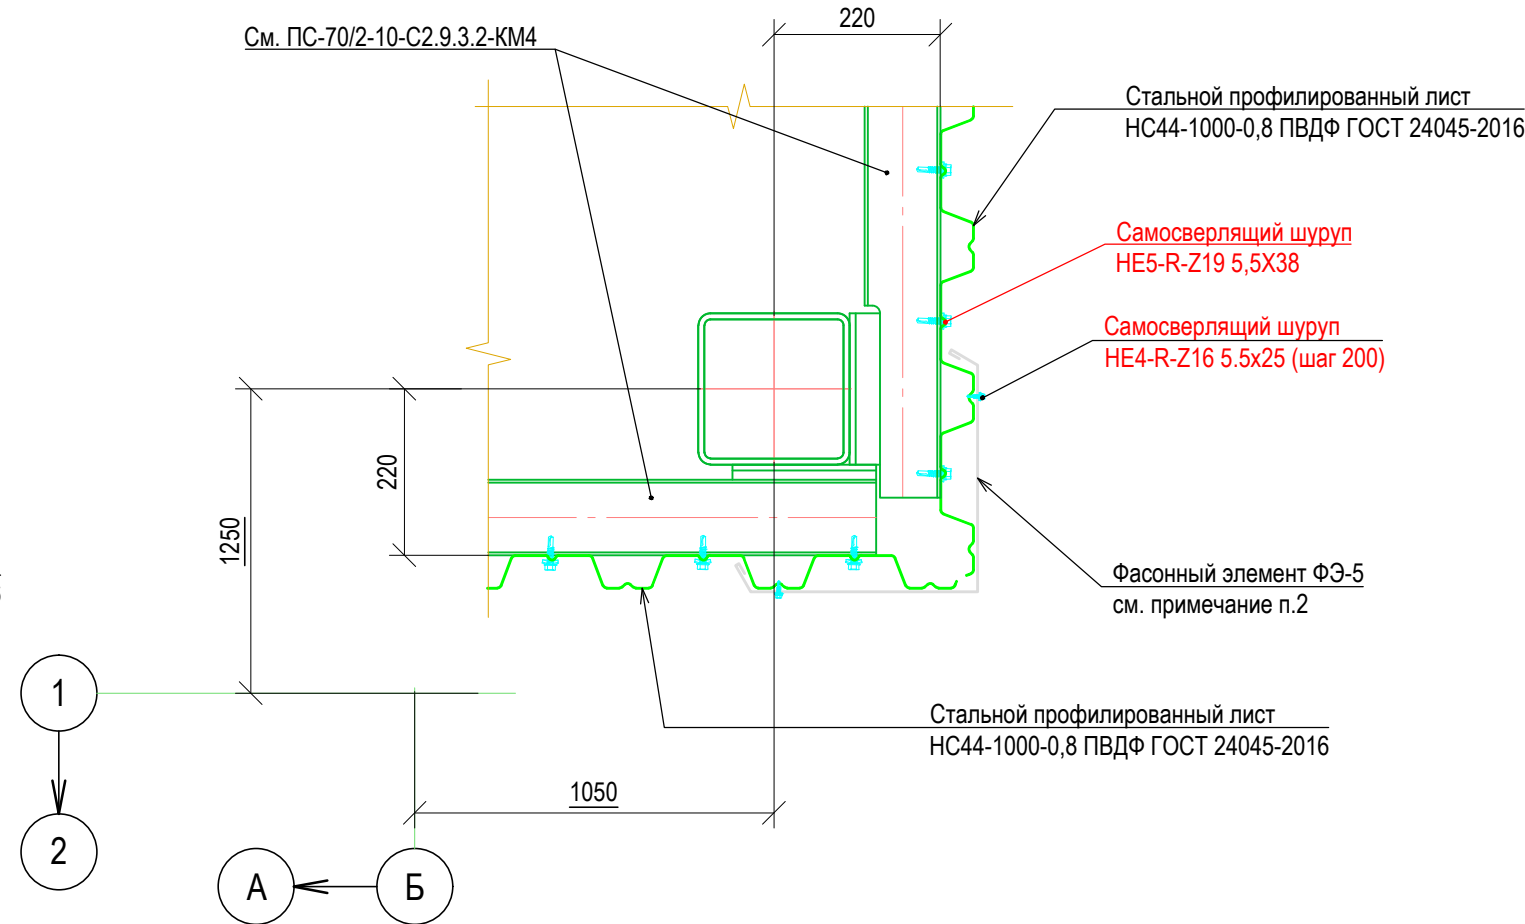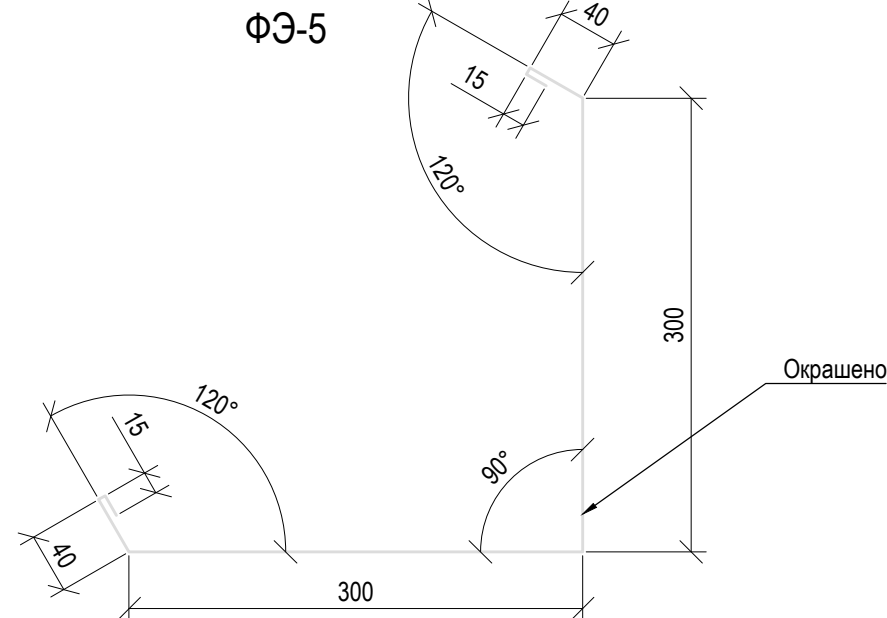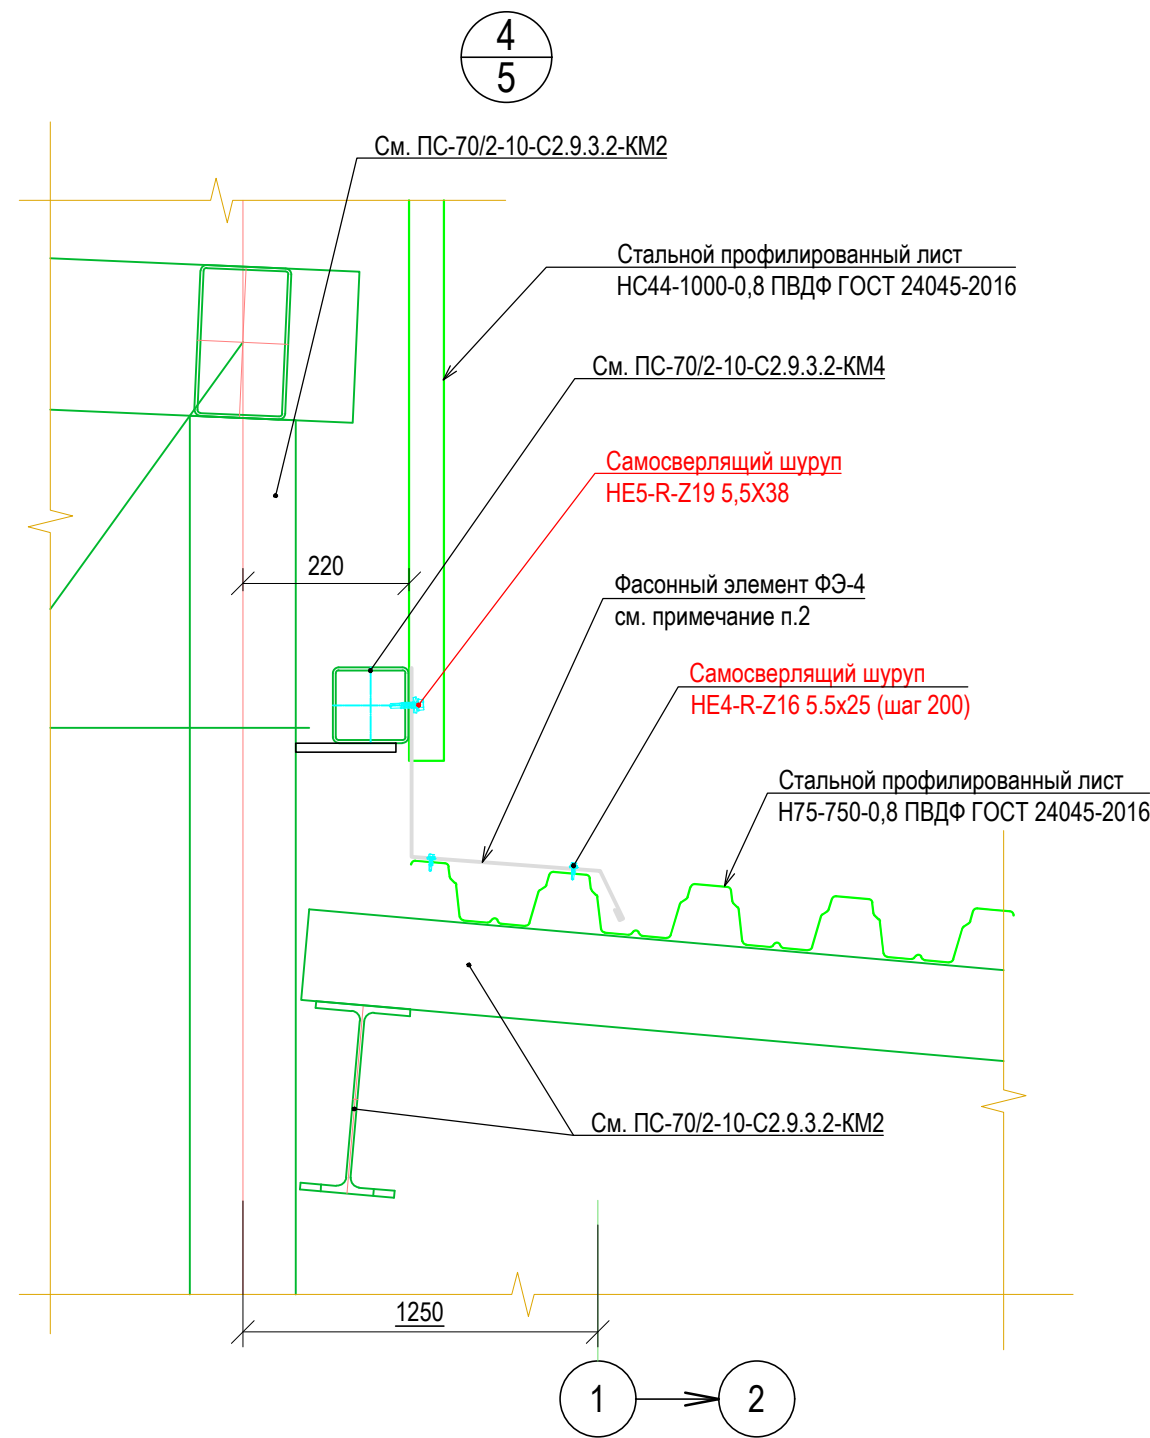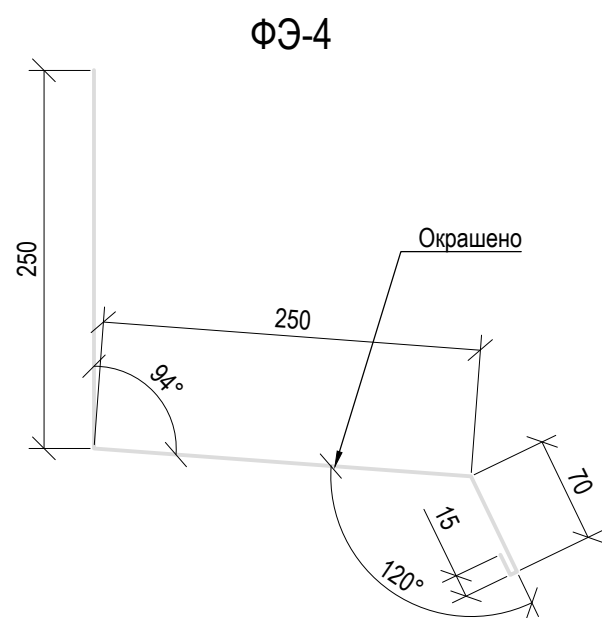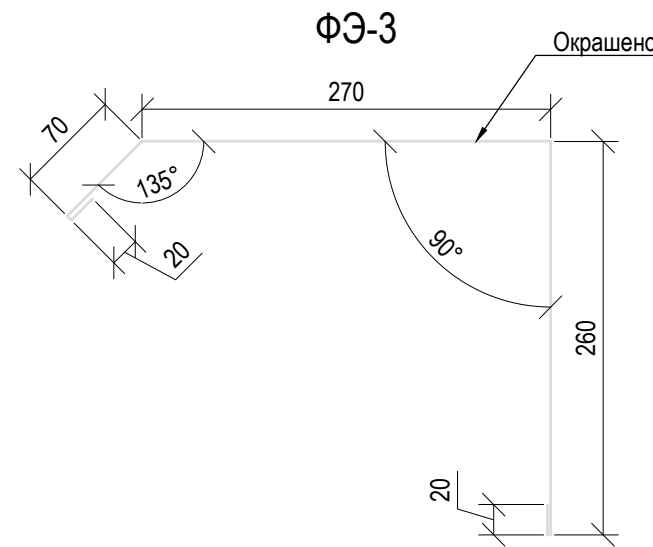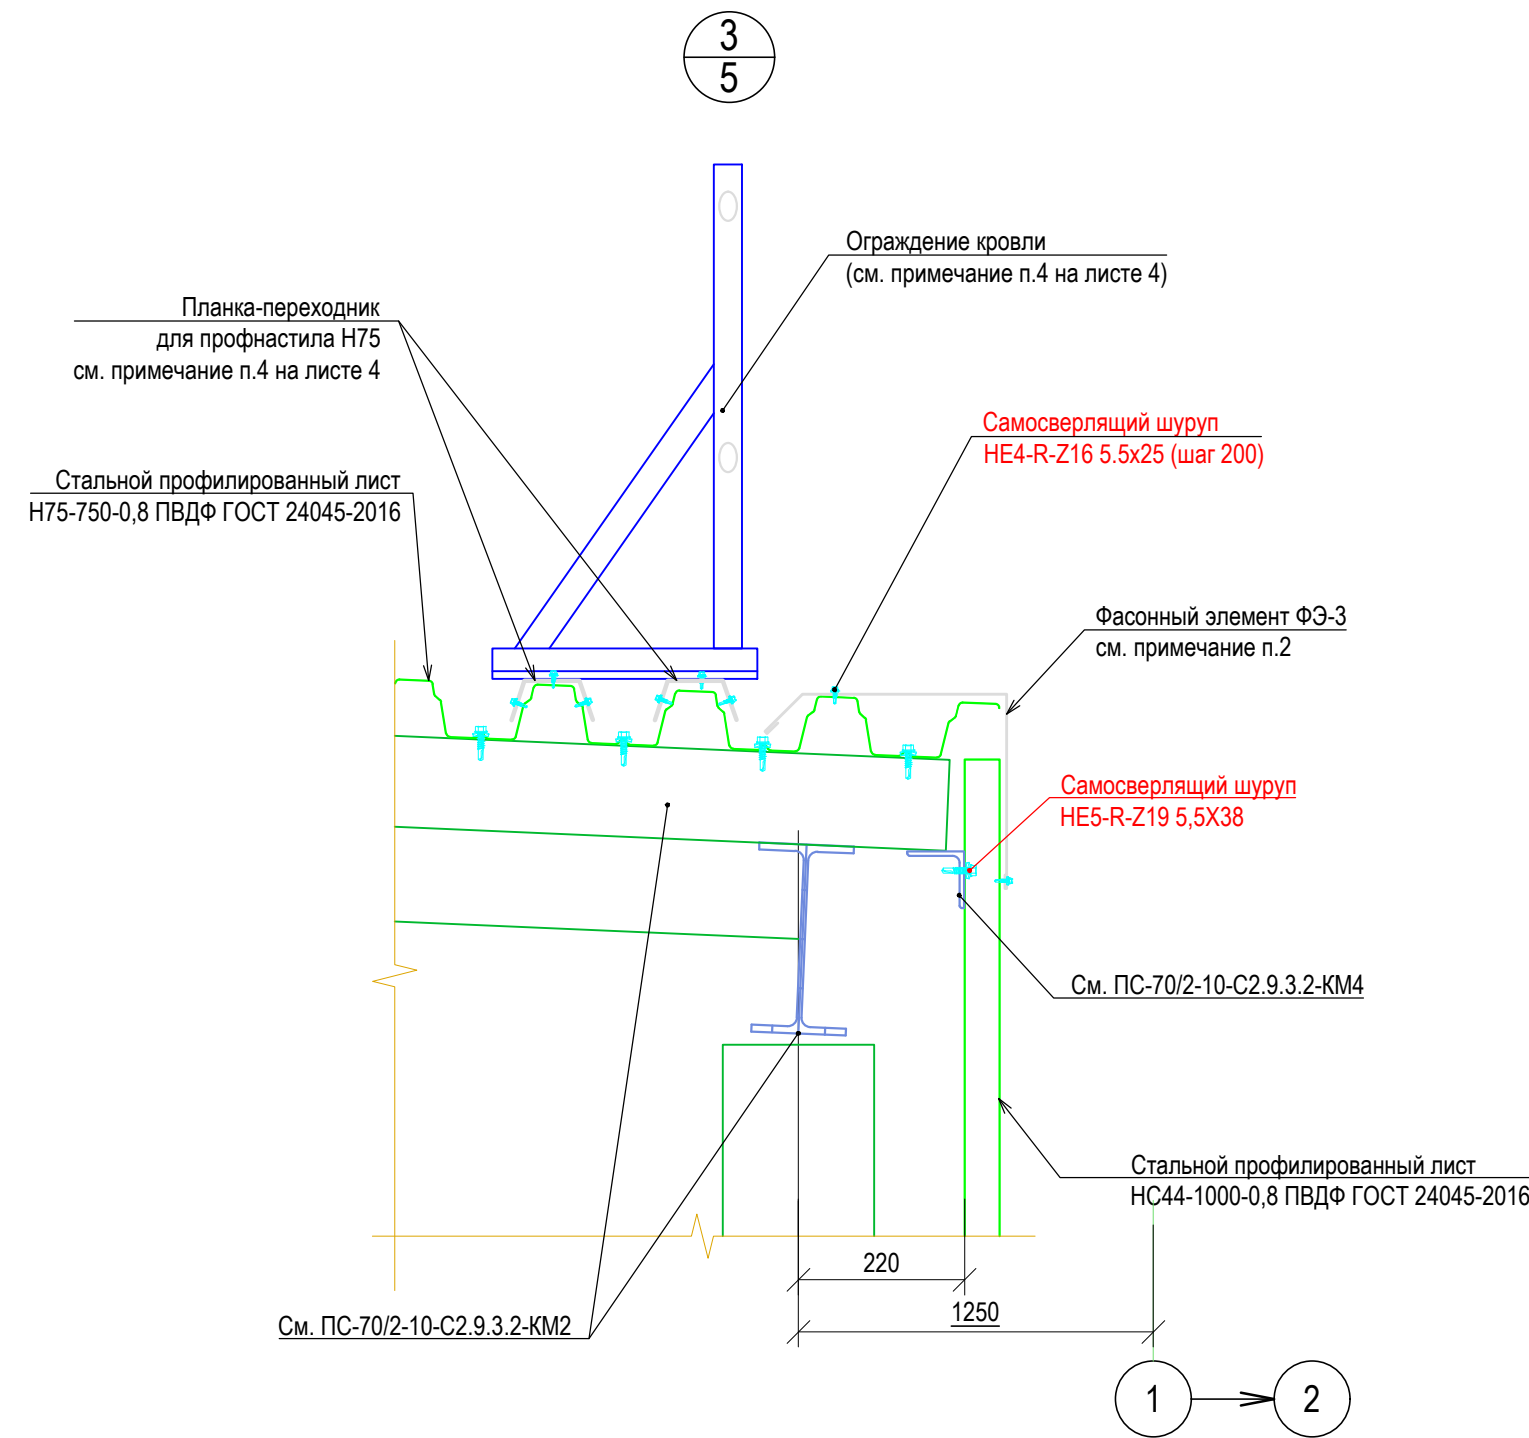

- Общие указания см. лист 2.
- Материал фасонных элементов:
Б-ПН-НО 0,7x1200 ГОСТ 14918-80
ОЦ ОН-КП(ПВДФ)/ХП-КР-УР-1/1
- Крепление фасонных элементов между собой выполнять одинарным лежащим фальцем.

						ПС-70/2-10-С2.9.3.2-АР1					
						Таманский терминал навалочных грузов.					
1	-	Зам.	1617-20		12.20	Этап 1					
Изм.	Колуч	Лист	Недок	Подпись	Дата						
Разработал	Тимофеев				05.26	Конвейерная галерея минеральных удобрений ГК-15 (тит. С2.9.3.2)		Стадия	Лист	Листов	
Проверил								Р	17		
Нач. отдела											
Н. контроль						Узлы 3-5		ООО "Гранд Вэй"			
ГИП											


Инв. N подл.	Взам. инв. N
72931220327	
Подпись и дата	11.25

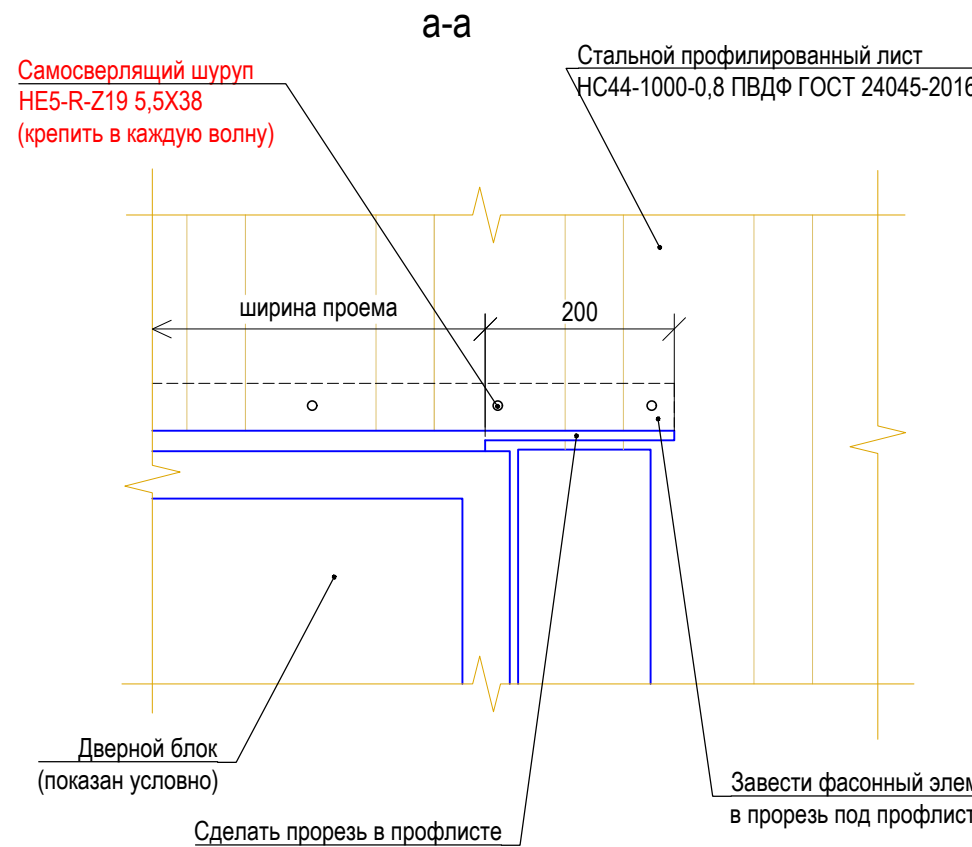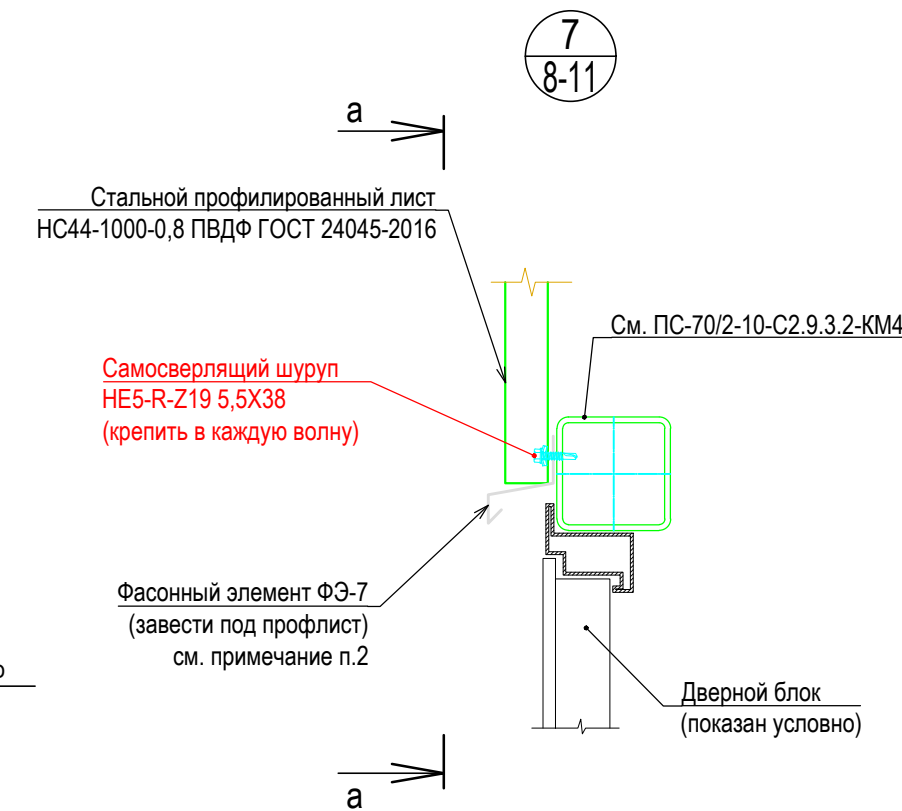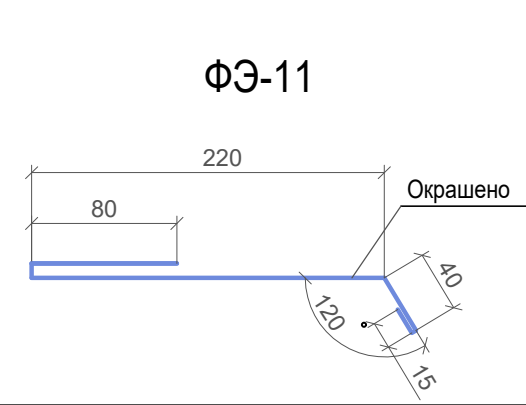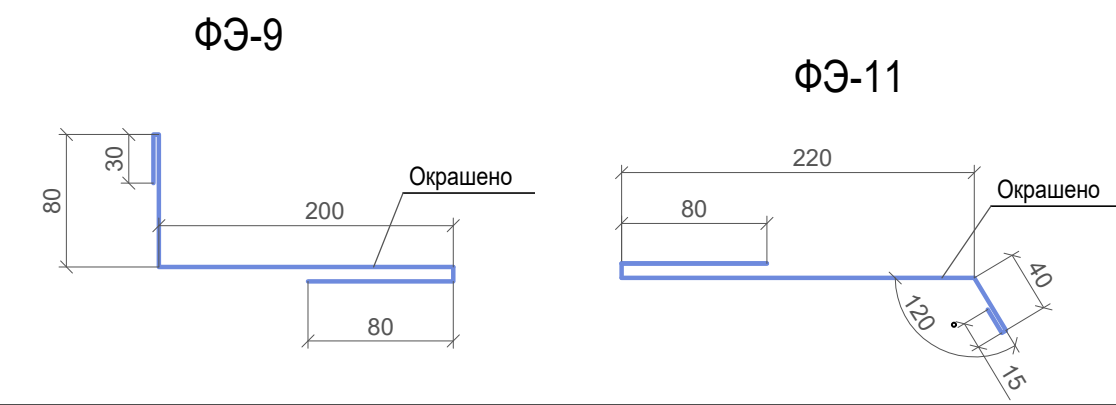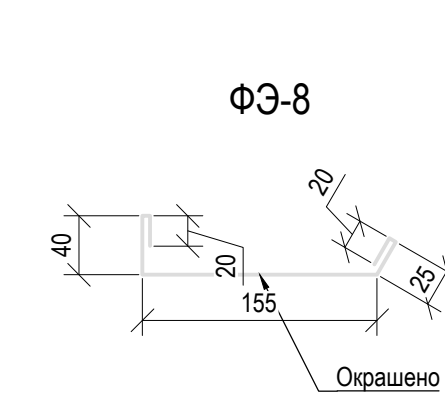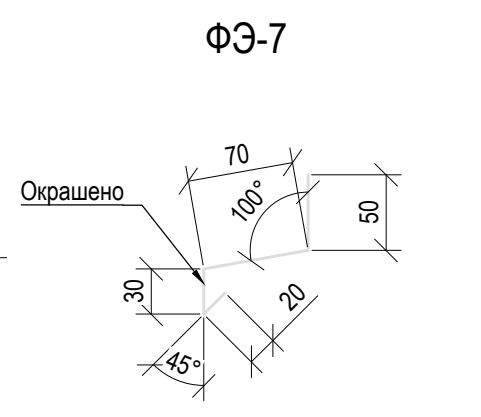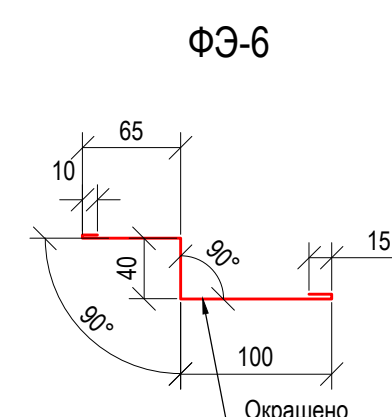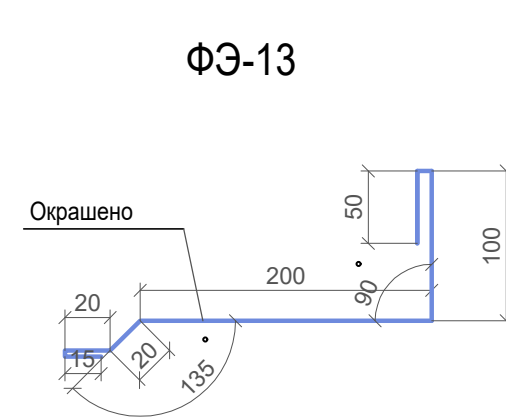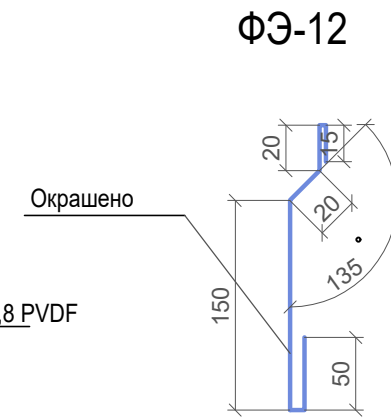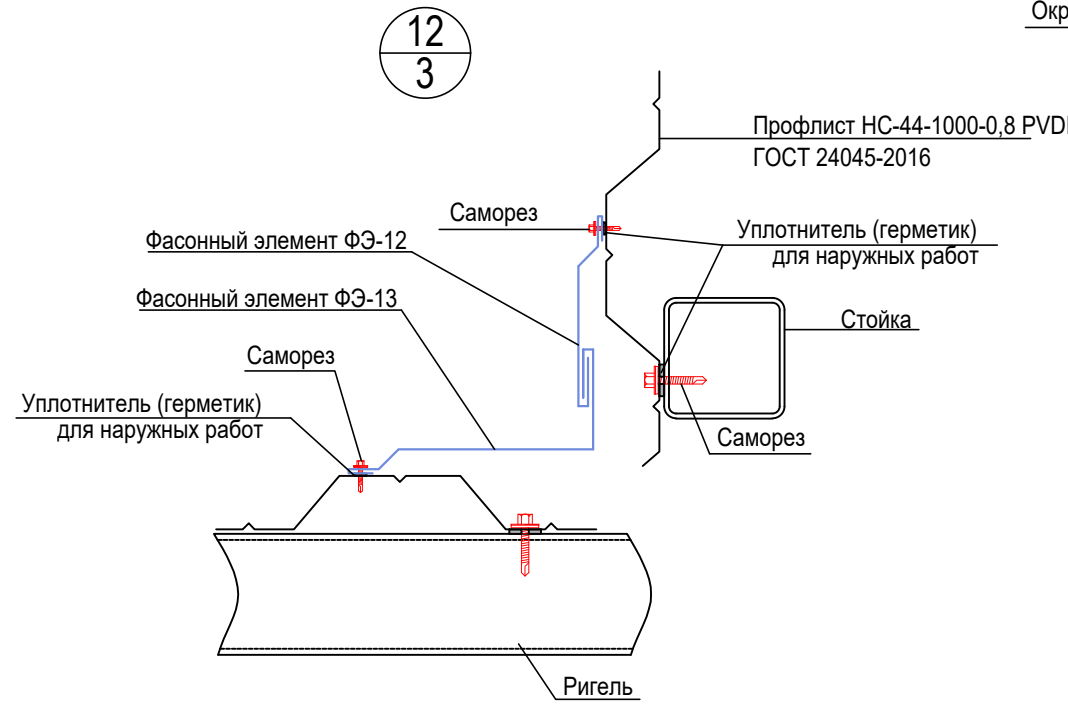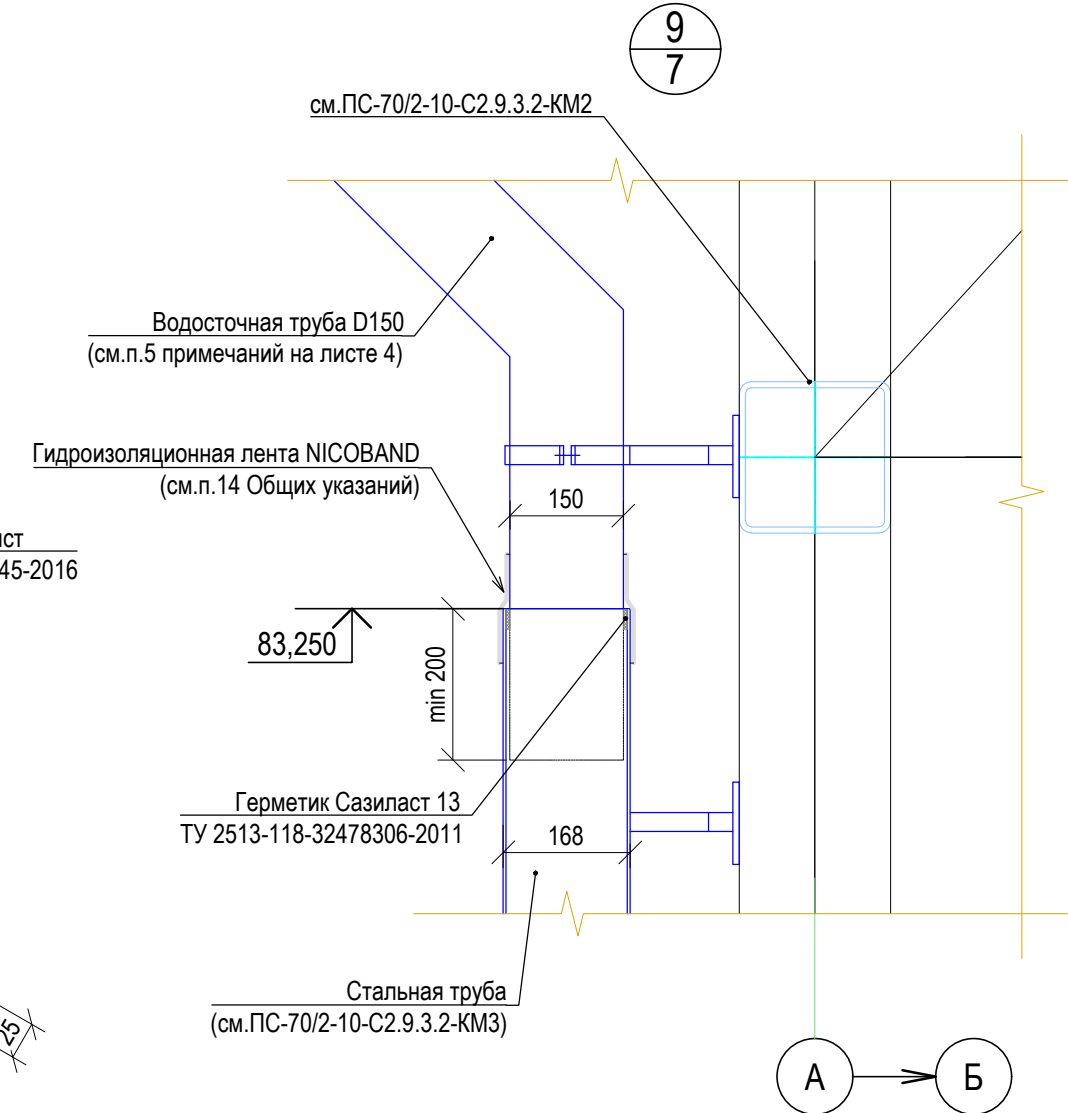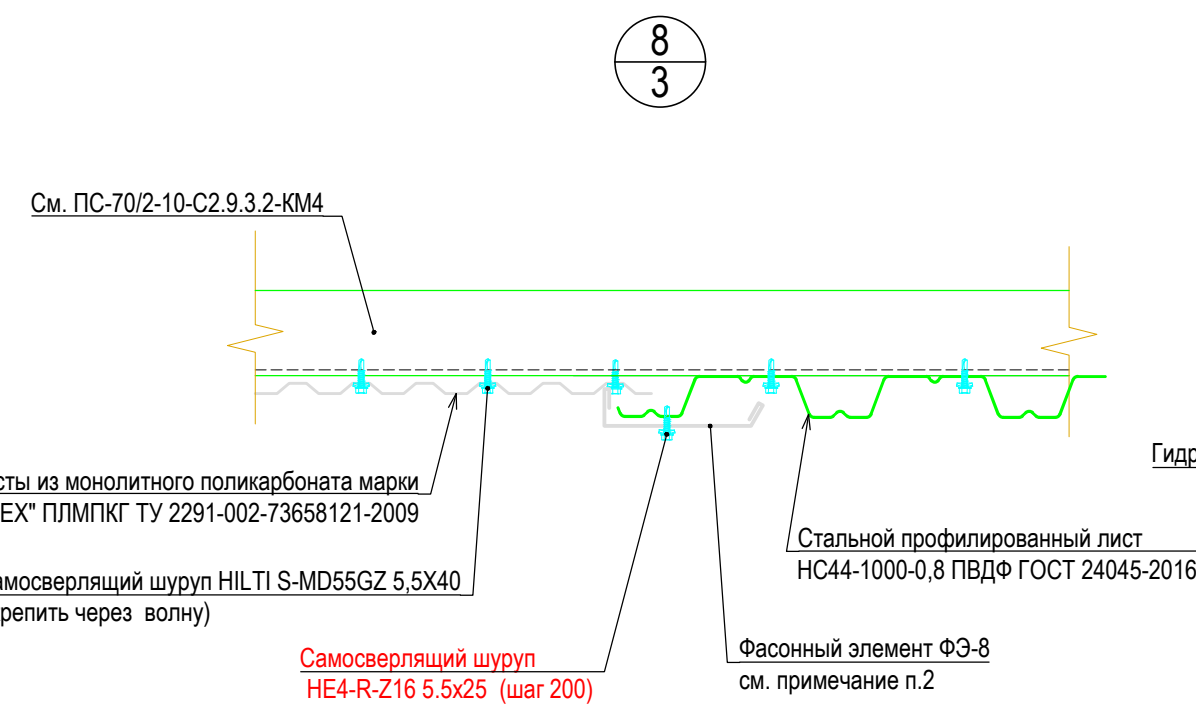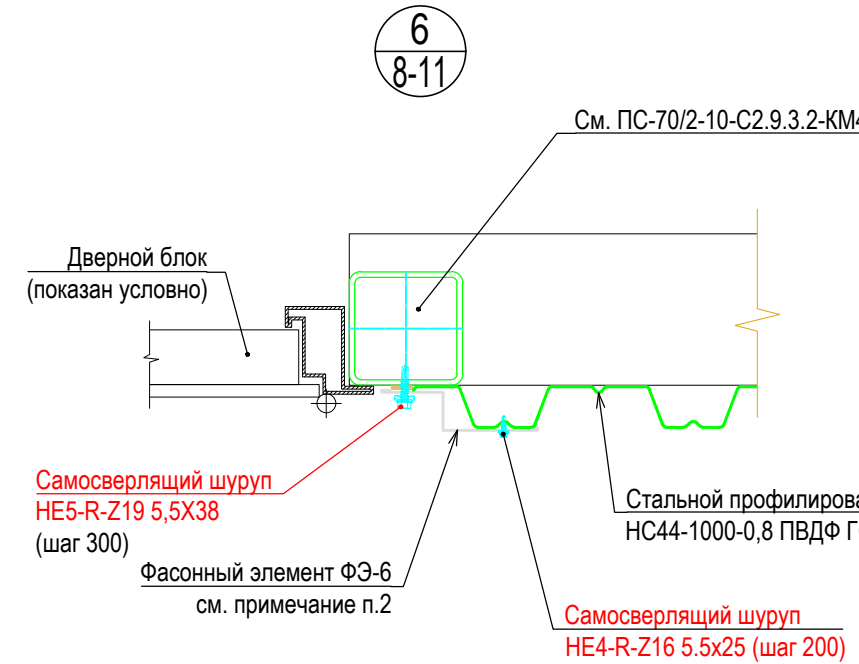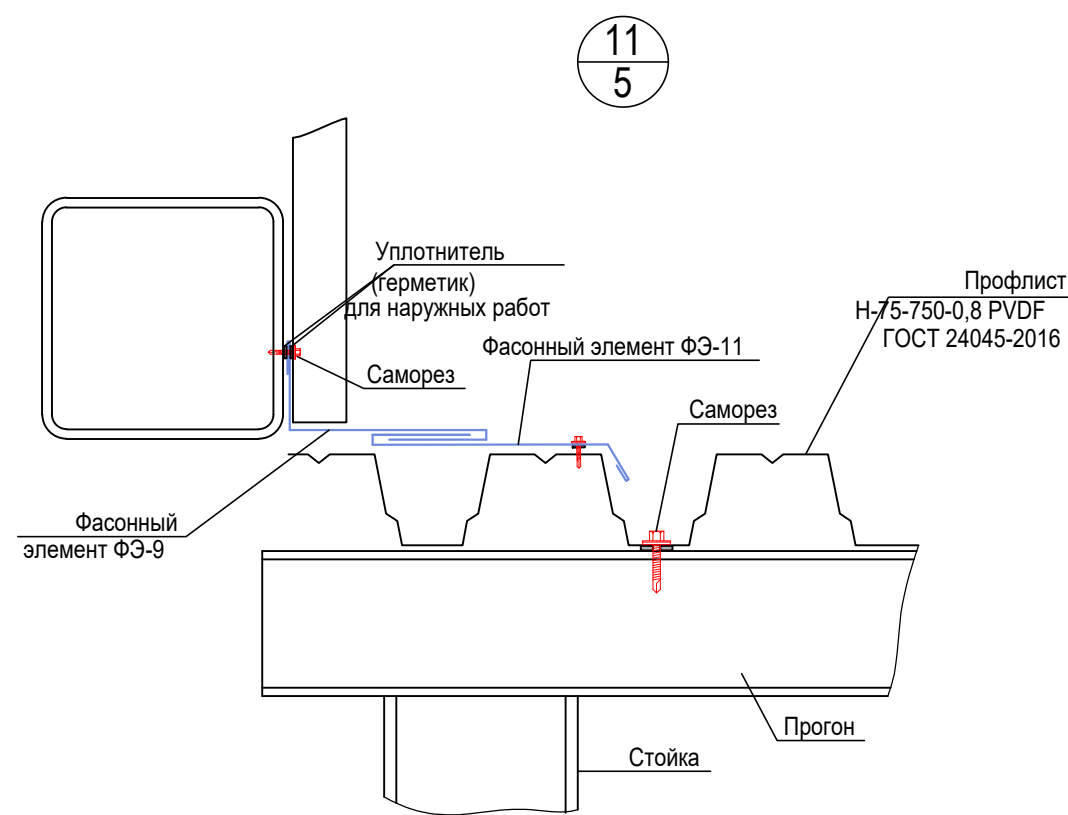

- Общие указания см. лист 2.
- Материал фасонных элементов:
Б-ПН-НО 0,7х1200 ГОСТ 14918-80
ОЦ ОН-КП(PVDF)/ХП-КР-УР-1/1
- Крепление фасонных элементов между собой выполнять одинарным лежащим фальцем.

						ПС-70/2-10-С2.9.3.2-АР1			
2	-	Зам.	439-25		12.25	Таманский терминал навалочных грузов. Этап 1			
1	-	Зам.	1617-20		12.20				
Изм.	Копуч	Лист	Недок	Подпись	Дата				
Разработал	Тимофеевко			05.26	Конвейерная галерея минеральных удобрений ГК-15 (тит. С2.9.3.2)	Стадия	Лист	Листов	
Проверил						Р	18		
Нач. отдела									
					Узлы 6-9, 11, 12	ООО "Гранд Вэй"			
Н. контроль									
ГИП									

План площадок обслуживания на отм. 78,090

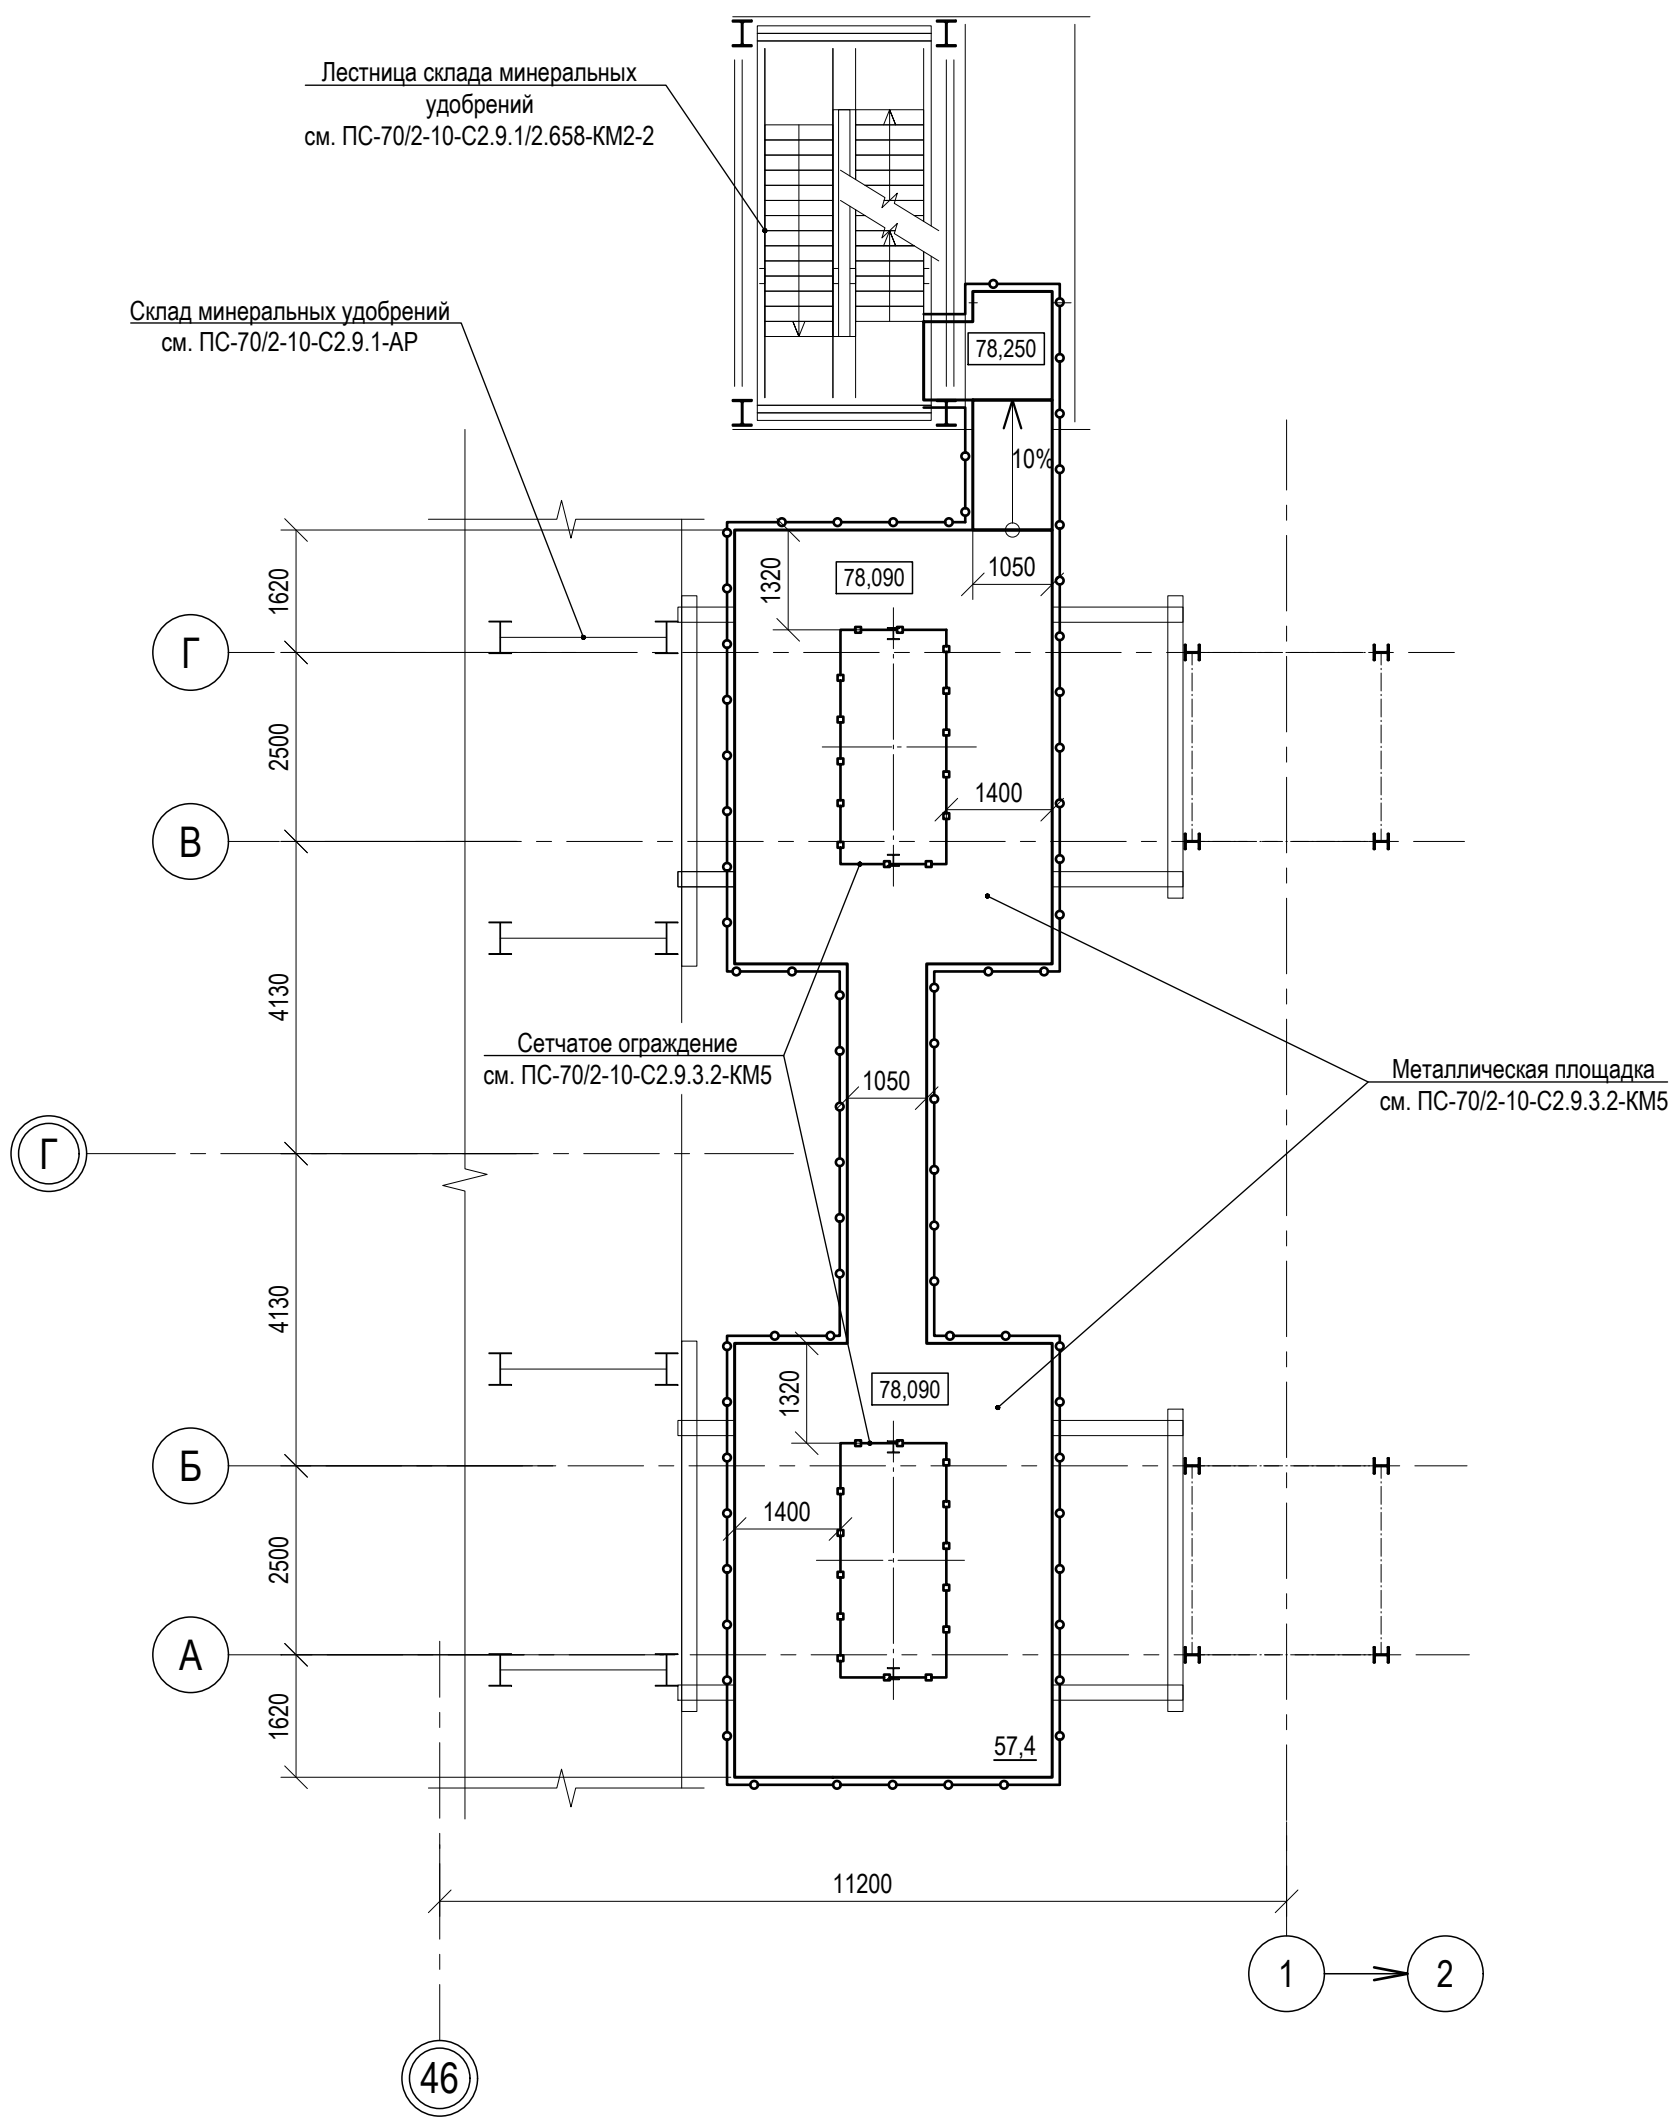


Общие указания см. лист 2.

Инов. N подл.	Подпись и дата	Взам. инв. N
7293120327		

						ПС-70/2-10-С2.9.3.2-АР1			
						Таманский терминал навалочных грузов. Этап 1			
1	-	Зам.	1617-20		12.20	Конвейерная галерея минеральных удобрений ГК-15 (тит. С2.9.3.2)			
Изм.	Колуч	Лист	Недок	Подпись	Дата				
Разработал	Божкова			12.20					
Проверил	Силина			12.20	План площадок обслуживания на отм. 78,090				
Нач. отдела	Зеленева			12.20					
					ООО "Югтерминалпроект"				
Н. контроль	Фоменкова			12.20					
ГИП	Пряников			12.20					

План площадок обслуживания на отм. 82,270

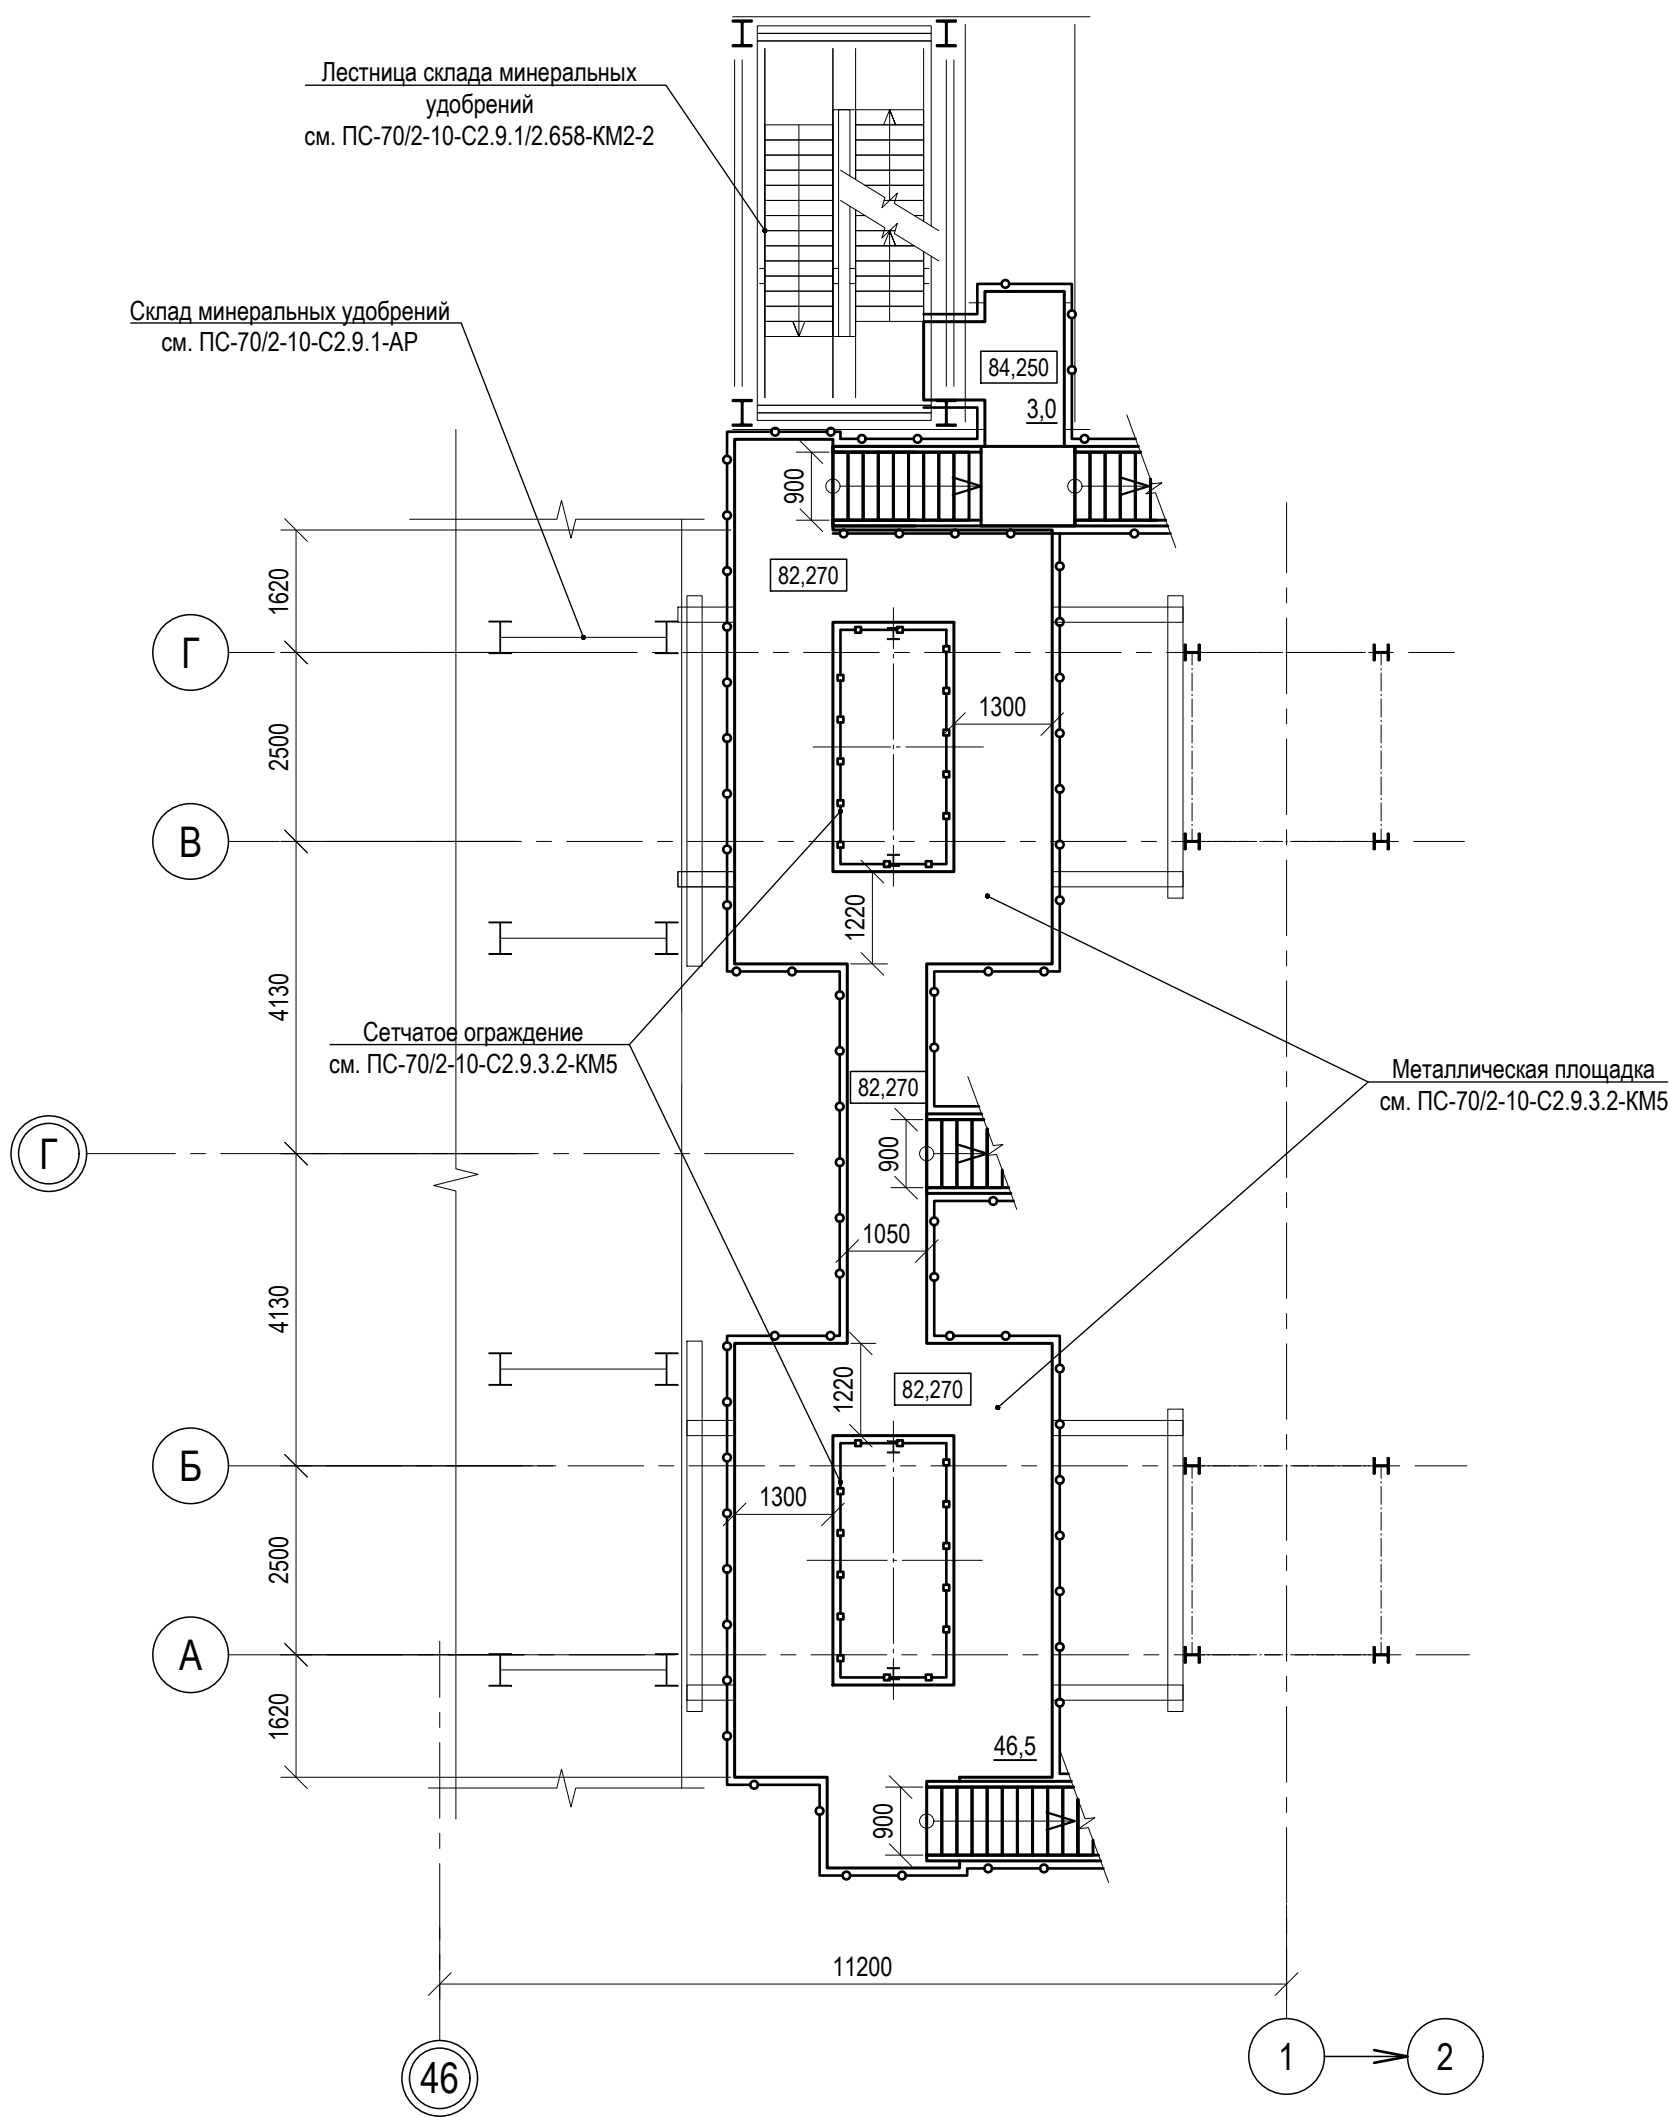

Общие указания см. лист 2.

Инов. N подл.	Подпись и дата	Взам. инв. N
7293120327		

						ПС-70/2-10-С2.9.3.2-АР1			
						Таманский терминал навалочных грузов. Этап 1			
1	-	Зам.	1617-20		12.20				
Изм.	Колуч	Лист	Недок	Подпись	Дата				
Разработал		Божкова			12.20	Конвейерная галерея минеральных удобрений ГК-15 (тит. С2.9.3.2)	Стадия	Лист	Листов
Проверил		Силина			12.20		Р	20	
Нач. отдела		Зеленева			12.20				
						План площадок обслуживания на отм. 82,270	ООО "Югтерминалпроект"		
Н. контроль		Фоменкова			12.20				
ГИП		Пряников			12.20				

Спецификация изделий и материалов

Поз.	Обозначение	Наименование	Кол.	Масса, ед., кг	Примечание
Элементы кровли					
	ТУ 5262-001-84344822-2019	Ограждение кровельное Roof Systems PRESTIGE H-600 45x25 (овал) 2 трубы EURO L=3м, RAL 9006	148		м
	ТУ 5262-001-84344822-2019	Планка-переходник для профнастила Н75	396		шт
	ТУ 22.21.41-001-36690888-2019	Уплотнитель профильный (нижний)	70		м
	ТУ 22.21.41-001-36690888-2019	Уплотнитель профильный (верхний)	70		м
	ТУ 5285-002-37144780-2012	Водосточная система "МП Проект" :			
	ТУ 5285-002-37144780-2012	Желоб водосточный D185x3000 (RAL 7047)	70		м
	ТУ 5285-002-37144780-2012	Соединитель желоба D185 (RAL 7047)	24		шт
	ТУ 5285-002-37144780-2012	Воронка выпускная D185/150 (RAL 7047)	6		шт
	ТУ 5285-002-37144780-2012	Труба водосточная D150 (RAL 7047)	42		м
	ТУ 5285-002-37144780-2012	Заглушка желоба	8		шт
	ТУ 5285-002-37144780-2012	Держатели желоба	172		шт
	ТУ 5285-002-37144780-2012	Держатели трубы водосточной	48		шт
	ТУ 5285-002-37144780-2012	Колено трубы D150 (RAL 7047) 45°	20		шт
	ТУ 2513-118-32478306-201	Герметик Сазиласт 13	3		м
	СТО 72746455-3.1.6-2014	Гидроизоляционная самоклеящаяся битумно-полимерная лента NICOBAND	15		м
Фасонные элементы					
ФЭ-1.1	ГОСТ 14918-80	Фасонный элемент ФЭ-1.1	70	1.87	м
ФЭ-1.2	ГОСТ 14918-80	Фасонный элемент ФЭ-1.2	70	0.94	м
ФЭ-2.1	ГОСТ 14918-80	Фасонный элемент ФЭ-2.1	70	0.74	м
ФЭ-2.2	ГОСТ 14918-80	Фасонный элемент ФЭ-2.2	70	3.08	м
ФЭ-3	ГОСТ 14918-80	Фасонный элемент ФЭ-3	5.4	3.52	м
ФЭ-4	ГОСТ 14918-80	Фасонный элемент ФЭ-4	5.4	3.22	м
ФЭ-5	ГОСТ 14918-80	Фасонный элемент ФЭ-5	5.4	3.91	м
ФЭ-6	ГОСТ 14918-80	Фасонный элемент ФЭ-6	8.4	1.27	м
ФЭ-7	ГОСТ 14918-80	Фасонный элемент ФЭ-7	6	0.94	м
ФЭ-8	ГОСТ 14918-80	Фасонный элемент ФЭ-8	335	1.43	м
ФЭ-9	ГОСТ 14918-80	Фасонный элемент ФЭ-9	10.8	2.15	м
ФЭ-10	ГОСТ 14918-80	Фасонный элемент ФЭ-10	4	0.81	шт
ФЭ-11	ГОСТ 14918-80	Фасонный элемент ФЭ-11	10.8	1.95	м
ФЭ-12	ГОСТ 14918-80	Фасонный элемент ФЭ-12	29.6	1.43	м
ФЭ-13	ГОСТ 14918-80	Фасонный элемент ФЭ-13	29.6	2.22	м

1. Общие указания см. лист 2.
2. Длины фасонных элементов указаны без учета нахлестов.
3. Изделия и материалы, указанные в спецификации, допускается заменять аналогом с соответствующими характеристиками.

						ПС-70/2-10-C2.9.3.2-AP1				
2	-	Зам.	439-25		12.25	Таманский терминал навалочных грузов. Этап 1				
1	-	Зам.	1617-20		12.20					
Изм.	Колуч	Лист	Недок	Подпись	Дата					
Разработал		Недев			12.25	Конвейерная галерея минеральных удобрений ГК-15 (тит. С2.9.3.2)		Стадия	Лист	Листов
Проверил		Зырянов			12.25			Р	21	
Нач. отдела		Зеленева			12.25					
						Спецификация изделий и материалов		ООО "Югтерминалпроект"		
Н. контроль		Парфёнов			12.25					
ГИП		Пряников			12.25					

Изм. N подл.	Подпись и дата	Взам. инв. N
7293120327	11.25	